

Министерство науки и высшего образования российской федерации
Федеральное государственное автономное образовательное учреждение
Высшего образования
(Уральский федеральный университет
ИМЕНИ ПЕРВОГО ПРЕЗИДЕНТА РОССИИ Б.Н.ЕЛЬЦИНА)
Институт Строительства и Архитектуры
Кафедра Промышленного , гражданского строительства
и экспертизы недвижимости

ПОС Разработка строительных генеральных планов на возведение 21-этажного жилого дома (секция В5.1) по ул.
Василия Малкова в г. Тюмень(1)

Проектный практикум 6
По направлению 08.03.01 строительство

Д.ИСА.08.03.01.06201102.ПОС.26.ГЧ

Руководитель Проекта:	_____	Бадрн Хазем Хешам	СТ-420004
Заказчик:	_____	Машкин Олег Владимирович	
Главный Куратор Проекта:	_____	Бессонова Ольга Александровна	
1- Член команды:	_____	Ибрахим Омар Мохамед	СТ-420001
2- Член команды:	_____	Мохамед Махмуд Мохамед	СТ-420003
3- Член команды:	_____	Кадейл Мохаймен Мохамед	СТ-420003
4- Член команды:	_____	Мохамед Кхалед Ибрагим	СТ-420002

Условные обозначения		
№	Максировка	Пояснение
1		Контуры строящегося здания
2		Площадка складирования
3		Контейнер ТБО
4		Зона работы крана
5		Опасная зона работы крана
6		Временная зона работы крана
7		Направление движения строительного транспорта (одностороннее)
8		Направление движения строительного транспорта (двустороннее)
9		Направление движения рабочих к местам производства работ
10		Временное защитно-ограждение строительной площадки
11		Пешеходные дорожки
12		Временные дороги в опасной зоне работы крана
13		Временные дороги в рабочей зоне работы крана
14		Защитный козырек
15		Пункт мойки колес
16		Закрытый склад
17		Открытый склад
18		Склад под навесом
19		Выступ жел
20		ВЛ
21		Сеть водопроводная постоянная существующая
22		ВЛ пр
23		Сеть водопроводная постоянная проектируемая
24		Сеть водопроводная временная
25		Канализационная линия постоянная существующая
26		Канализационная линия постоянная проектируемая
27		Канализационная линия временная
28		Сеть электроснабжения строительной площадки
29		Сеть электроснабжения постоянная проектируемая
30		Сеть электроснабжения временная
31		Место для курения
32		Пржектор
33		Щит распределительный
34		Трансформаторная подстанция
35		Знак ограничения скорости движения транспорта
36		Ворота строительной площадки
37		Граница проектируемого земельного участка
38		Ограждение зоны работы крана
39		Столбик стрелового крана
40		Защитная заграда для прохода людей в здание
41		Знак, предупреждающий о работе крана
42		Пастор объекта
43		Места хранения грузозахватных приспособлений и т.п.
44		Противопожарная стена
45		Водоотстойник (для сбора воды от мойки колес)

Экспликация временных зданий и сооружений				
№	Наименование	Тип	Кол-во	Размеры, м
Административные (служебные)				
1	Капота	15 Блок-контейнер	4	(12,00x3,00)
2	Кладовая	21 Блок-контейнер	1	(12,00x3,00)
3	Пост охраны	9 МКПП	3	(1,5x1,5)
Санитарно-бытовые				
4	Гардеробные (муж)	5,4 Блок-контейнер	5	(6,00x3,00)
5	Гардеробные (жен)	5,4 Блок-контейнер	2	(6,00x3,00)
6	Смешки (муж)	8,1 Блок-контейнер	3	(2,98x2,435)
7	Смешки (жен)	15,5 Блок-контейнер	3	(1,980x1,950)
8	Душевые (муж)	15,5 Блок-контейнер	1	(6,00x3,00)
9	Душевые (жен)	15,5 Блок-контейнер	1	(2,98x2,44)
10	Умывальные (муж)	5,4 Блок-контейнер	2	(1,00x1,100)
11	Умывальные (жен)	5,4 Блок-контейнер	1	(1,00x1,100)
12	Уборные (муж)	8,1 Блок-контейнер	4	(1,00x1,100)
13	Уборные (жен)	15,5 Блок-контейнер	3	(1,00x1,200)
14	Помещение для обогрева и отдыха	15,5 Блок-контейнер	3	(12,00x3,00)
15	Помещение для приема пищи	15,5 Блок-контейнер	4	(12,00x3,00)
Складские				
16	Открытый склад	-	1	(10,00 x 17,5)
17	Закрытый склад	-	-	-
18	Склад с навесом	-	1	(2,00 x 1,00)
Площадки (размеры приняты условно)				
19	Площадка для приема бетона	-	1	(10,0 x 10,0)
20	Арматурная площадка	-	1	(6,00 x 6,00)
21	Разгрузочная площадка	-	1	(15,00 x 10,00)
22	Разборные площадки	-	1	(10,00 x 10,00)

Ситуационный план



Розы ветров


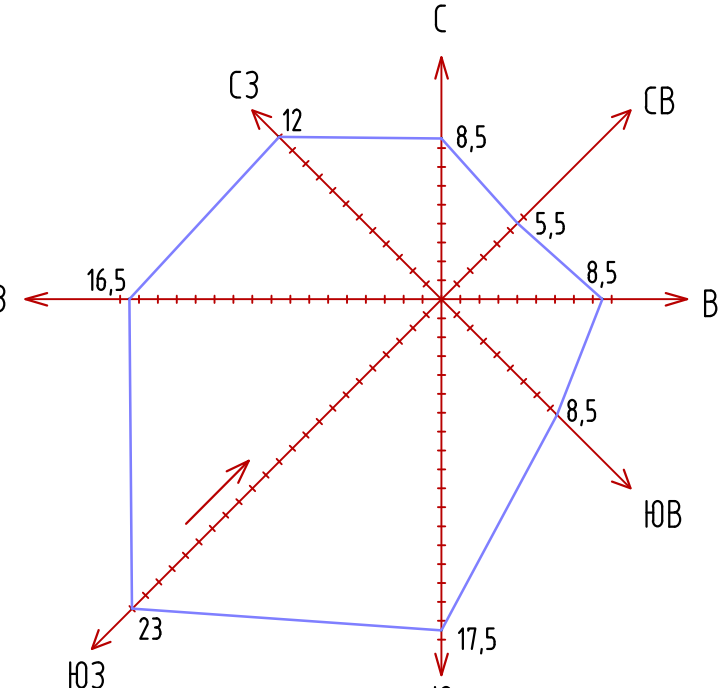



СХЕМА УСТРОЙСТВА МЕСТА ДЛЯ КУРЕНИЯ

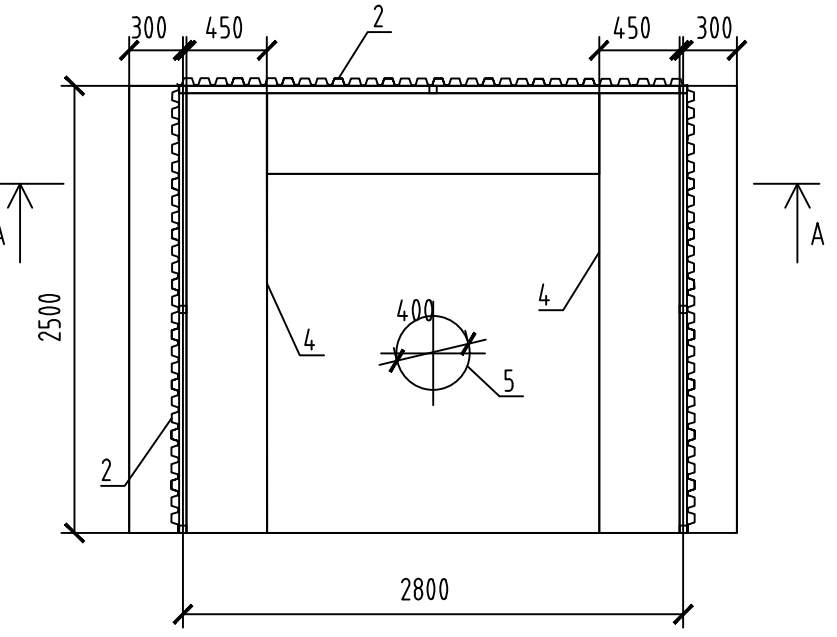

- 1 Труба квадратная 140x140 мм
- 2 Профилированный лист оцинкованный С8-1000-4,5
- 3 Бетон тяжелый, крупность заполнения 20 мм, класс В15 (М200)
- 4 Скатыва из керамических досок 28x90 мм
- 5 Зона металлическая оцинкованная


СХЕМА УСТРОЙСТВА ОГРАЖДЕНИЙ СТРОИТЕЛЬНОЙ ПЛОЩАДКИ

А. Фронтон ограждения строительной площадки без козырька

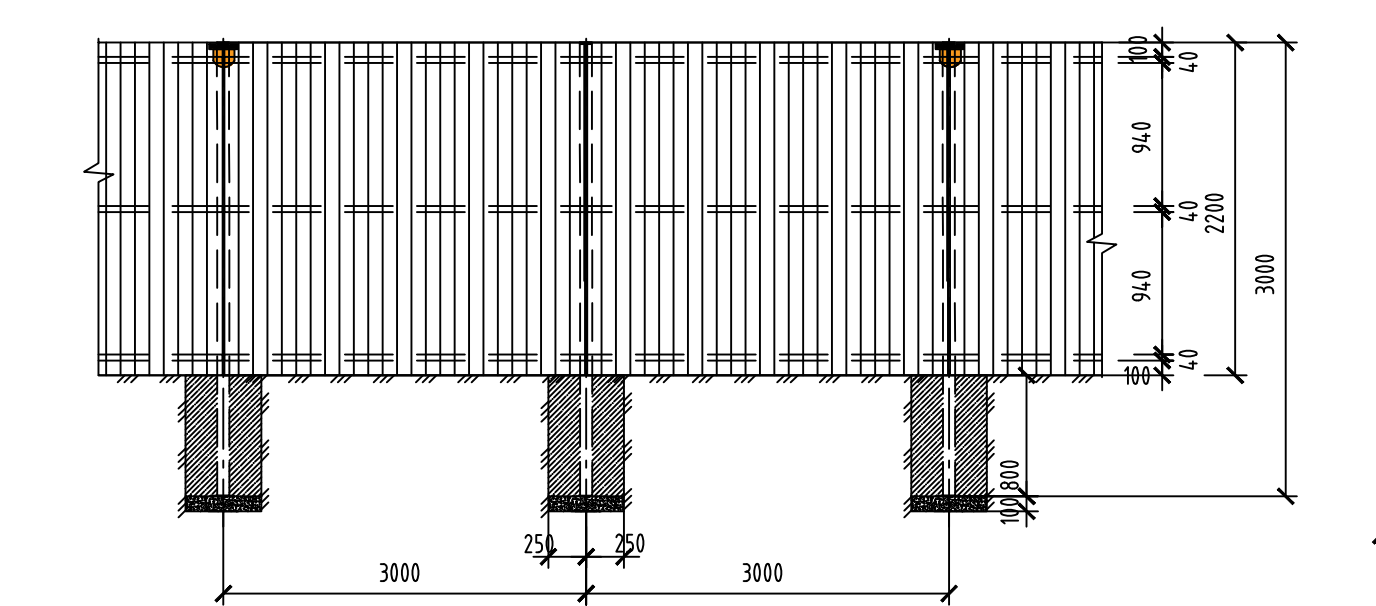

КОНСТРУКЦИЯ ВРЕМЕННЫХ ДОРОГ (ПЛОЩАДОК)

а) шириной 3,5 м, из дорожных плит

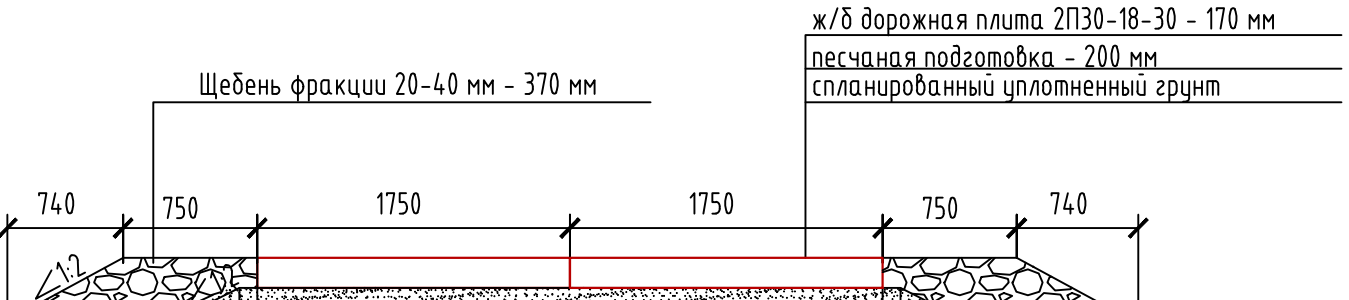

б) пешеходные дорожки и площадки

Щебень - 200 мм

Спандарбонный уплотненный грунт

Щебень - 200 мм

Спандарбонный уплотненный грунт

СХЕМА УСТРОЙСТВА ПЛОЩАДКИ ДЛЯ МОЙКИ КОЛЕС АВТОМАЦИН

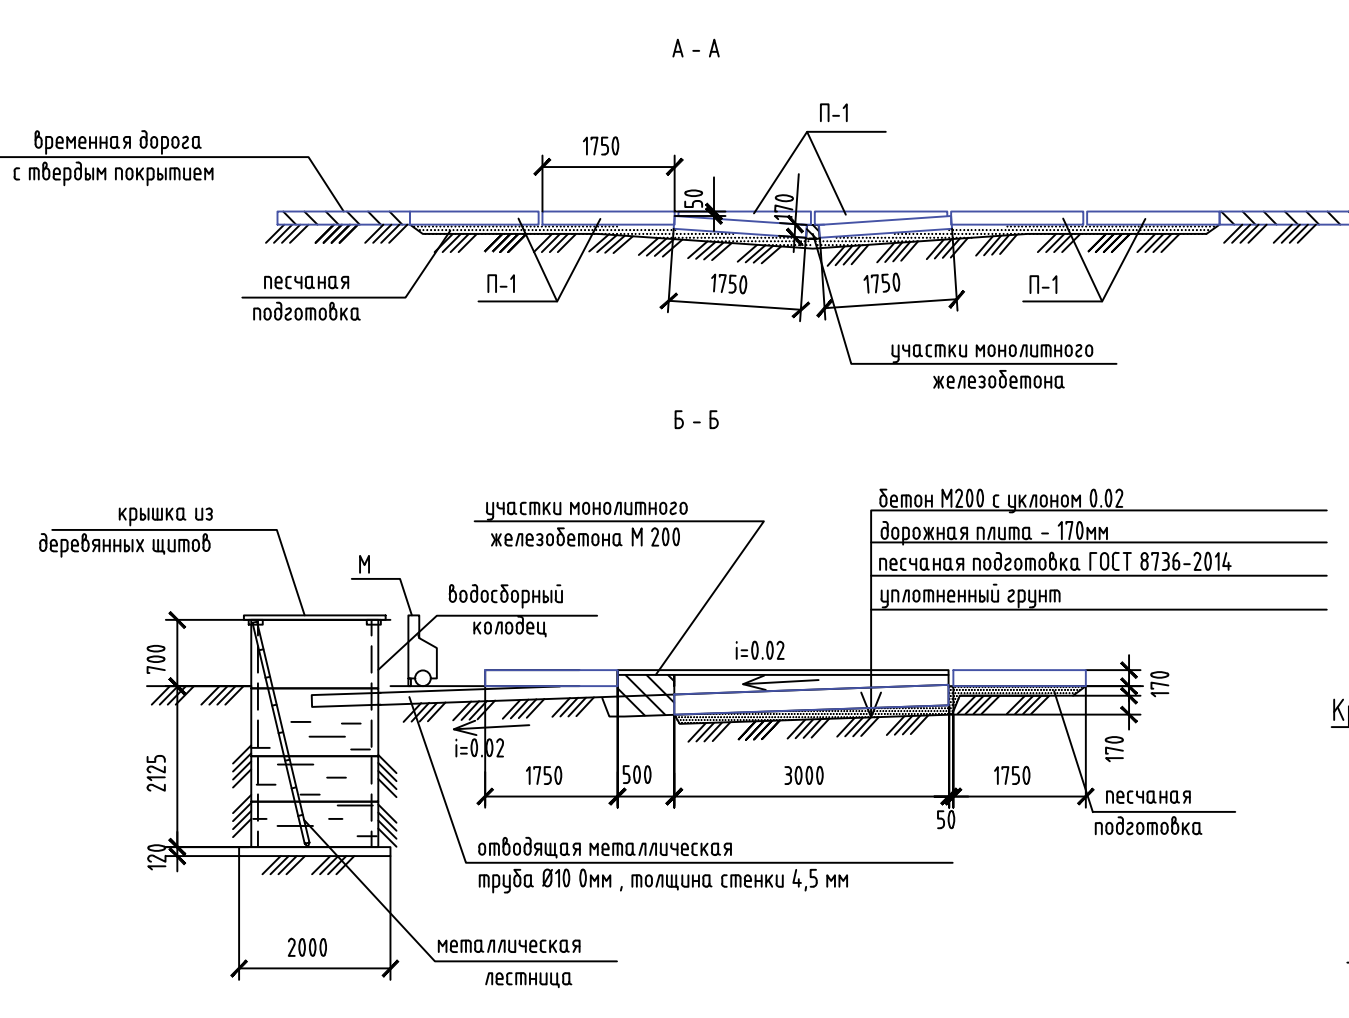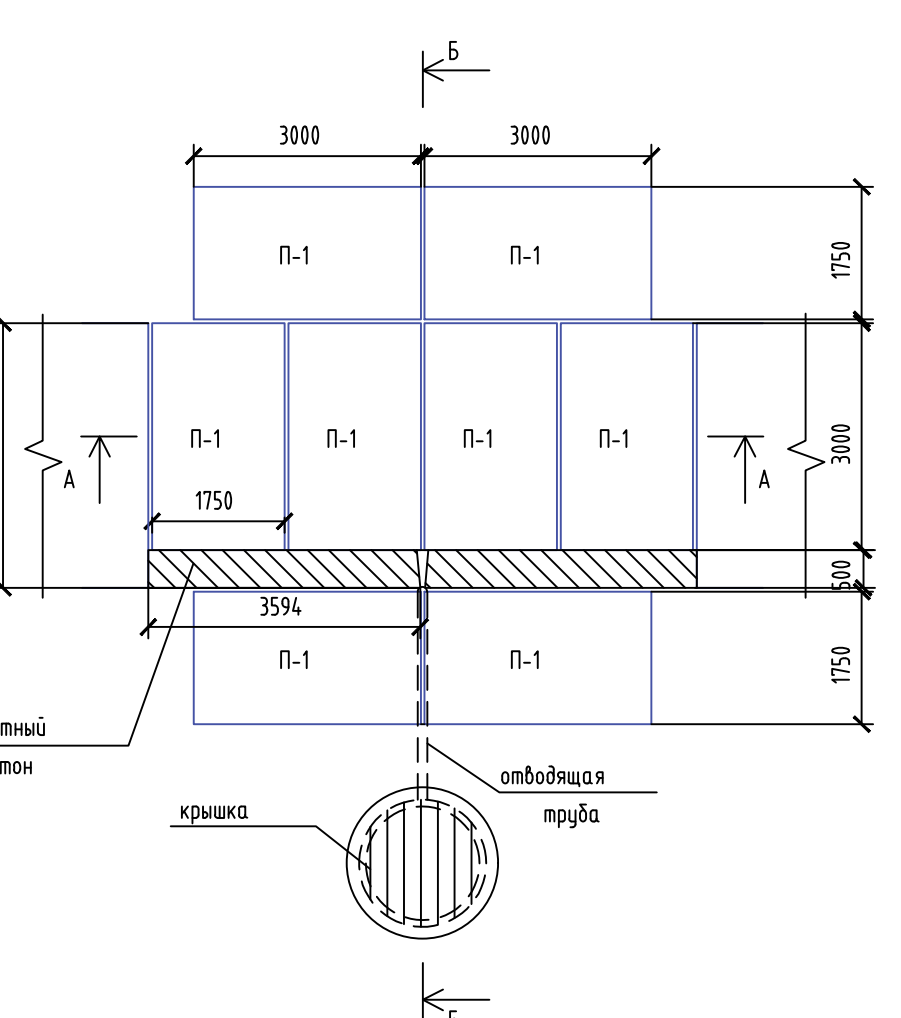


М - Мойка высокого давления, Karcher HD 9/20 classic

Строительный генеральный план

На период строительства подземной части здания

М 1:350

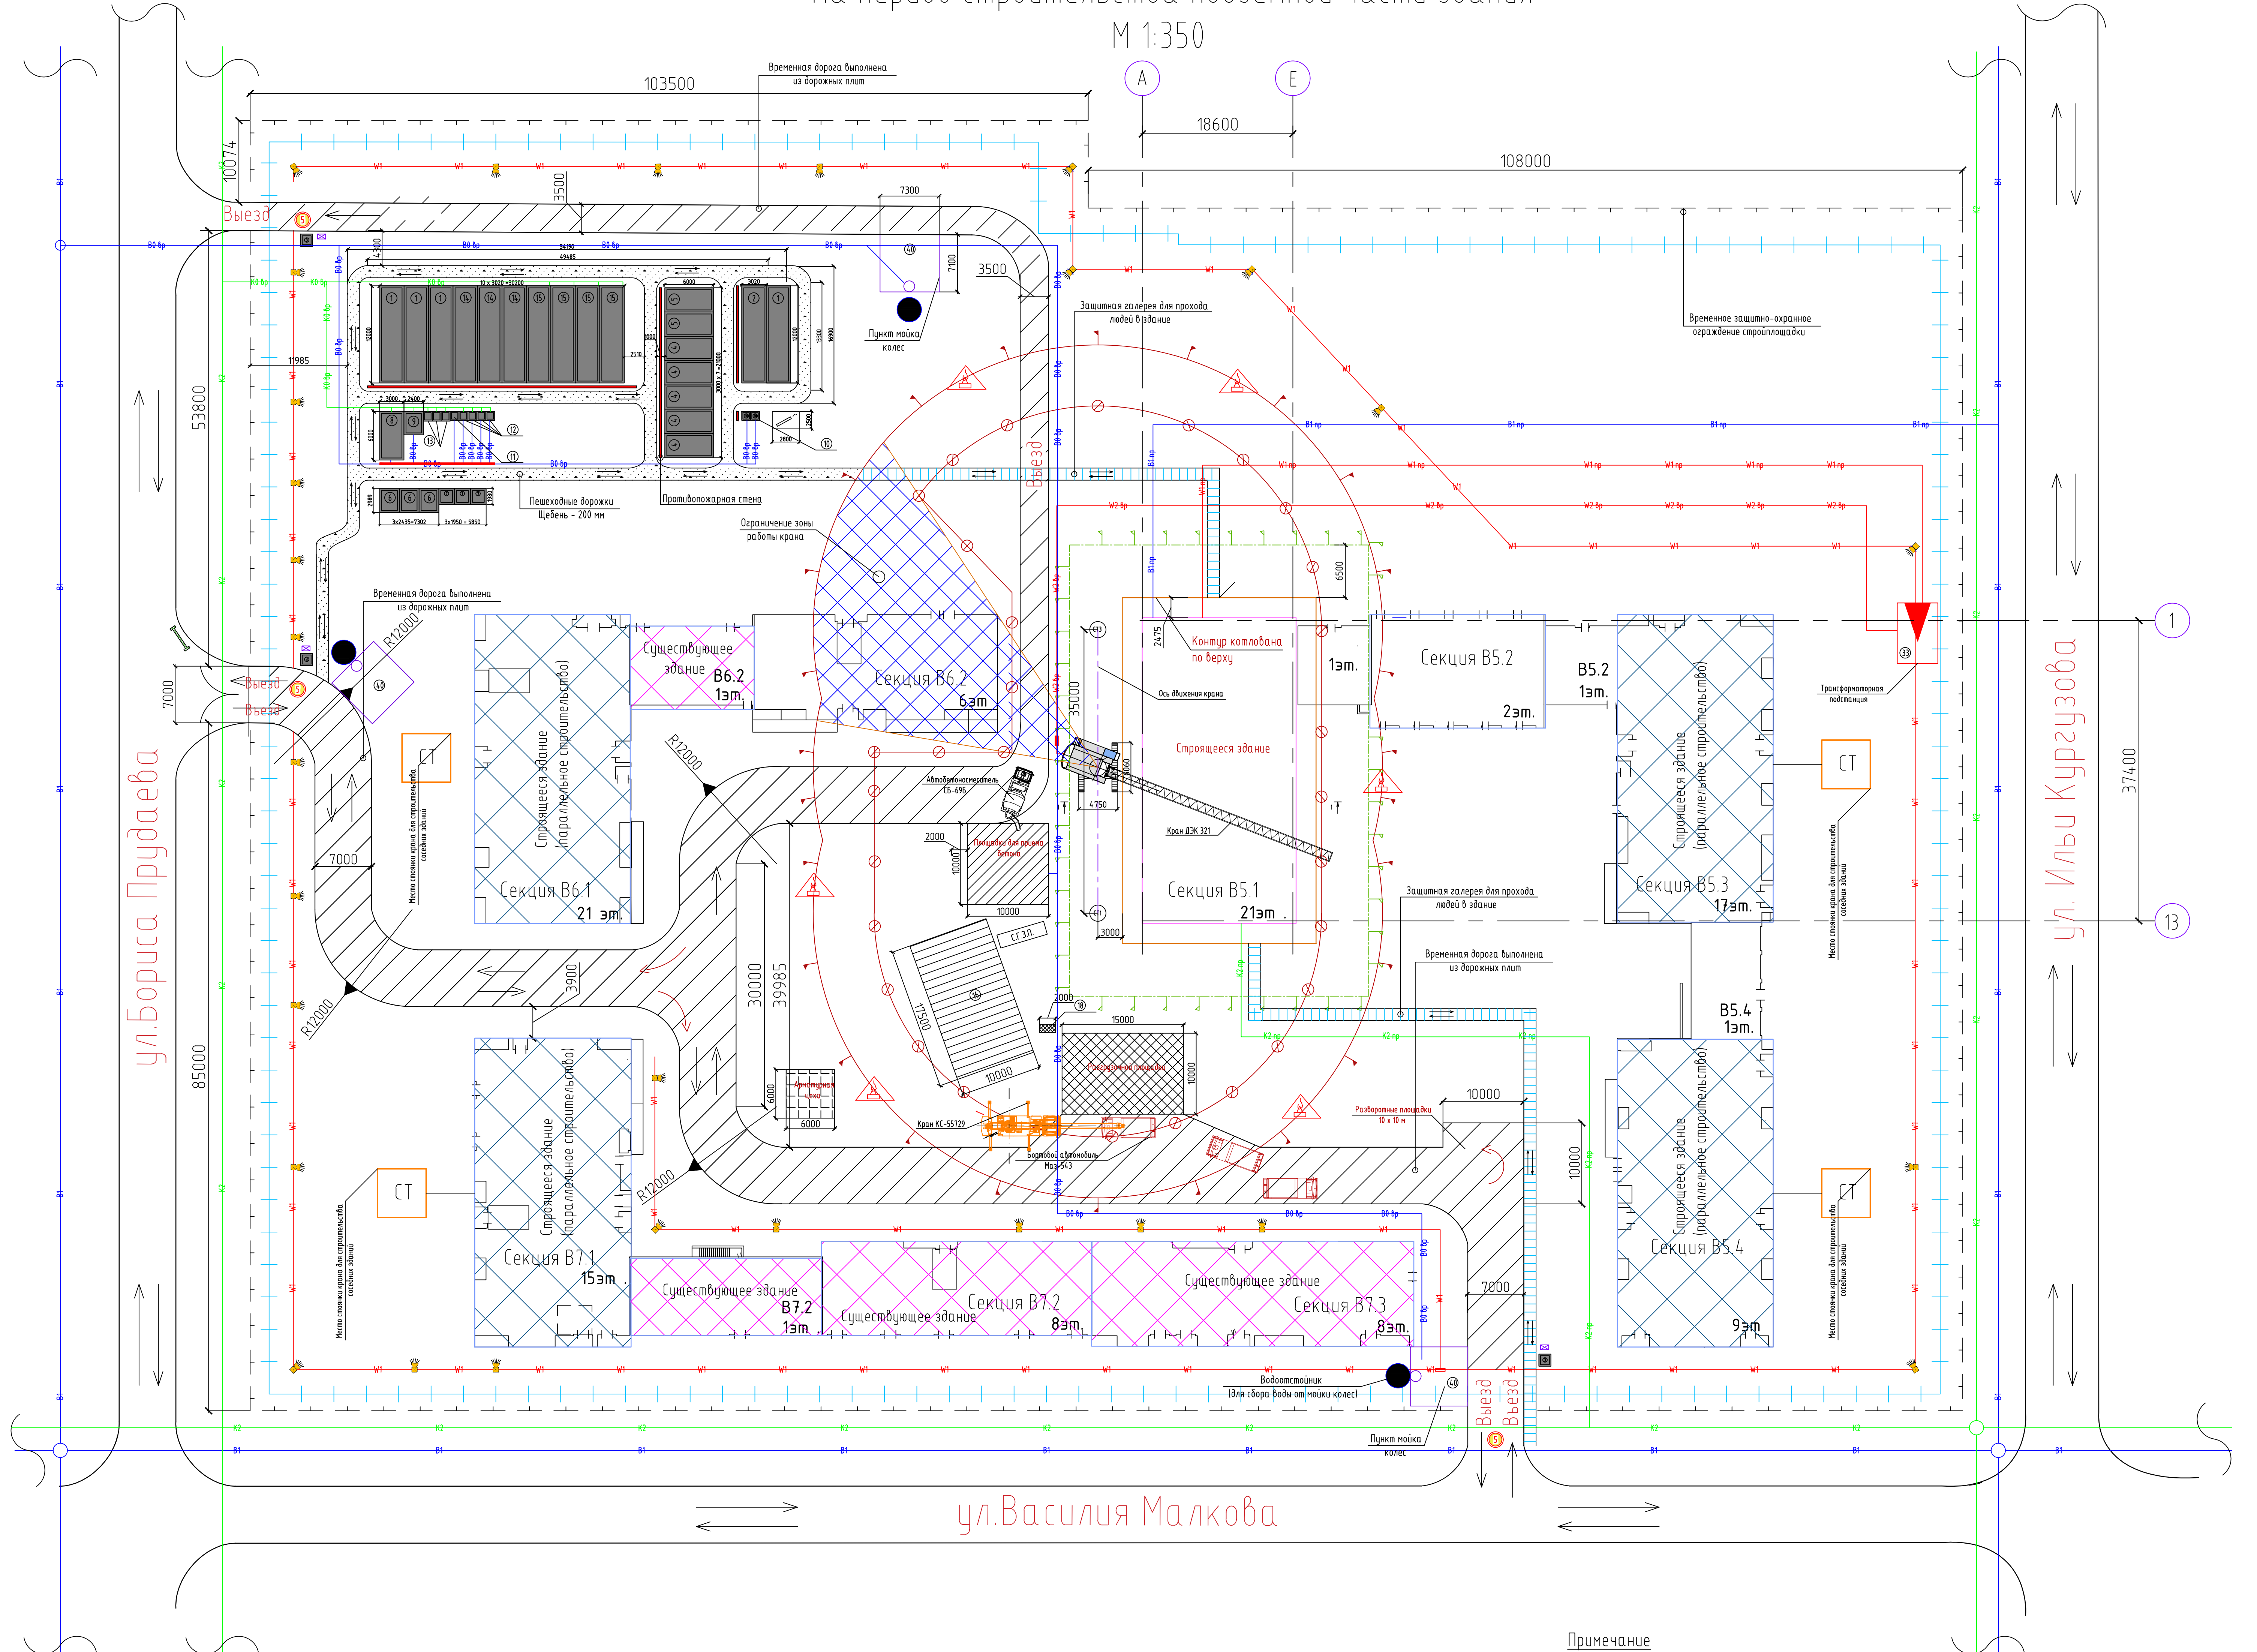

Примечание

- 1- Данный строенплан разработан для строительства подземных частей зданий
- 2- До начала строительства жилого дома должны быть выполнены подготовительные работы, в т.ч. установлено ограждение из металлического профлиста.
- 3- Электрооснащение строительной площадки выполнить подключением к существующим электрокоммуникациям. На площадке установить трансформаторную подстанцию КТП-10/10 с номинальной мощностью 100 кВт.
- 4- Складские площадки устраиваются из слоя щебня толщиной 100 мм. Площадку складирования обеспечить уклоном 3°.
- 5- У въездов на строительную площадку вывесить планы пожарной защиты с местонахождением Водоотстойника, средств пожаротушения. Каждый въездной вагончик обеспечить огнетушителями.
- 6- Подъемный краном груз на монтажном горизонте перемещать к месту установки с минимальной скоростью.
- 7- При въезде автотранспорта на строительную площадку необходимо мыть колеса. Для мойки устроить площадку.
- 8- Выполнить освещение каркаса здания и крана в ночное время.
- 9- Освещение территории производить при помощи светильников ПЭС-35.
- 10- Данный строенплан разработан для строительства подземных частей зданий.
- 11- Обеспечить круглосуточную охрану строительной площадки.
- 12- Отходы и строительный мусор своевременно вывозить на свалку.
- 13- Монтажную зону и опасную зону работы крана на местности обозначить хорошо видимыми знаками и указателями.
- 14- Скорость движения автотранспорта на площадке не должна превышать 10 км/ч на прямых участках и 5 км/ч на разворотах.
- 15- Условные обозначения приняты по прил. И СТО НОСТРОЙ 2.33.51-2011 "Организация строительного производства. Подготовка и производство строительных и монтажных работ".

И. ИСА. 08.03.014.20004. ПОС.З.2026				
ПОС - Разработка строительных генеральных планов на возведение 21-этажного жилого дома				
Имя	Имя	Лист	И. ИСА	Дата
Создатель	Бессонов О.А.	23.06.2026	23.06.2026	23.06.2026
Проверенный	Бессонов О.А.	23.06.2026	23.06.2026	23.06.2026
Утвержденный	Бессонов О.А.	23.06.2026	23.06.2026	23.06.2026
21-этажный жилой дом (секция Б5.1) по ул. Василия Малкова в г. Тюмень			Состав	Лист	Листов
Строительный генеральный план			4	1	2
Упр.У			кафедра ПГС и ЭН		

Условные обозначения		
№	Максировка	Пояснение
1		Контур строящегося здания
2		Площадка складирования
3		Контейнер Т50
4		Зона работы крана
5		Опасная зона работы крана
6		Монтажная зона здания
7		Направление движения строительного транспорта (административное)
8		Направление движения строительного транспорта (автотранспортное)
9		Направление движения рабочих к местам производства работ
10		Временное защитно-оградное ограждение строительной площадки
11		Пешеходные дорожки
12		Временные дороги в опасной зоне работы крана
13		Временные дороги в рабочей зоне работы крана
14		Защитный козырек
15		Пункт мойки колес
16		Закрытый склад
17		Открытый склад
18		Склад под навесом
19		Выступ жел
20		ВЛ
21		Сеть водопроводная постоянная существующая
22		Пожарная гидрант
23		ВЛ пр
24		Сеть водопроводная постоянная проектируемая
25		Сеть водопроводная временная
26		Канализационная линия постоянная существующая
27		Канализационная линия постоянная проектируемая
28		Канализационная линия временная
29		Сеть электроснабжения строительной площадки
30		Сеть электроснабжения постоянная проектируемая
31		Сеть электроснабжения временная
32		Место для курения
33		Проектор
34		Щит распределительный
35		Трансформаторная подстанция
36		Знак ограничения скорости движения автотранспорта
37		Ворота строительной площадки
38		Граница проектируемого земельного участка
39		Ограждение зоны работы крана
40		Стойка стрелового крана
41		Защитная заграда для прохода людей в здание
42		Знак, предупреждающий о работе крана
43		Паспорт объекта
44		Места хранения грузозахватных приспособлений и т.п.
45		Противопожарная стена
46		Водоотстойник (для сбора воды от мойки колес)

Экспликация временных зданий и сооружений				
№	Наименование	Тип	Кол-во	Размеры, м
Административные (служебные)				
1	Капота	15 Блок-контейнер	4	(12,00x3,00)
2	Кладовая	21 Блок-контейнер	1	(12,00x3,00)
3	Пост охраны	9 МКПП	3	(1,5x1,5)
Санитарно-бытовые				
4	Гардеробные (муж)	5,4 Блок-контейнер	6	(6,00x3,00)
5	Гардеробные (жен)	5,4 Блок-контейнер	3	(6,00x3,00)
6	Сушилки (муж)	8,1 Блок-контейнер	4	(2,98x2,435)
7	Сушилки (жен)	15,5 Блок-контейнер	3	(1,980x1,950)
8	Душевые (муж)	15,5 Блок-контейнер	1	(6,00x3,00)
9	Душевые (жен)	15,5 Блок-контейнер	1	(2,98x2,44)
10	Умывальные (муж)	5,4 Блок-контейнер	2	(1,00x1,100)
11	Умывальные (жен)	5,4 Блок-контейнер	1	(1,00x1,100)
12	Уборные (муж)	8,1 Блок-контейнер	6	(1,00x1,100)
13	Уборные (жен)	15,5 Блок-контейнер	5	(1,00x1,200)
14	Помещение для одевания и раздевания	15,5 Блок-контейнер	4	(12,00x3,00)
15	Помещение для приема пищи	15,5 Блок-контейнер	4	(12,00x3,00)
Складские				
16	Открытый склад	-	1	(10,00 x 3,00)
17	Закрытый склад	-	1	(6,00 x 3,00)
18	Склад с навесом	-	2	(10,00 x 16,25)
Площадки (размеры приняты условно)				
19	Площадка для приема бетона	-	1	(10,0 x 10,0)
20	Арматурная площадка	-	1	(6,00 x 6,00)
21	Разгрузочная площадка	-	1	(15,00 x 10,00)
22	Разборные площадки	-	1	(10,00 x 10,00)

Ситуационный план



Розы ветров


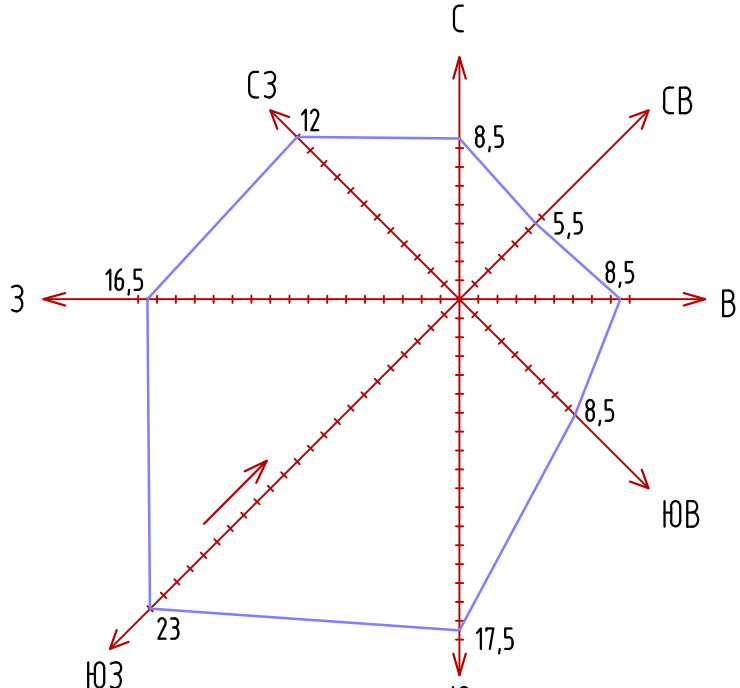



СХЕМА УСТРОЙСТВА МЕСТА ДЛЯ КУРЕНИЯ

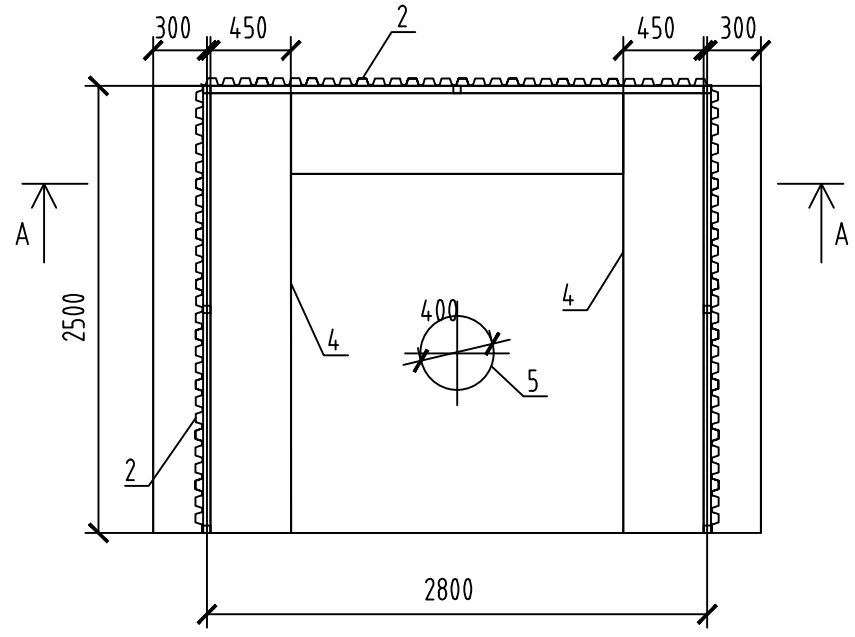

- Условные обозначения
- 1 Труба квадратная 140x140 мм
 - 2 Профилированный лист оцинкованный С8-1000-4,5
 - 3 Бетон тяжелый, крупность заполнения 20 мм, класс В15 (М20)
 - 4 Скатывающиеся деревянные доски 28x90 мм
 - 5 Зона металлического ограждения


СХЕМА УСТРОЙСТВА ОГРАЖДЕНИЙ СТРОИТЕЛЬНОЙ ПЛОЩАДКИ

А. Фронтон ограждения строительной площадки без козырька

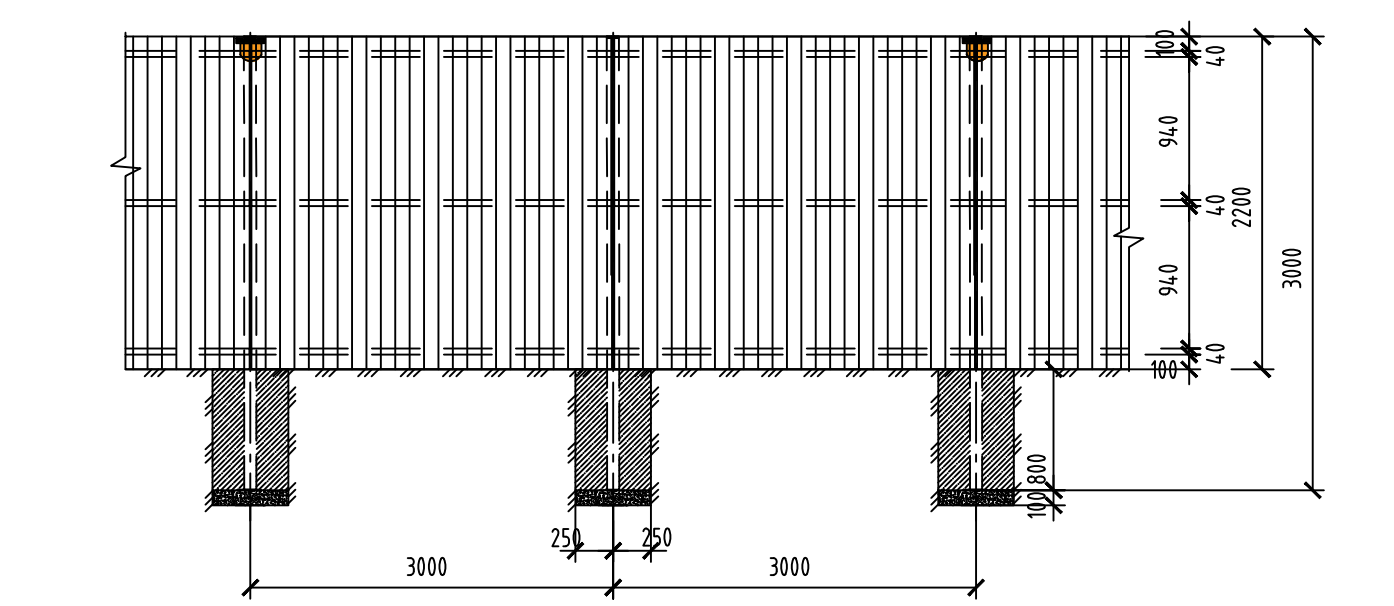

КОНСТРУКЦИЯ ВРЕМЕННЫХ ДОРОГ (ПЛОЩАДОК)

а) шириной 3,5 м, из дорожных плит

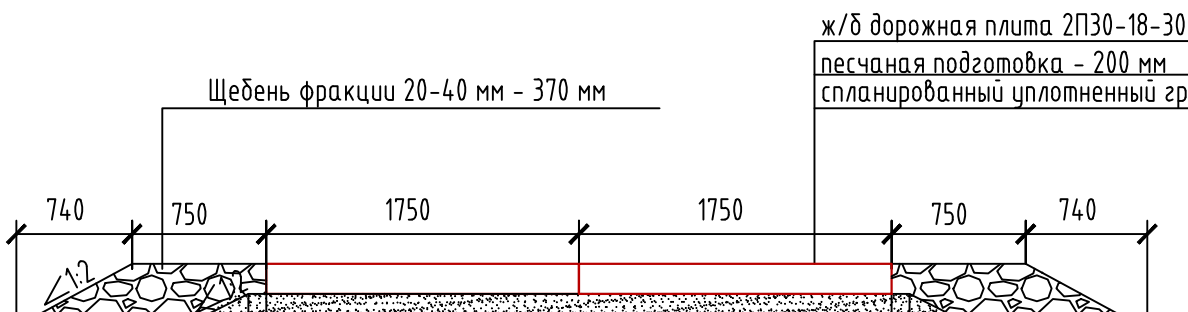

б) пешеходные дорожки и площадки



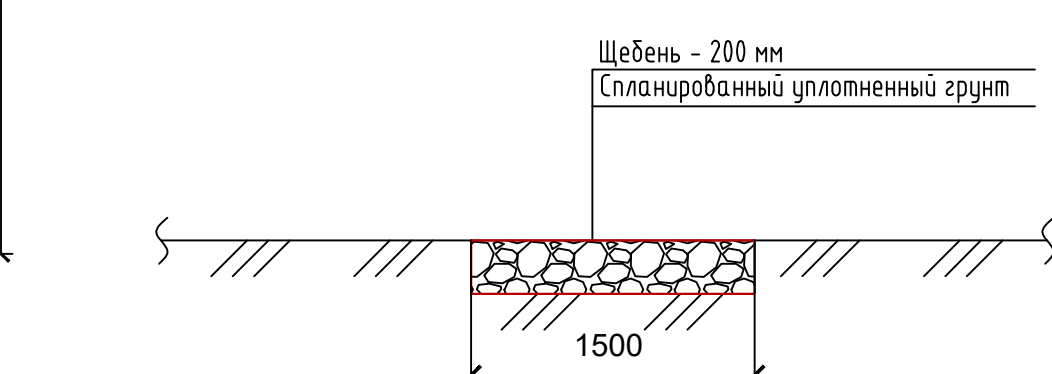



СХЕМА УСТРОЙСТВА ПЛОЩАДКИ ДЛЯ МОЙКИ КОЛЕС АВТОМАШИН

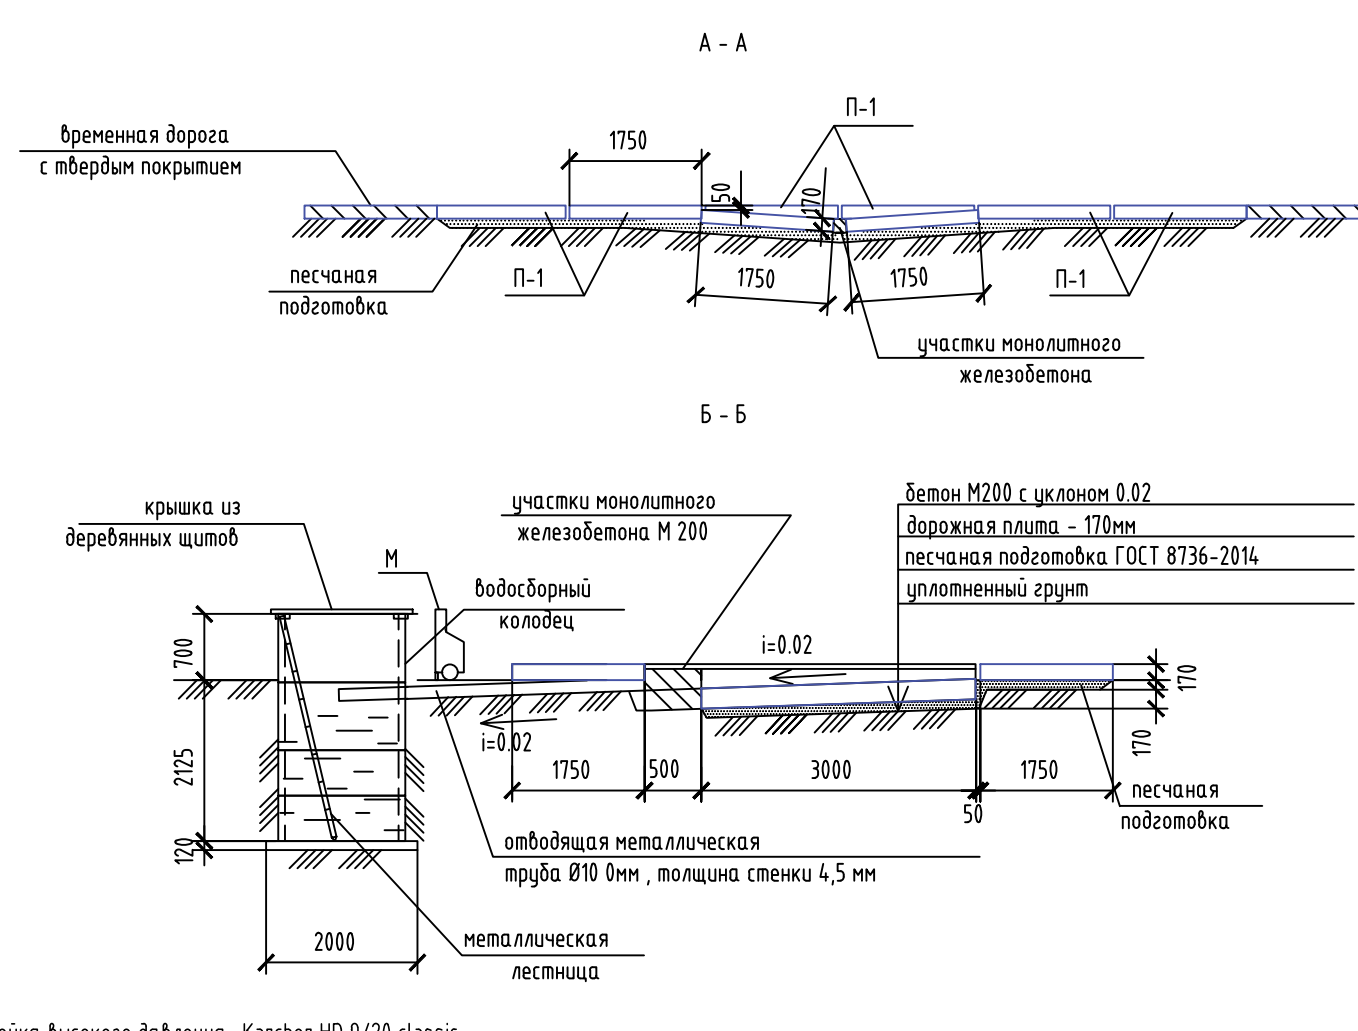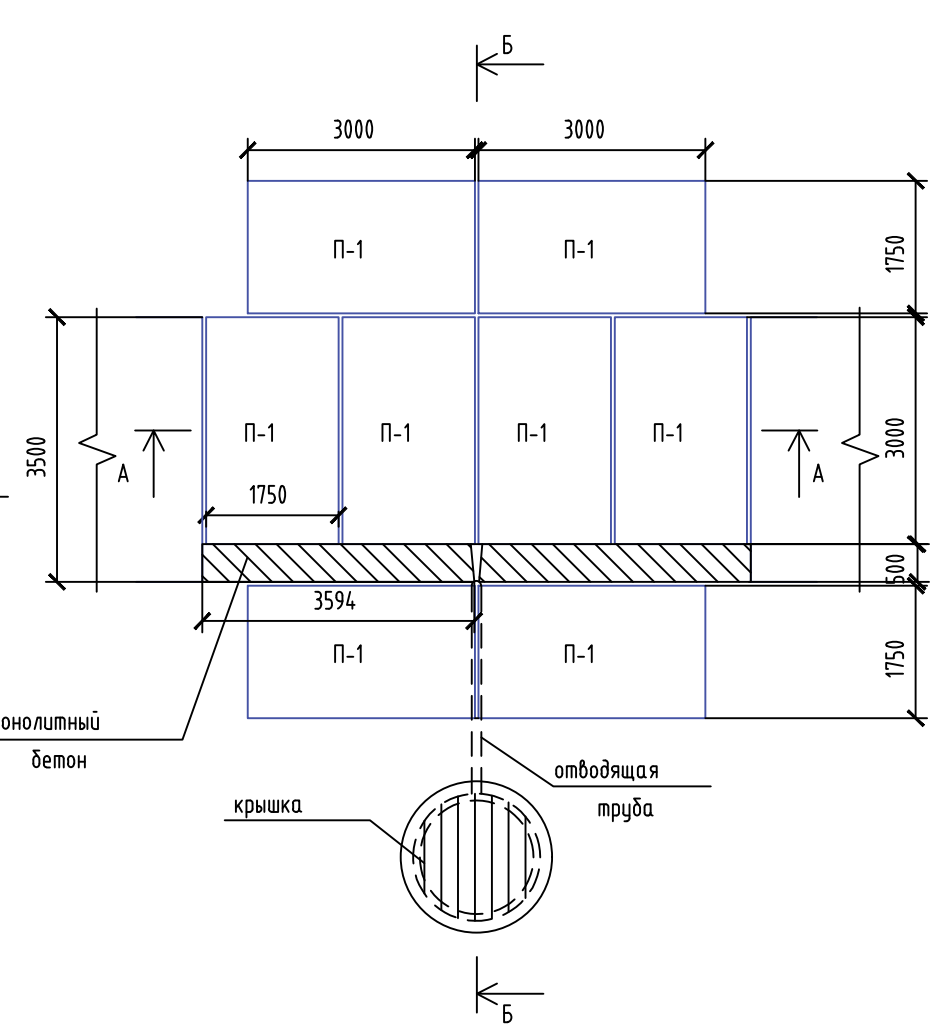


Строительный генеральный план

На период строительства надземной части здания

М 1:350

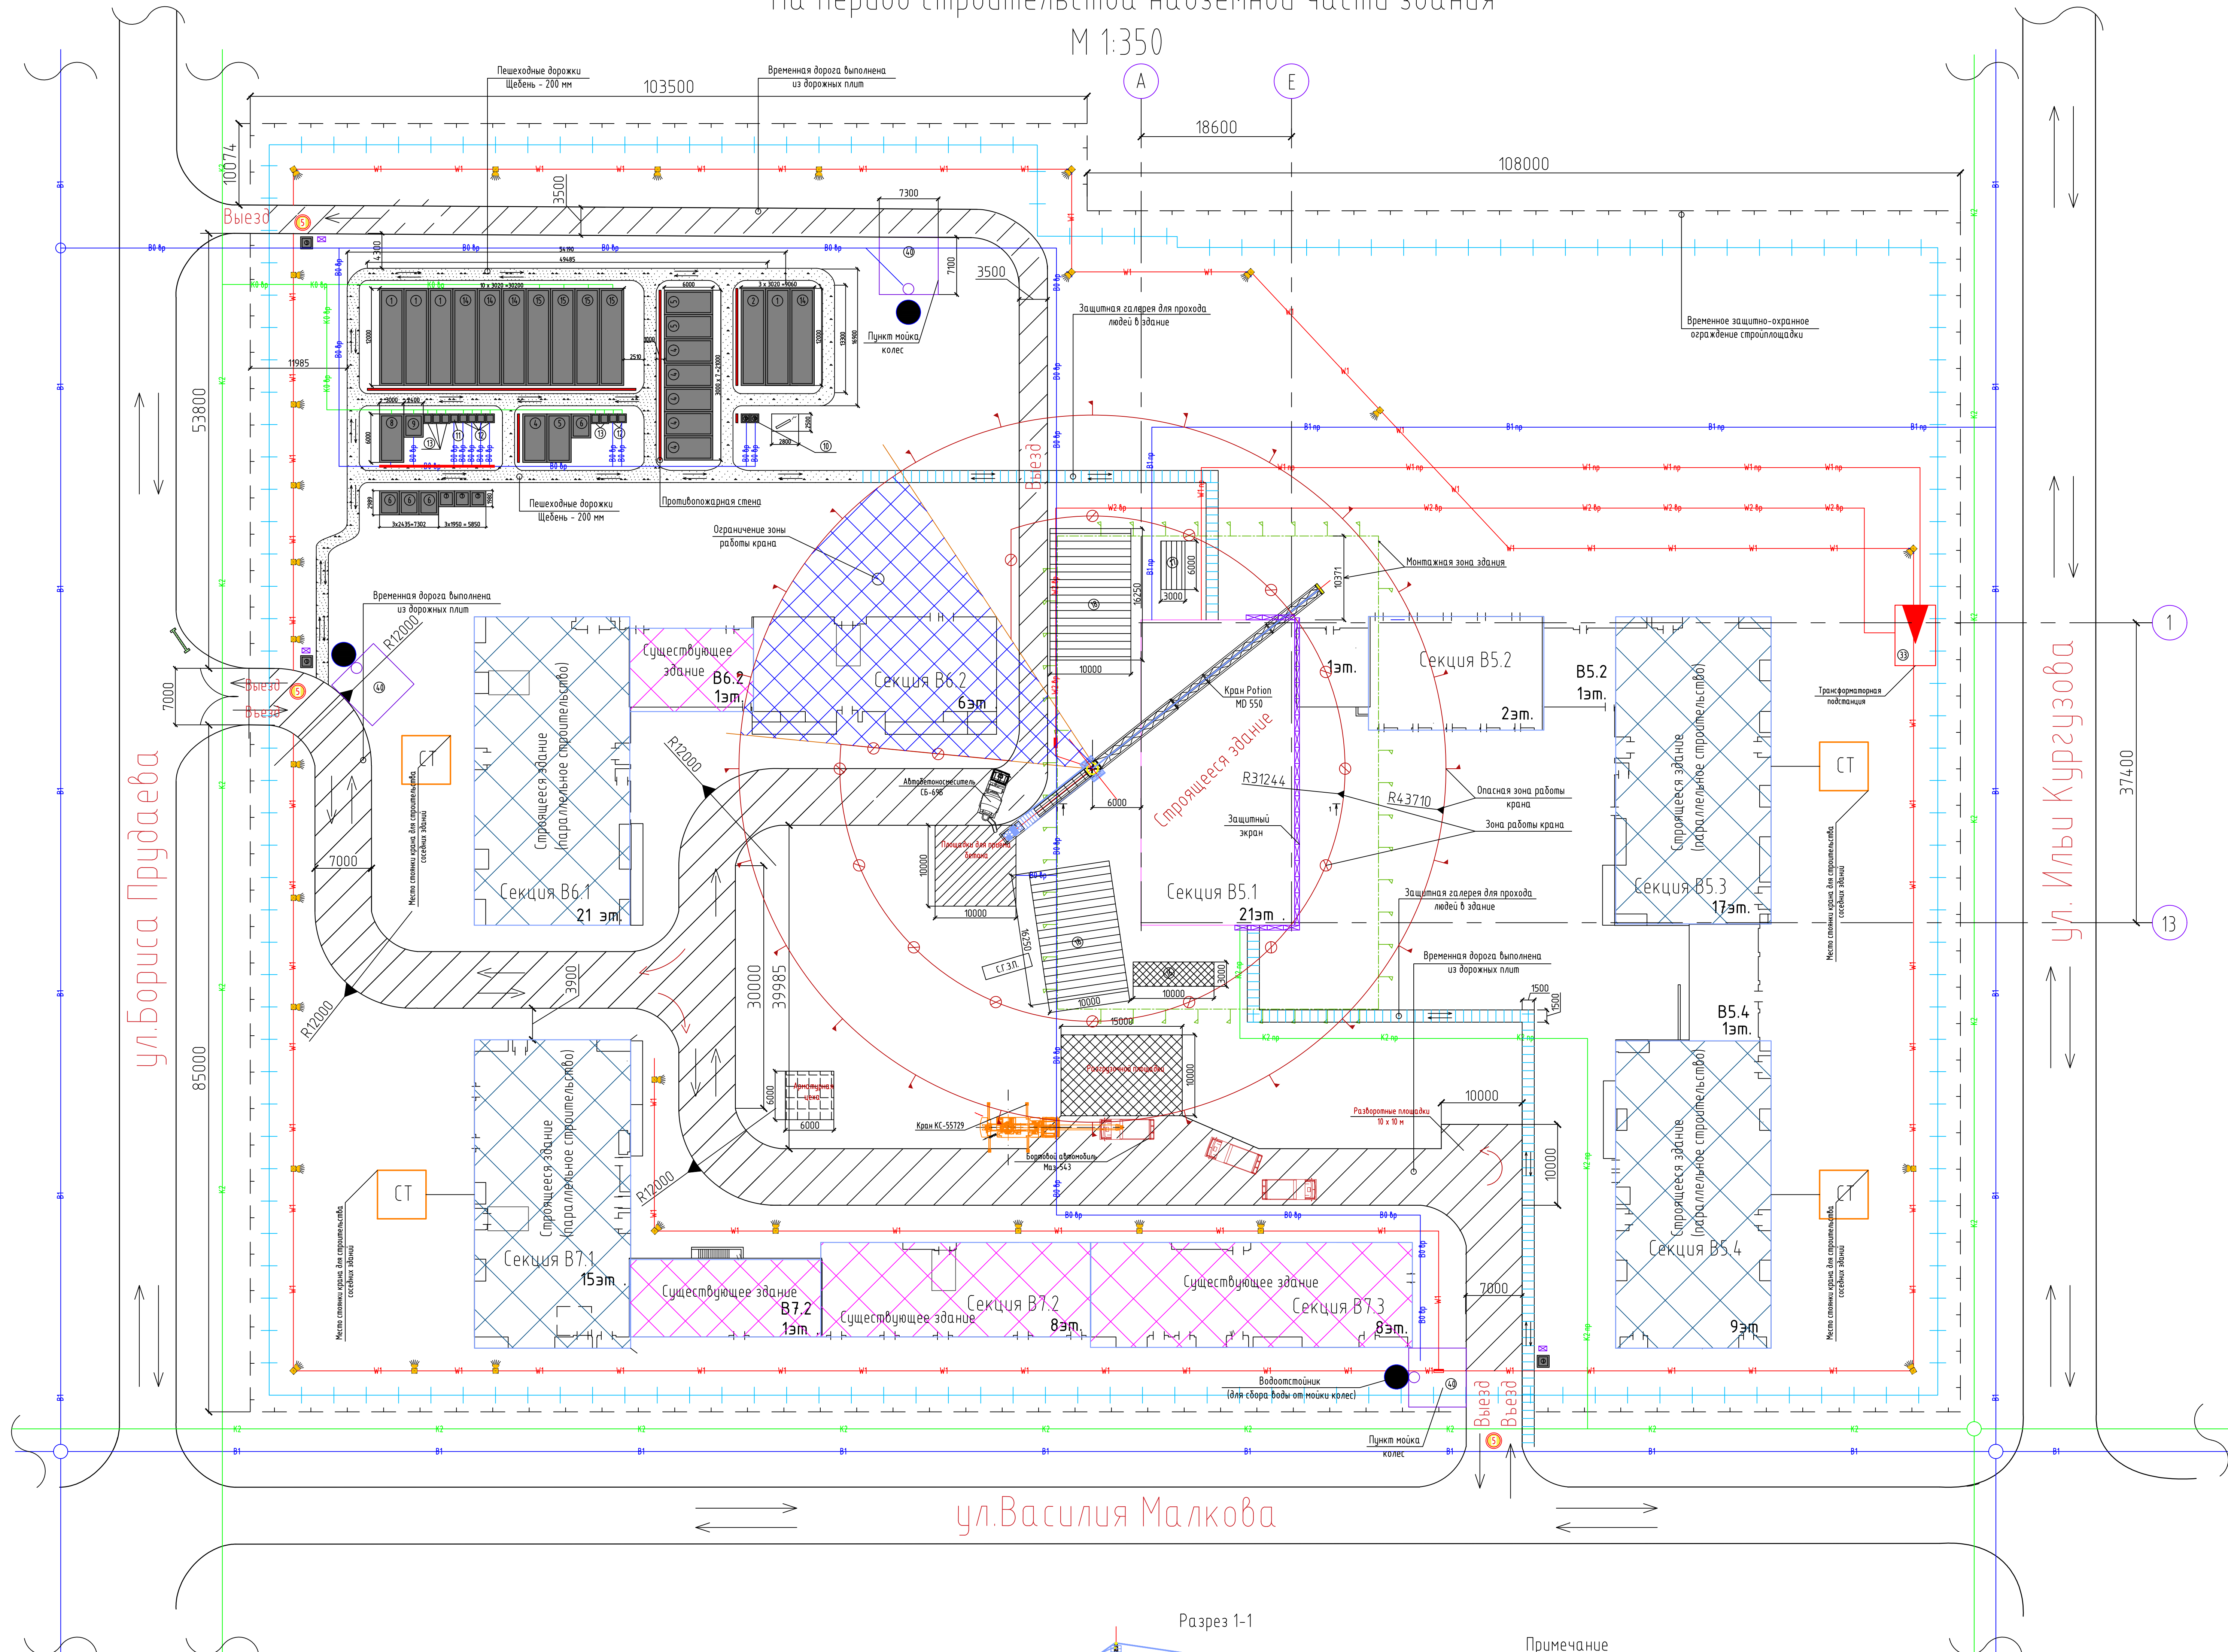

Разрез 1-1

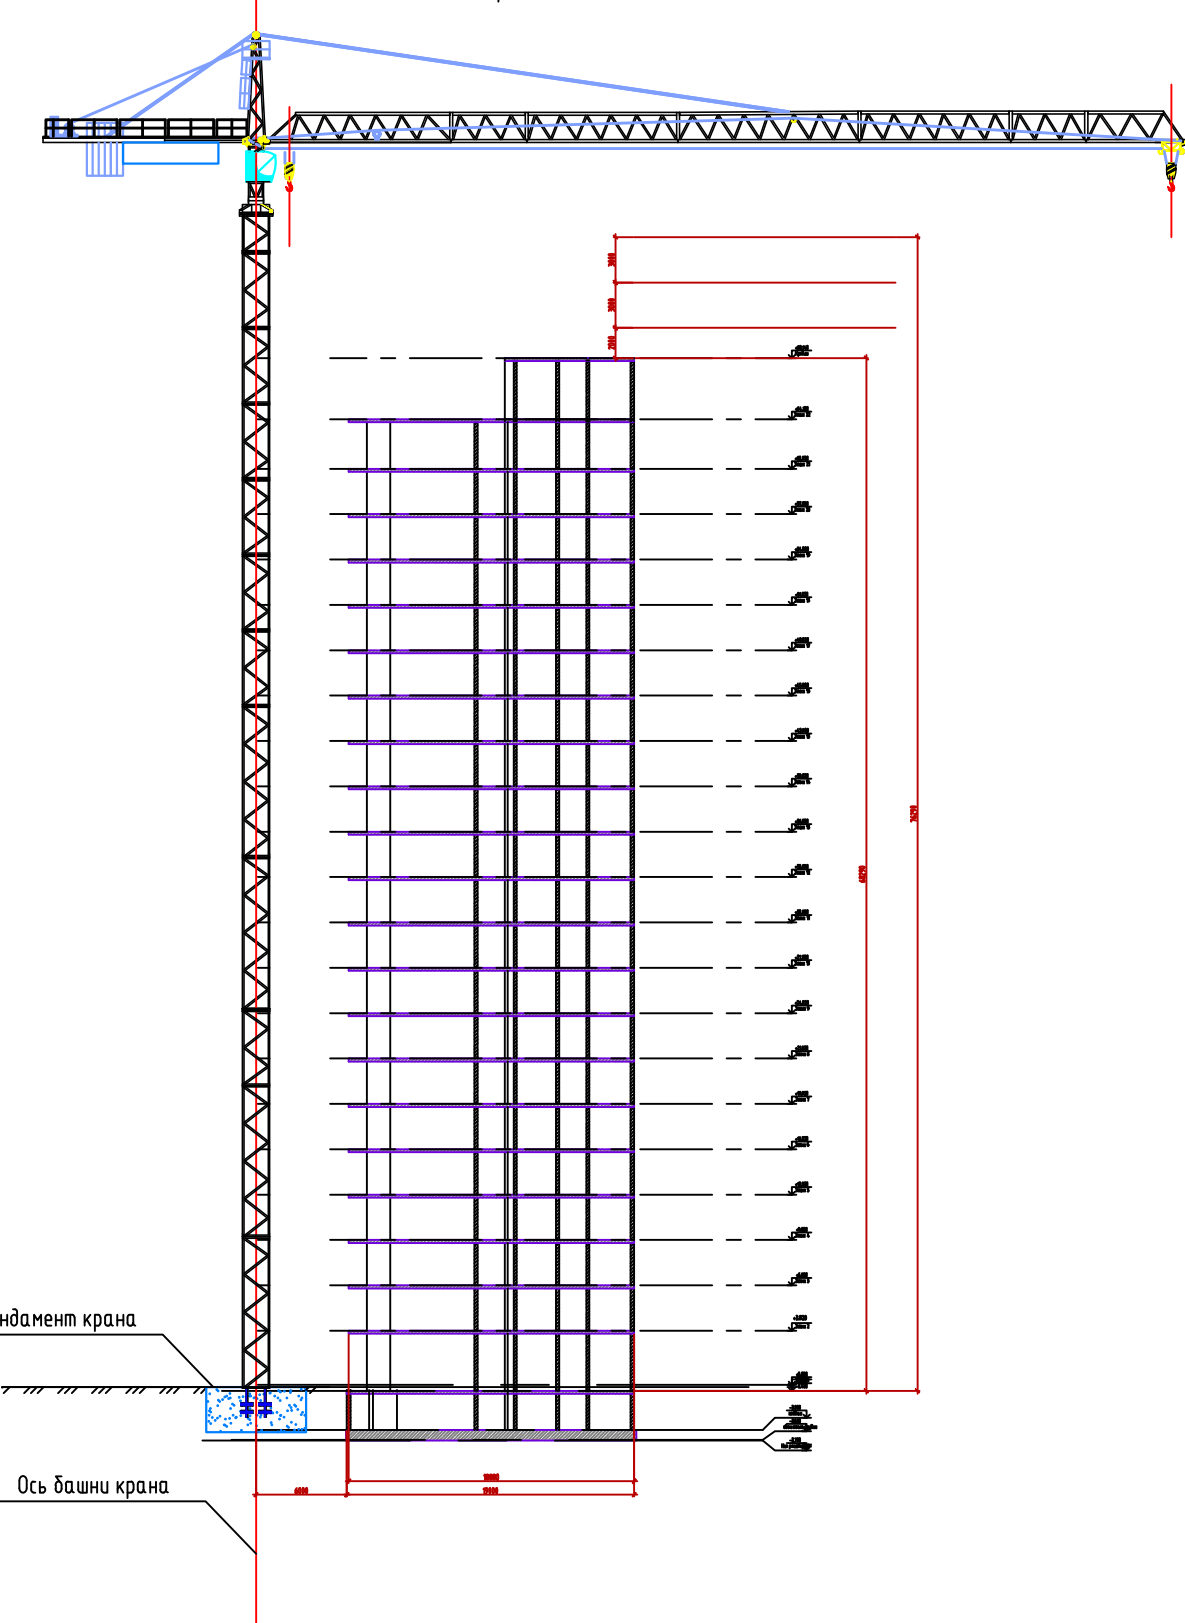

Примечание

- 1- Данный проект разработан для строительства надземных частей здания.
- 2- До начала строительства жилого дома должны быть выполнены подготовительные работы, в т.ч. установлено ограждение из металлического профлиста.
- 3- Электрооснащение строительной площадки. Выполнить подключение к существующим электрокоммуникациям. На площадке установить трансформаторную подстанцию КТП-560 с номинальной мощностью 560 кВт.
- 4- Складские площадки устраиваются из слоя щебня толщиной 100 мм. Площадку складирования обеспечить уклоном 3°.
- 5- У въездов на строительную площадку вывесить планы пожарной защиты с местонахождением водоотстойника, средств пожаротушения. Каждый дымовой датчик обеспечить огнетушителем.
- 6- Подвешивать краном груз на монтажном горизонте перемещать к месту установки с минимальной скоростью.
- 7- При въезде автотранспорта со строительной площадки необходимо мыть колеса. Для мойки устроить площадку.
- 8- Выполнить освещение каркаса здания и крана в ночное время.
- 9- Освещение территории производить при помощи светильников ПЭС-35.
- 10- Данный проект разработан для строительства подземных частей здания.
- 11- Обеспечить круглосуточную охрану строительной площадки.
- 12- Отходы и строительный мусор своевременно вывозить на свалку.
- 13- Монтажную зону и опасную зону работы крана на местности обозначить хорошо видимыми знаками и указателями.
- 14- Скорость движения автотранспорта на площадке не должна превышать 10 км/ч на прямых участках и 5 км/ч на разворотах.
- 15- Условные обозначения приняты по прил. И СТО НОСТРОЙ 2.33.51-2011 "Организация строительного производства. Подготовка и производство строительных и монтажных работ".

Д И С А 08.03.014.20004. ПОС.З.2026				
ПОС - Разработка строительных генеральных планов на возведение 21-этажного жилого дома				
Имя	Имя	Лист	Имя	Дата
Создатель	Создатель	Лист	Создатель	Дата
Проверенный	Проверенный	Лист	Проверенный	Дата
Утвержденный	Утвержденный	Лист	Утвержденный	Дата
Создатель	Создатель	Лист	Создатель	Дата
Проверенный	Проверенный	Лист	Проверенный	Дата
Утвержденный	Утвержденный	Лист	Утвержденный	Дата
Создатель	Создатель	Лист	Создатель	Дата
Проверенный	Проверенный	Лист	Проверенный	Дата
Утвержденный	Утвержденный	Лист	Утвержденный	Дата

21-этажный жилой дом (секция Б5.1) по ул. Василия Малкова в г. Тюмень			Состав	Лист	Листов
Строительный генеральный план			4	2	2
на период строительства надземной части здания			Упр.У кафедр ПГС и ЭИ		