


Инв. № подл.	Подпись и дата	Взам. инв. №

Инв. № подл.	Подпись и дата
--------------	----------------

Инв. № подл.	
--------------	--

- | | |
|--------------|--|
| Инв. № подл. | |
|--------------|--|

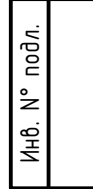


Инв. № подл.	
--------------	--

	Ярус 21	
	Ярус 20	
	Ярус 19	
	Ярус 18	
	Ярус 17	
	Ярус 16	
	Ярус 15	
	Ярус 14	
	Ярус 13	
	Ярус 12	
	Ярус 11	
	Ярус 10	
	Ярус 9	
	Ярус 8	
	Ярус 7	
	Ярус 6	
	Ярус 5	
	Ярус 4	
	Ярус 3	
	Ярус 2	
	Ярус 1	

[illegible]

№	Наименование	Единицы измерения	Показатели	Примечания
1	Общая продолжительность	дн	480	см. КП)
2	Общие трудовозатраты	челХСм	30310,22	см. КП)
3	Общие Машинемкости	машХСм	1215,58	см. КП)
4	Нормативная продолжительность строительства	мес	16	см. ПЗ)
5	Фактическая продолжительность строительства	мес	16	см. КП)
6	Мак количество рабочих Nmax	чел	126	см. КП)
7	Мин количество рабочих Nmin	чел	4	см. КП)
8	среднее число рабочих	чел./дн	63	$N_{ср} = T / П_{пр}$
9	Коэффициент неравномерности движения рабочих	-	2,00	$K_{дв} = N_{max} / N_{ср}$
10	Коэффициент механизации строительства	-	0,038	$K_{мех} = M / (M + T)$
11	Коэффициент совмещения	-	2,183	$K_{сов} = P / П_{пр}$

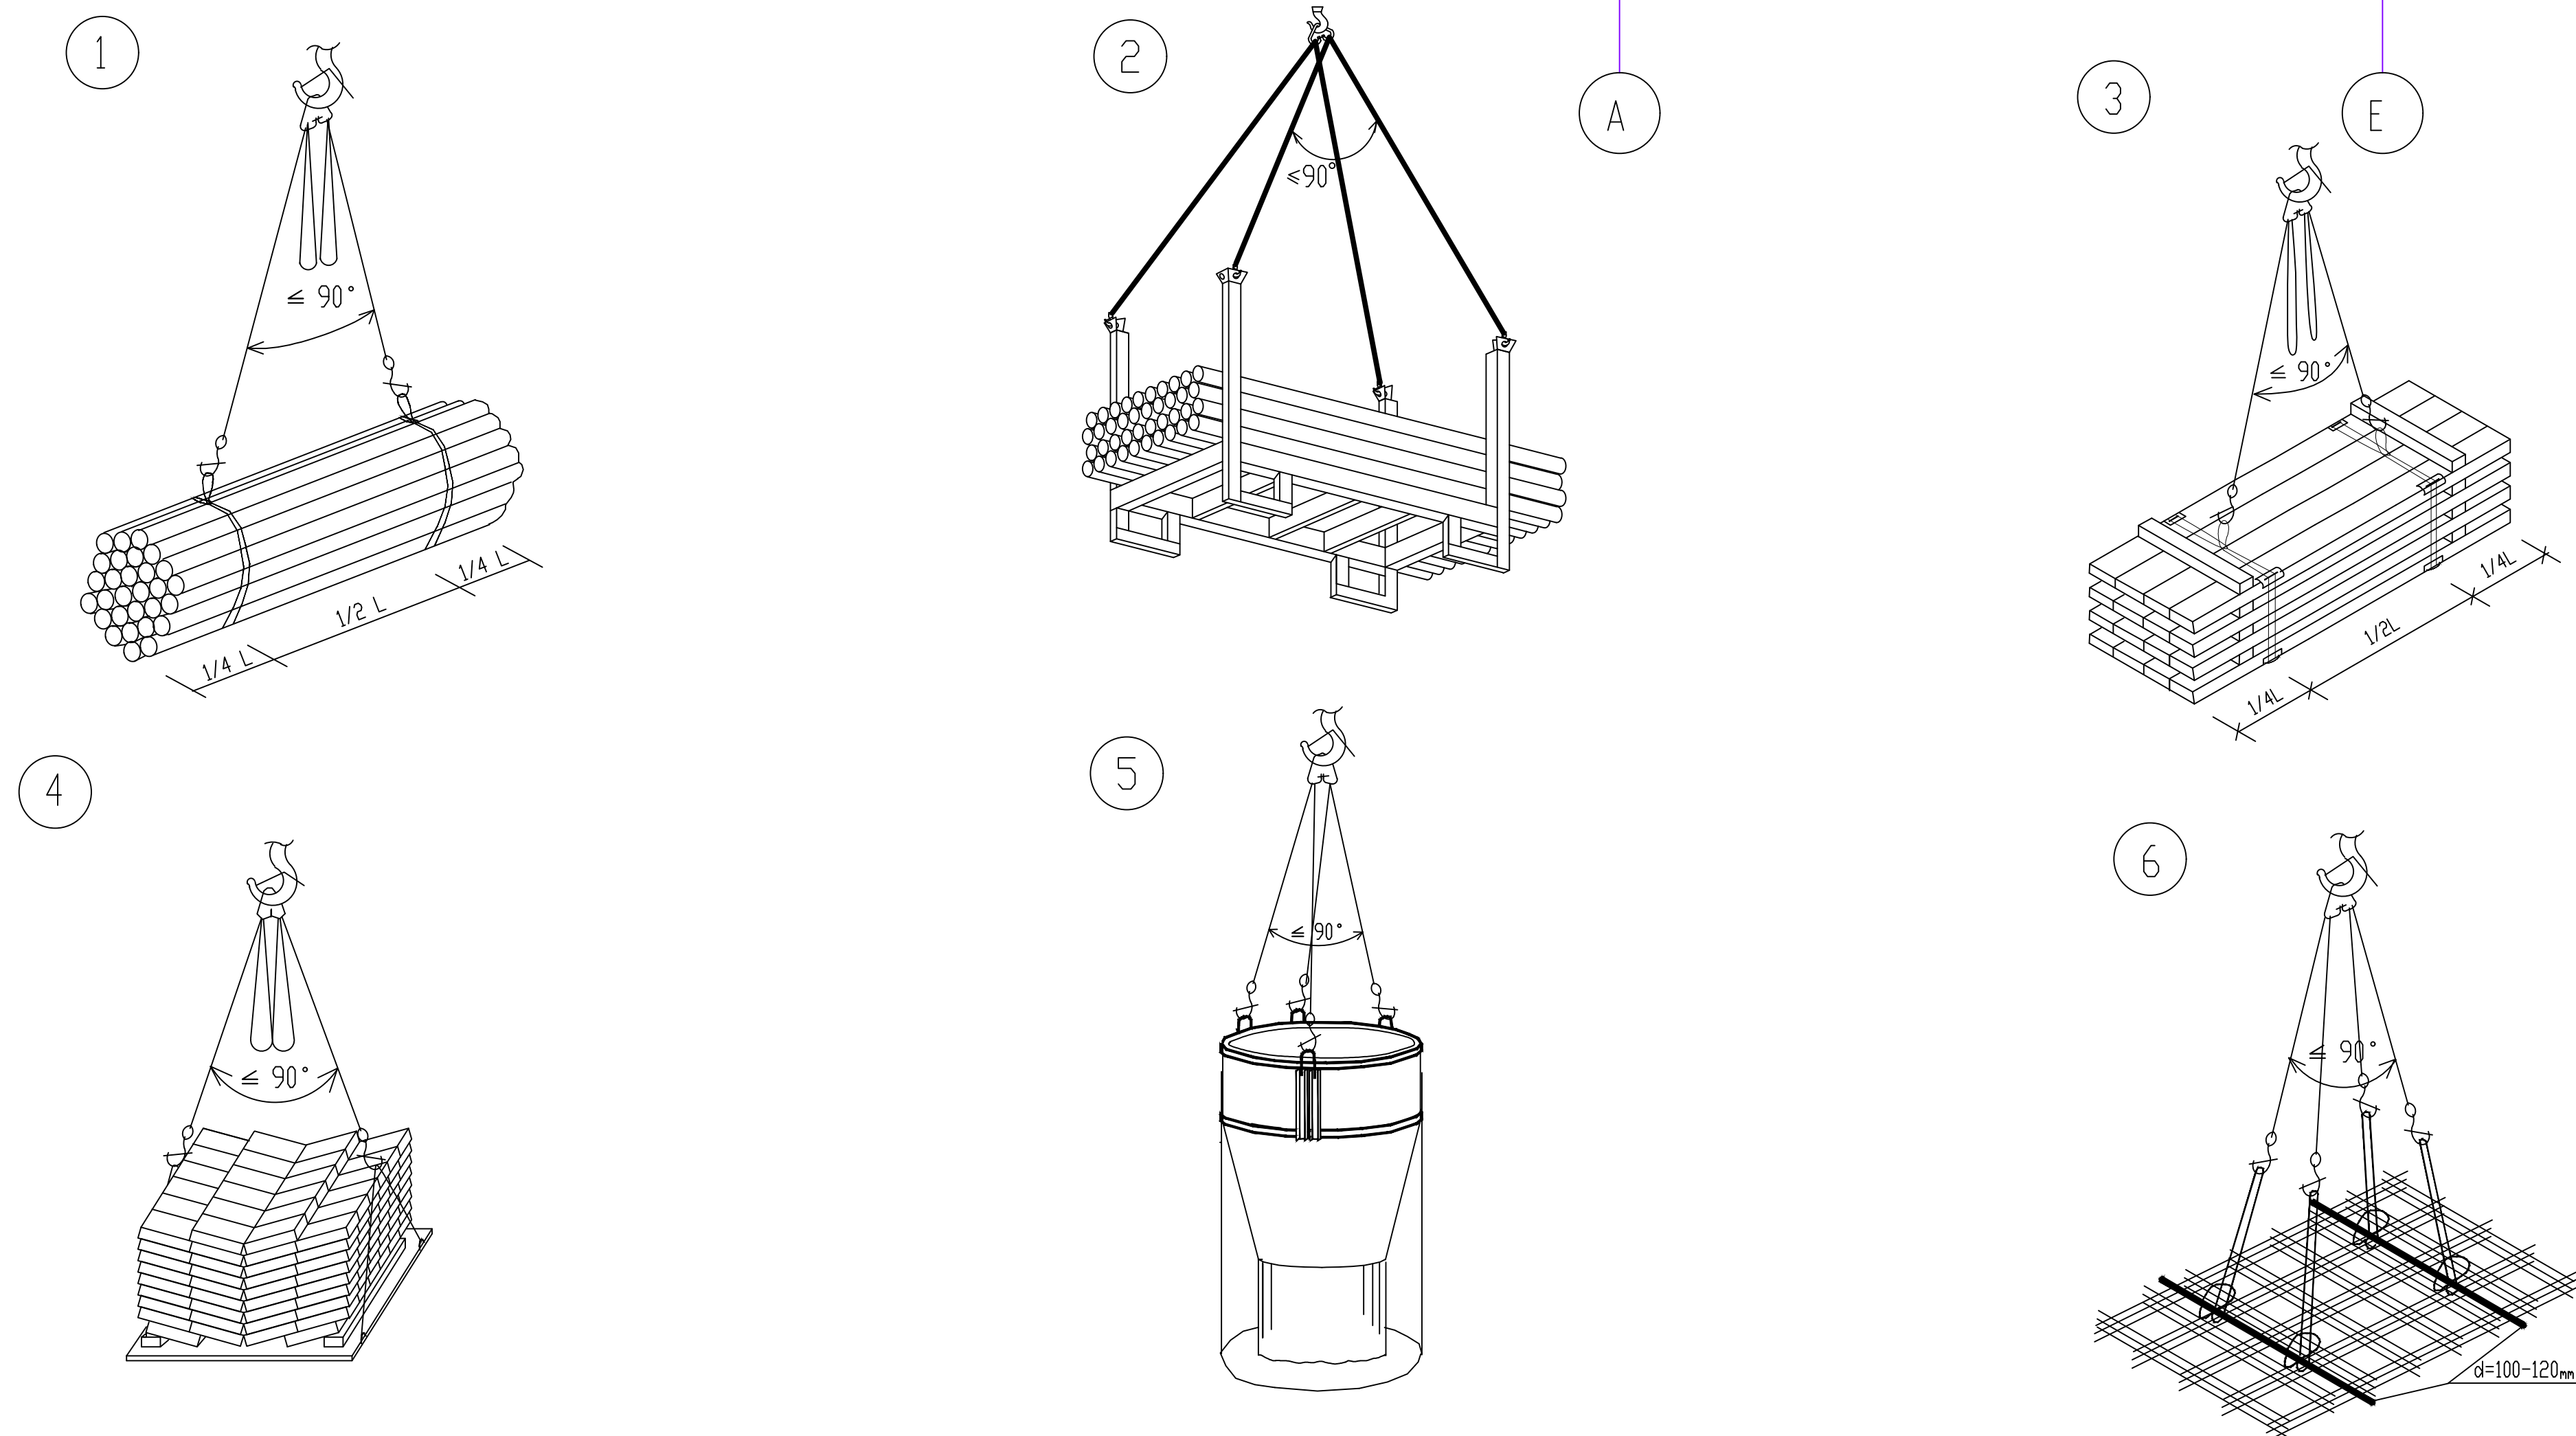

1	—	Схемы стропобки арматурные стержни
2	—	Контейнер с телескопическими стойками
3	—	Контейнер с телескопическими стойками
4	—	Поддон с кирпичом (при разгрузке)
5	—	Бафья с детонной смесью
6	—	Схемы стропобки арматурные сетки

Д.ИСА.08.03.01420004.ПОС.3.2025 Пас - Разработка календарного плана строительства 21-этажного жилого дома						Стация Лист Листов		
21-этажный жилой дом (секция Б5.1) по ул. Василия Малякова д.3. Тюмень						2	2	2
Календарный план строительства						Урфу кафедрПГС и ЭН		
Изм.	Кол-во	Лист	№ док.	Подпись	Дата			
Ступеней		Барды Х.Х.		<i>Хусеин</i>	11.25.25			
Консультаций		Бессоновой О.А.			11.25.25			
Консультаций		Бессоновой О.А.			11.25.25			
Продумывания		Бессоновой О.А.			11.25.25			
Итого					11.25.25			
Зав. кафе		Фомин Н.И.			11.25.25			