

2-2








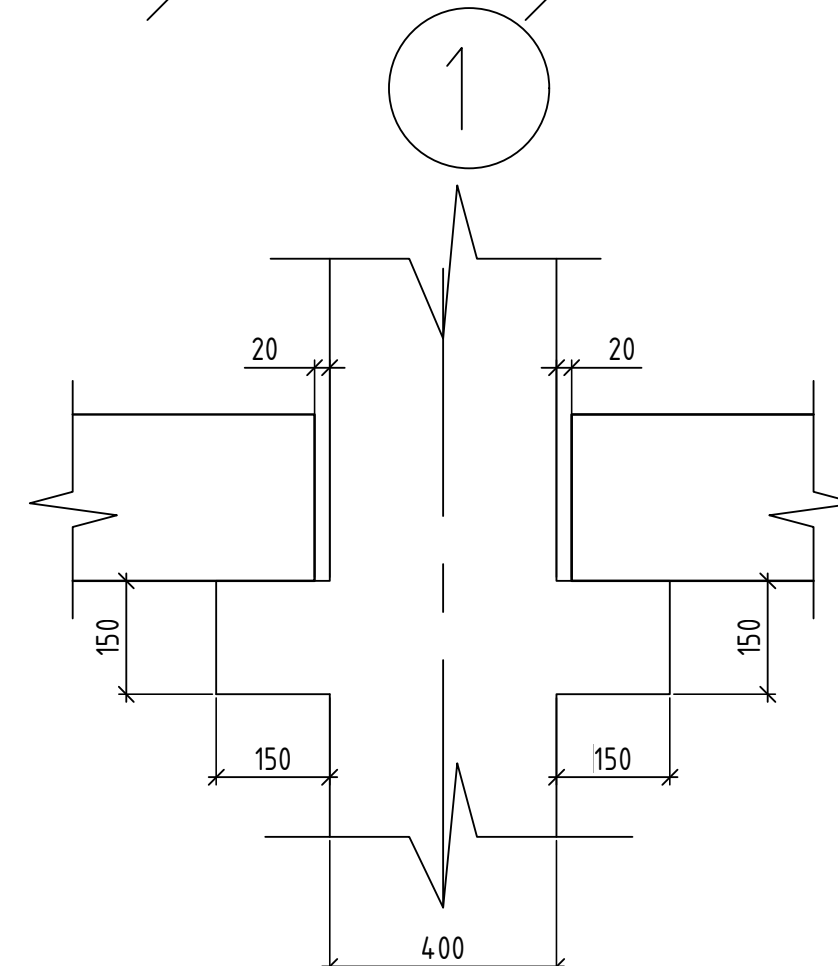
[illegible]

Схема плиты П1, разрез 1-1, разрез 2-2, разрез 3-3

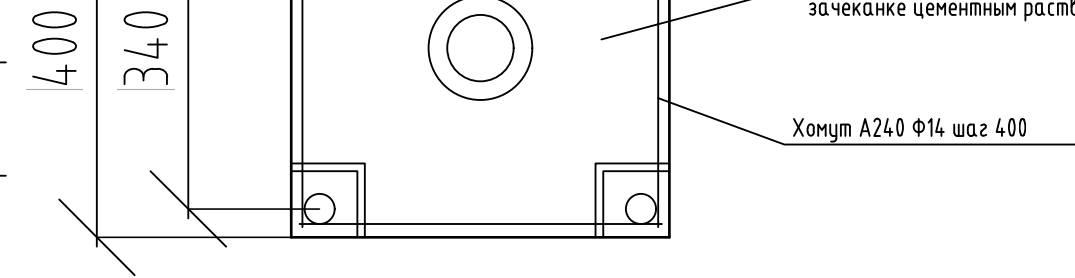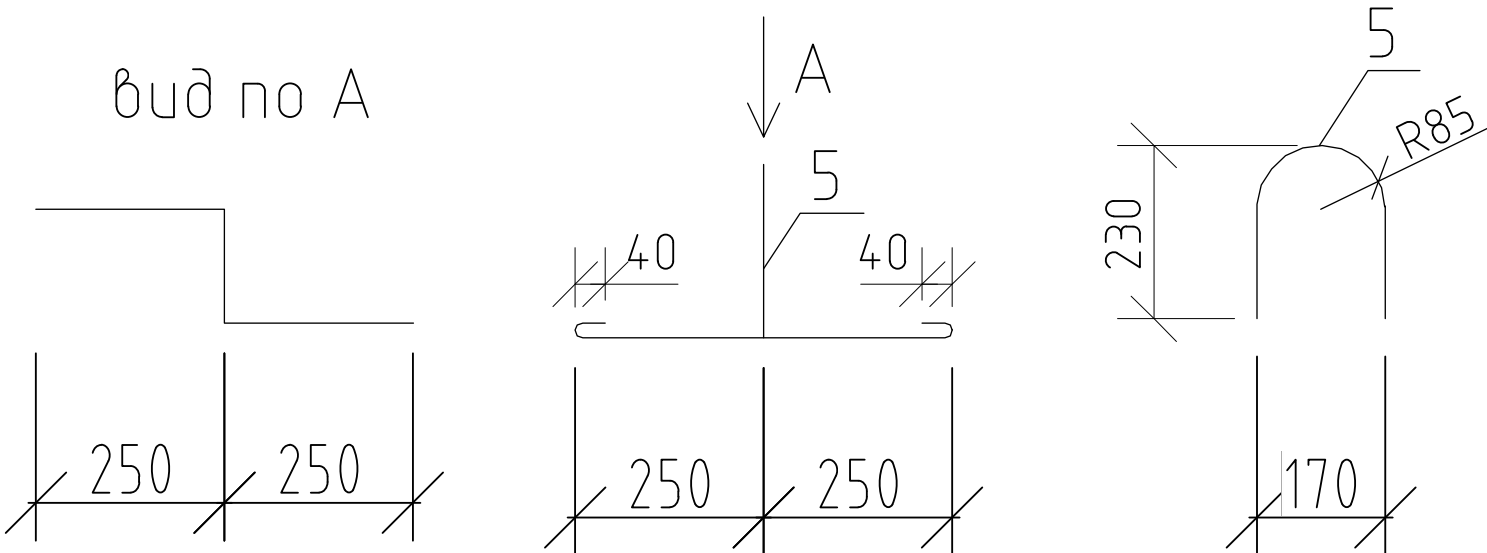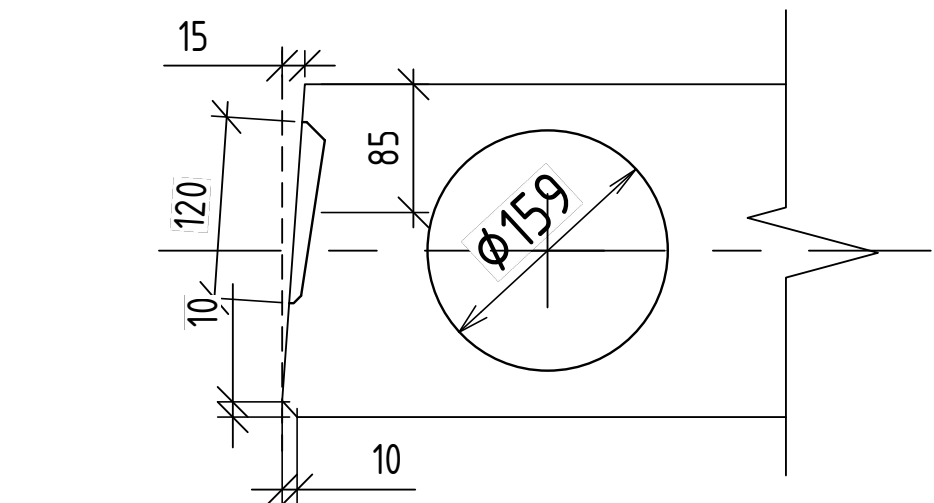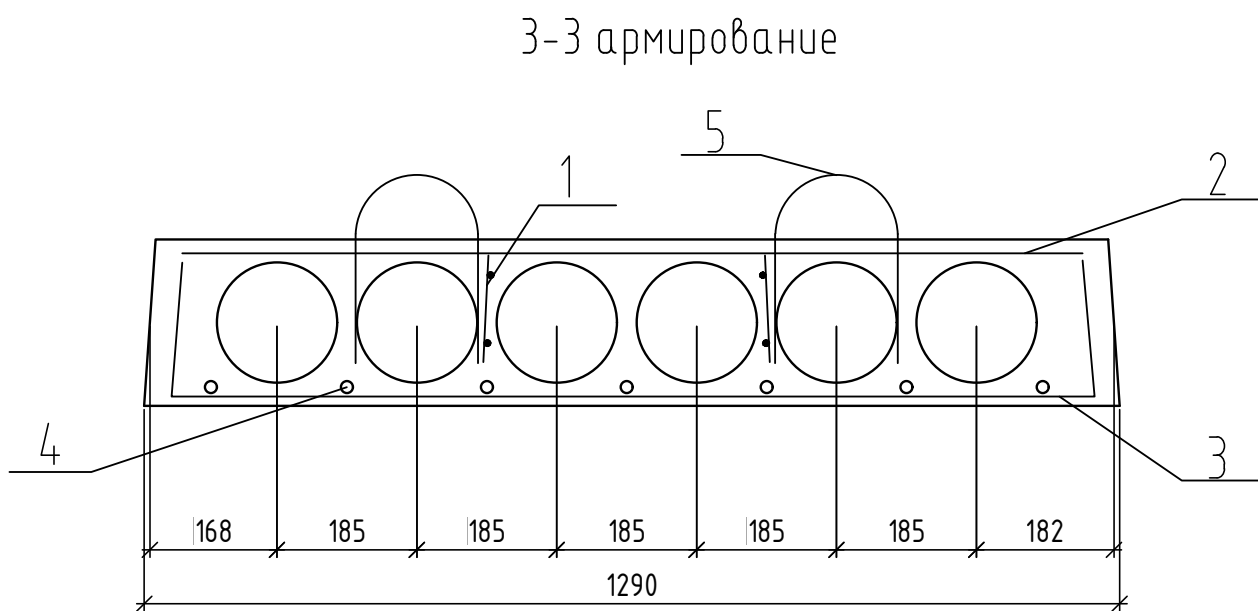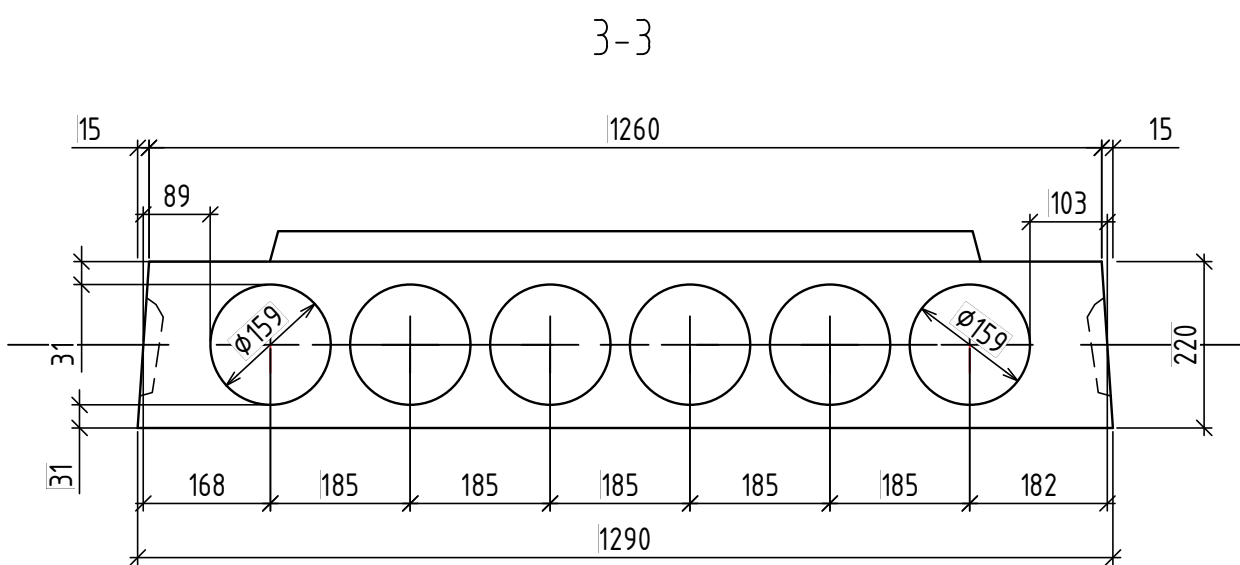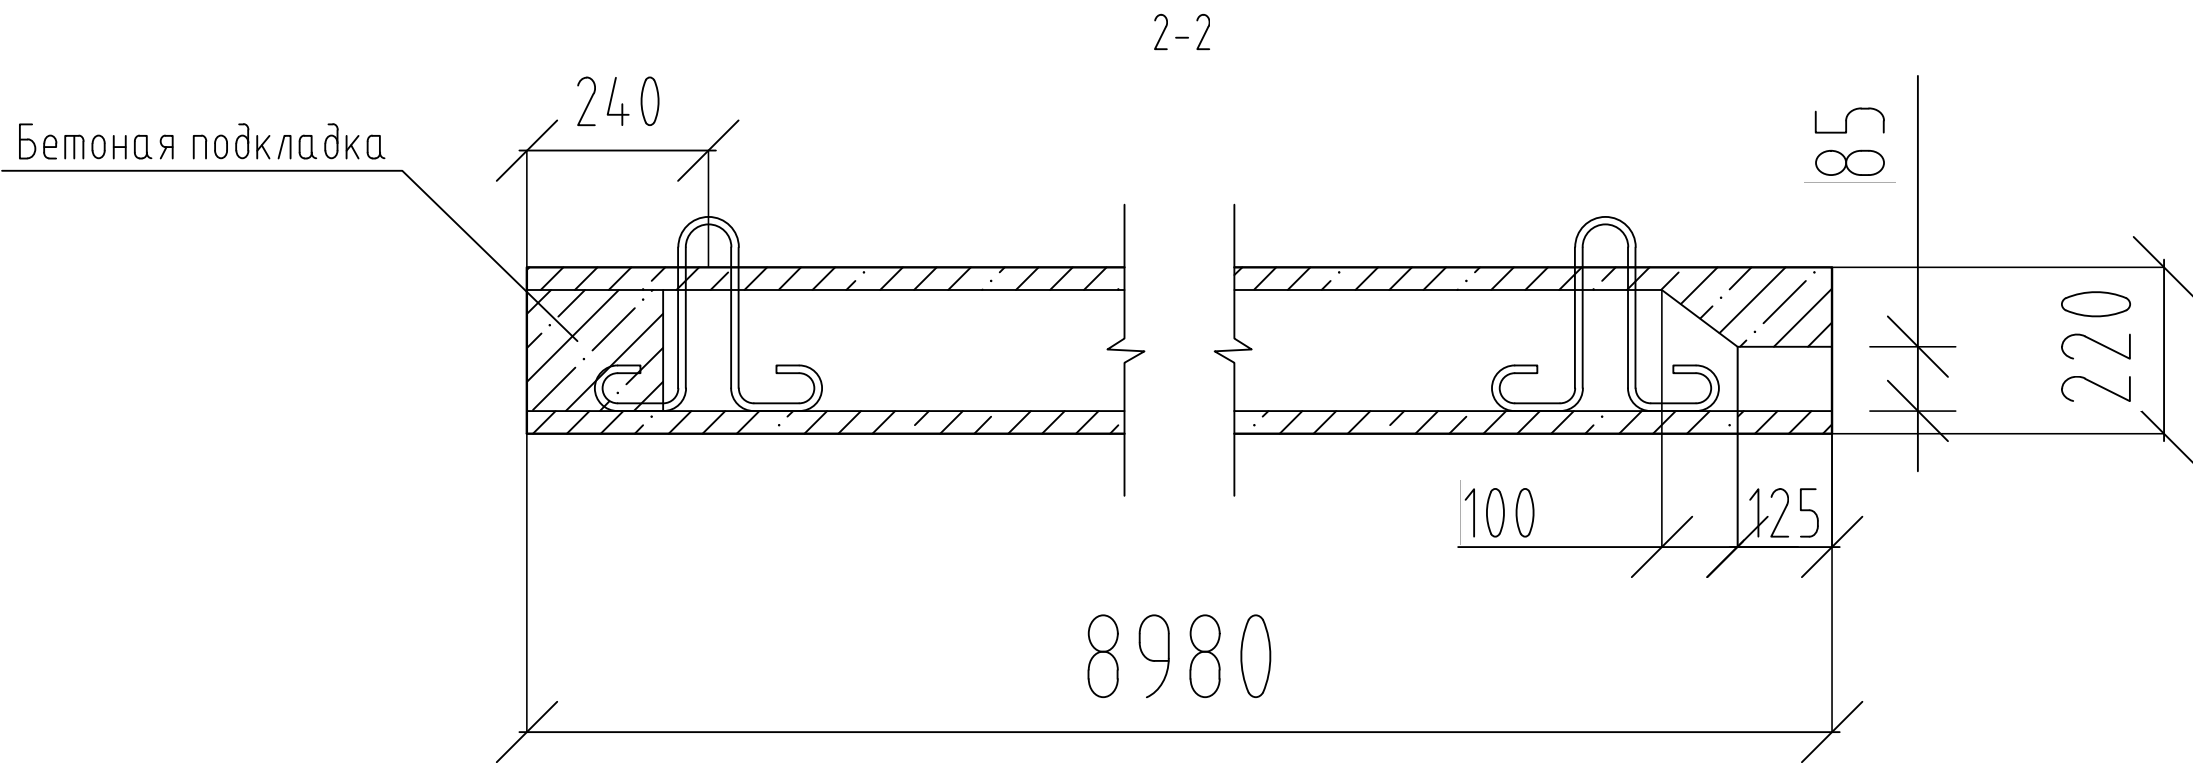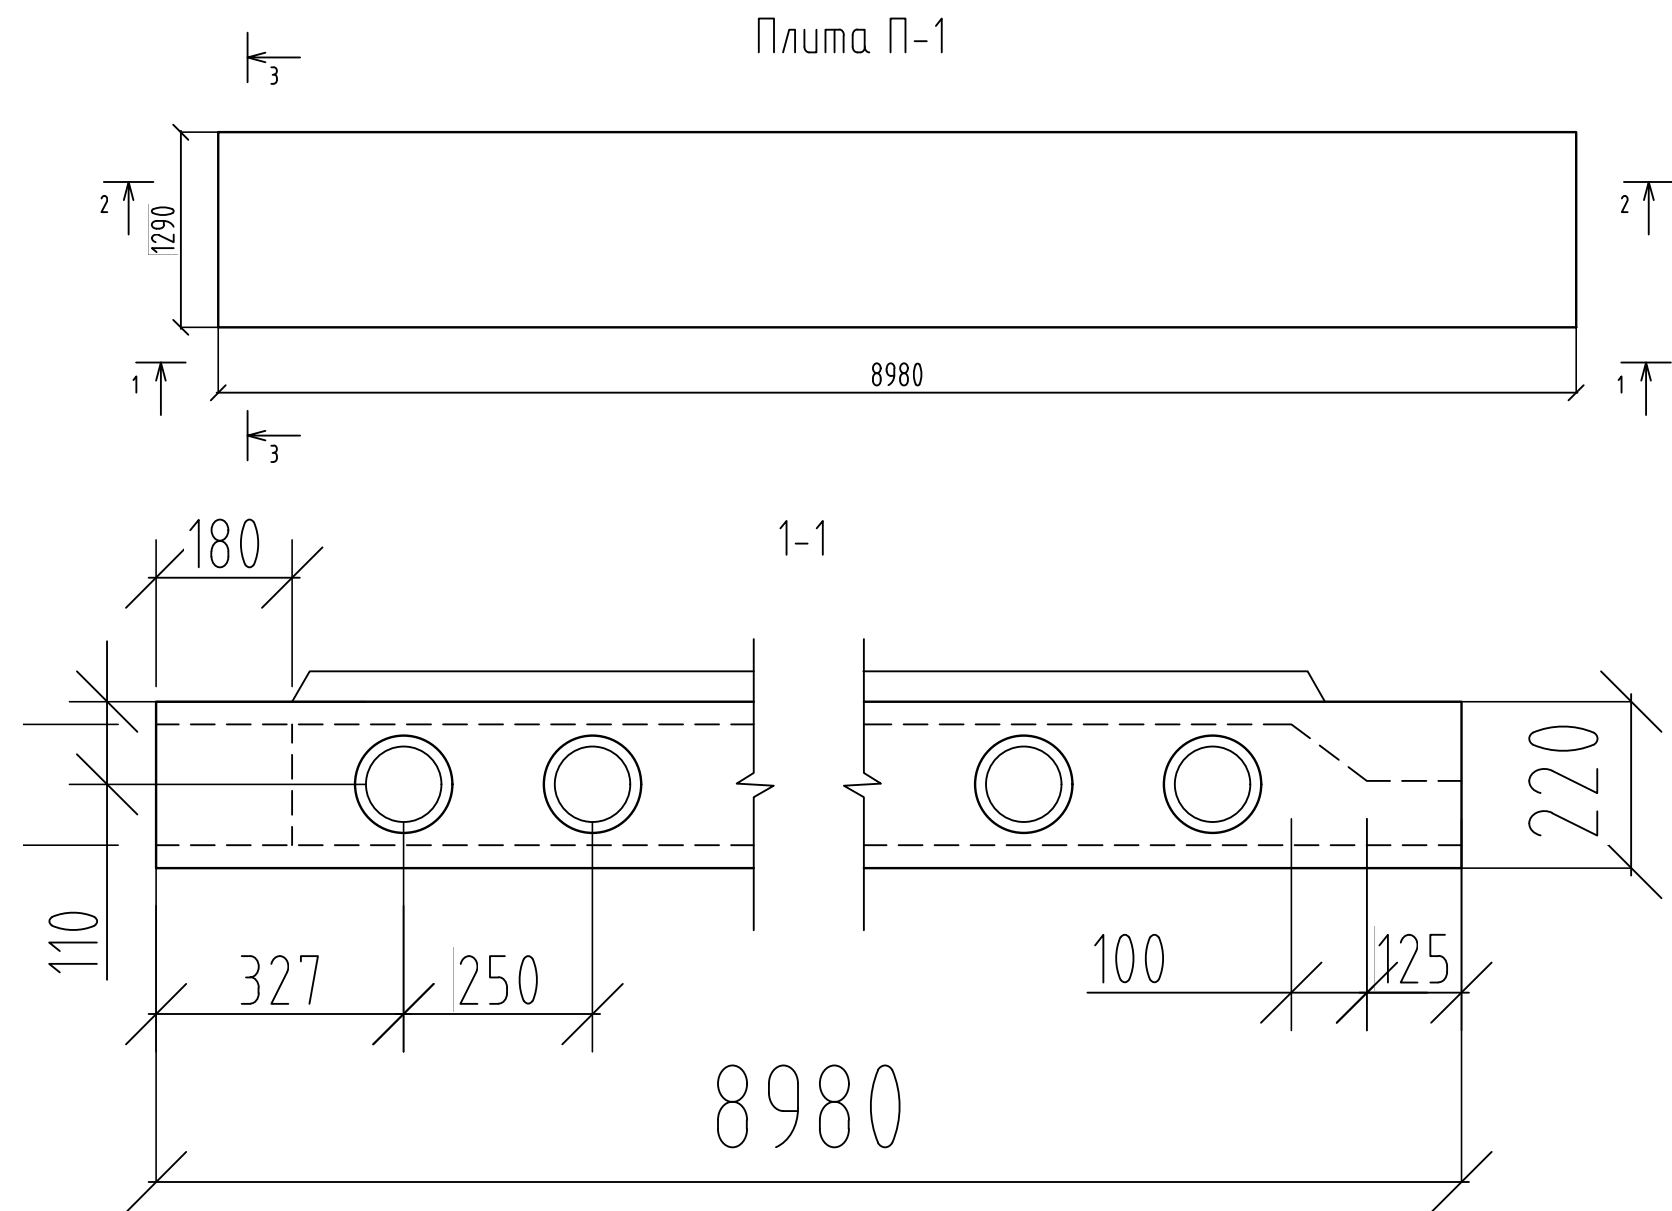


Спецификация элементов

Марка	Обозначение	Наименование	Кол.	Масса ед., кг	Примечание
П-1		Плита П-1			
		Сборные единицы			
1		Каркас плоский КР-1			
2		Сетка С-1			
3		Сетка С-2			
		Детали			
4		Стержни Ф 14 А800			
5		Стержни Ф 10 А240	4		
		Материалы			
6		Бетон В25			
Д.ИСА.08.03.01.06201102.КП.25-КЖ					
Многоэтажное промышленное здание с железобетонным каркасом					
Изм.	Кол. изм.	Лист	№ док.	Подпись	Дата
Студент		Бадри Х.Х.	23.06		
Консультант		Редикунцев	23.06		
Консультант		Редикунцев	23.06		
Руководитель		Редикунцев	23.06		
Н.контр.		Уфимцева	23.06		
Зав. каф		Беляева	23.06		
Сборное железобетонное перекрытие				Стадия	Лист
				У	2
Схема плиты П1, разрез 1-1, разрез 2-2, разрез 3-3				УрФУ кафедра СКМГ	

Инф. № подл.	Подпись и дата	Взам. инф. №

Колонна К-1

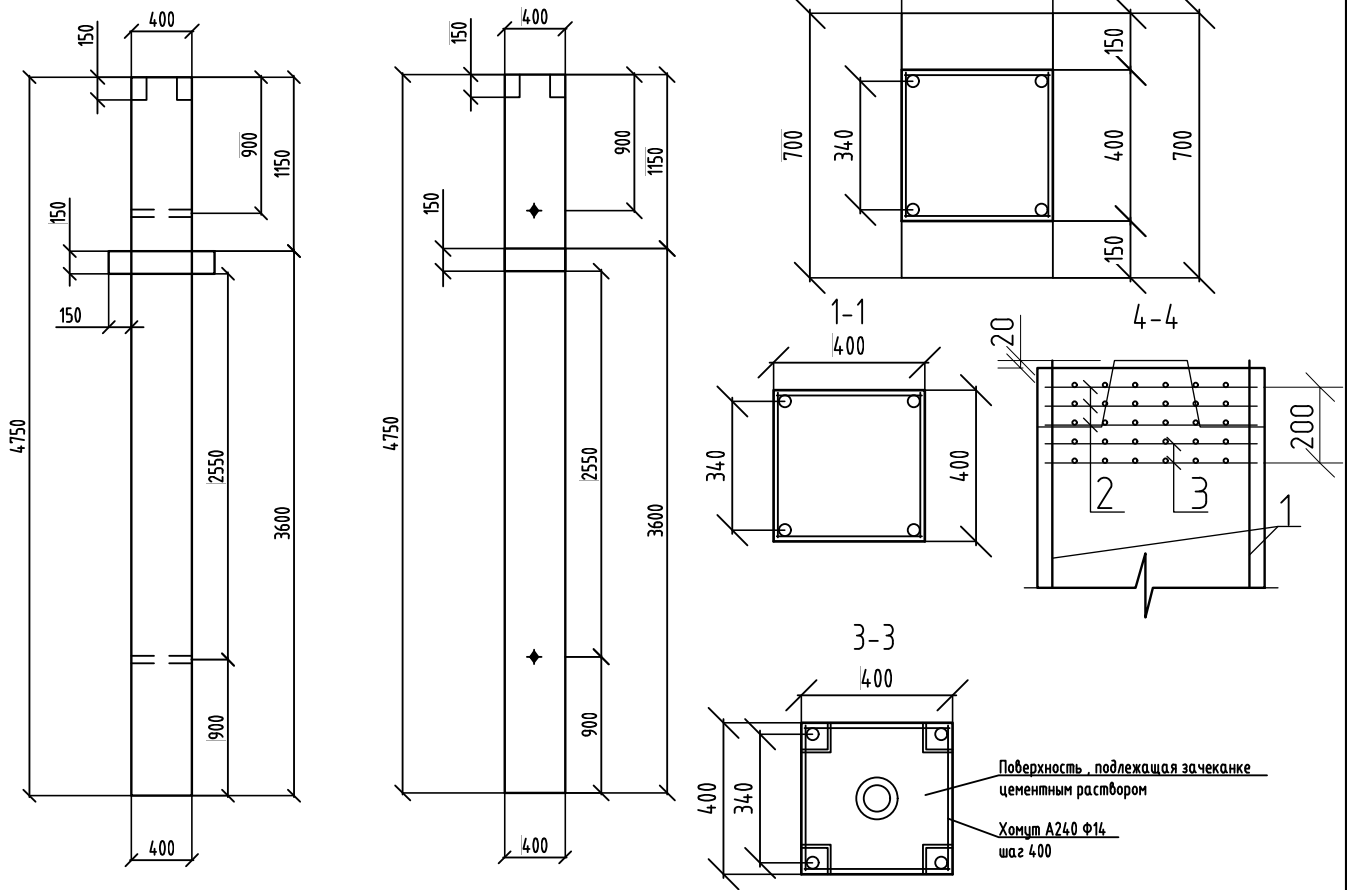


Спецификация элементов

Марка	Обозначение	Наименование	Кол.	Масса ед., кг	Примечание
К-1		Колонна К-1			
		Сборные единицы			
КП-1		Каркас пространственный КП1			
С-3		Сетка С3			
С-4		Сетка С4			
МН-1		Изделия закладные МН1			
		Материал			
		Бетон В25			

Взам. инв. №		С-4					Сетка С4						
		МН-1					Изделия закладные МН1						
							Материал						
							Бетон В25						
Подпись и дата							Д.ИСА.08.03.01.06201102.КП.25-КЖ						
							Многоэтажное промышленное здание с железобетонным каркасом						
		Изм.	Кол. уч.	Лист	№ док.	Подпись	Дата						
		Студент		Бадри Х.Х.			23.06	Сборное железобетонное колонн			Стадия	Лист	Листов
Консультант		Редикольцев			23.06	У	3				6		
Инв. № подл.		Консультант		Редикольцев		23.06	Колонна К-1			УрФУ кафедра СКУМГ			
		Консультант		Редикольцев		23.06							
		Руководитель		Редикольцев		23.06							
		Н.контр.		Уфимцева		23.06							
		Зав. каф		Беляева		23.06							

КП-1

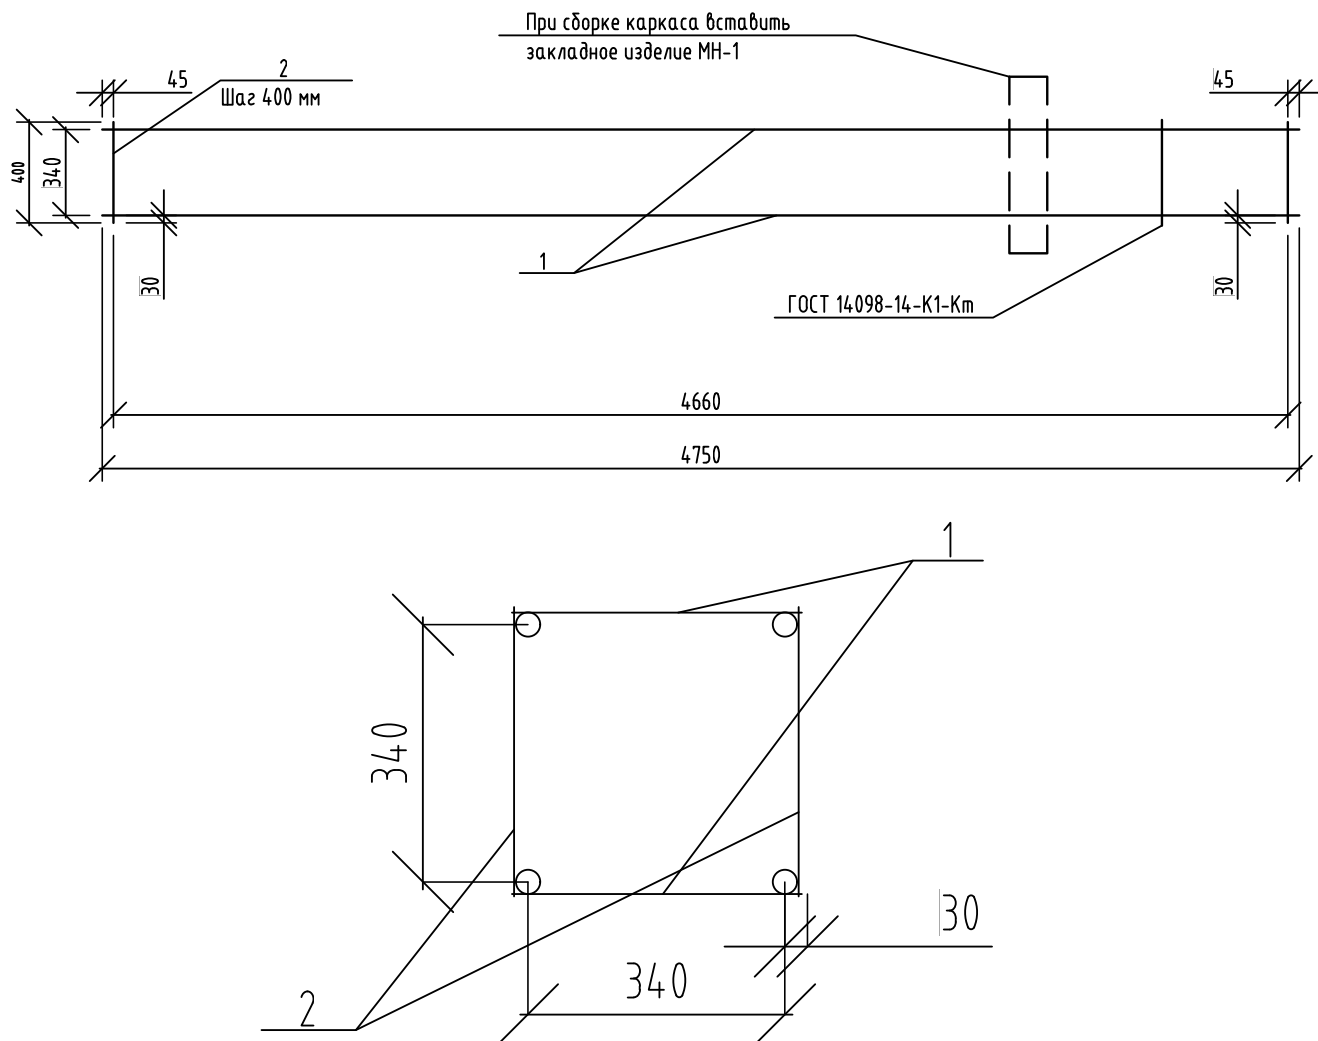

Спецификация элементов

Марка	Обозначение	Наименование	Кол.	Масса ед., кг	Примечание
		Сварочные единицы			
КР-1		Каркас плоский КР1	2		
		Детали			
МН-1		Изделия закладные МН1			
		Стержни ГОСТ Р 52544-2006 10 L = 370 мм	11		

Инв. № подл.	Взам. инв. №	Подпись и дата	Д.ИСА.08.03.01.06201102.КП.25-КЖ			
			Многоэтажное промышленное здание с железобетонным каркасом			
		Изм.	Кол. уч.	Лист	№ док.	Подпись
		Студент		Бадри Х.Х.	23.06	
		Консультант		Редикульцев	23.06	
		Консультант		Редикульцев	23.06	
		Руководитель		Редикульцев	23.06	
		Н.контр.		Уфимцева	23.06	
		Зав. каф		Беляева	23.06	
			Сборное железобетонное колонн			Стадия
						Лист
						Листов
			Каркас пространственный КП1			УрФУ
						кафедра СКМГ

Схема расположения главных и второстепенных балок



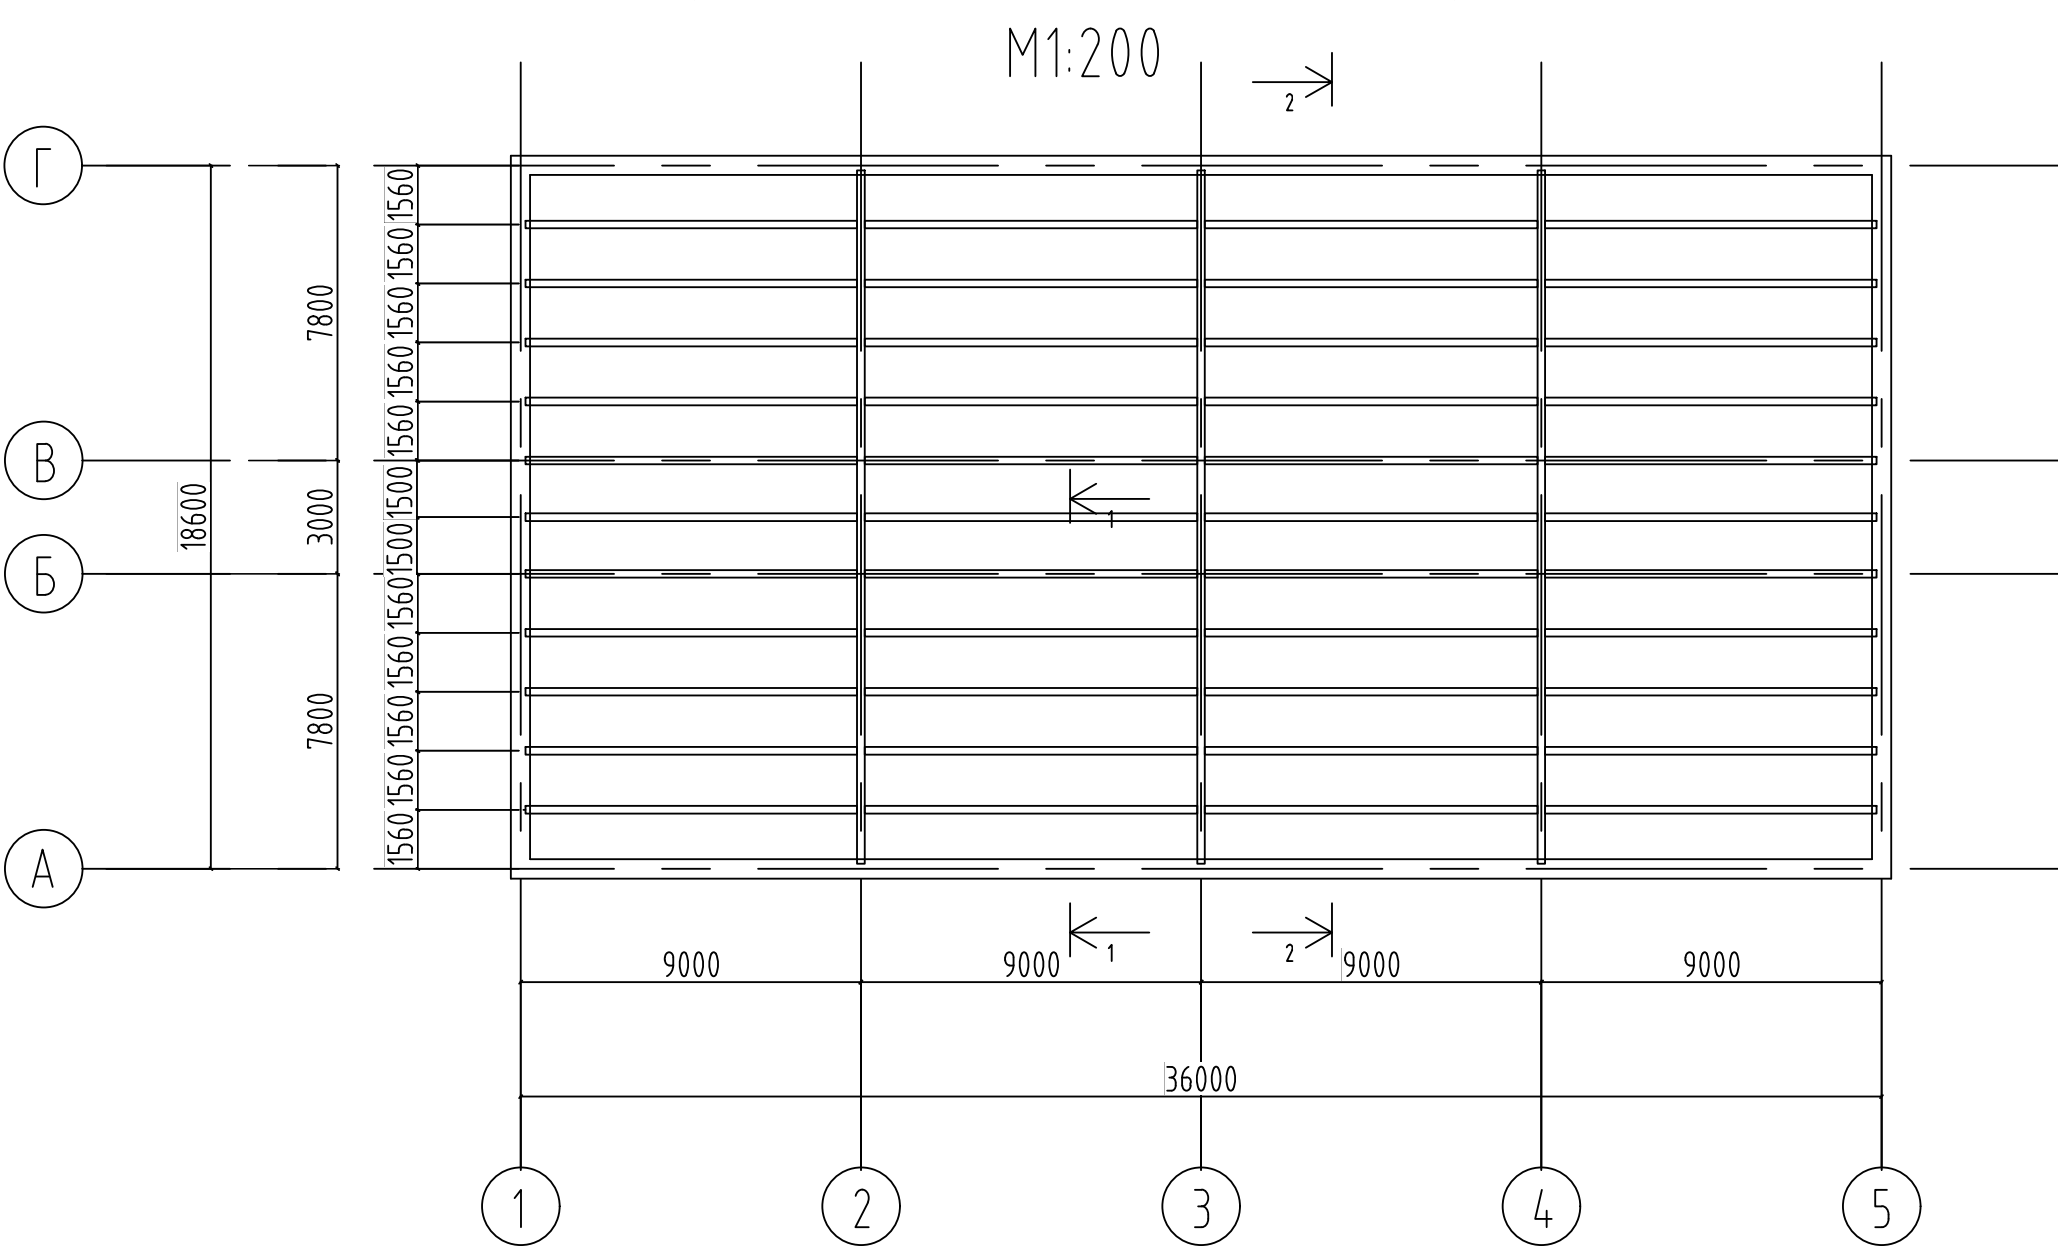



Схема армирования монолитного перекрытия рулонными сетками

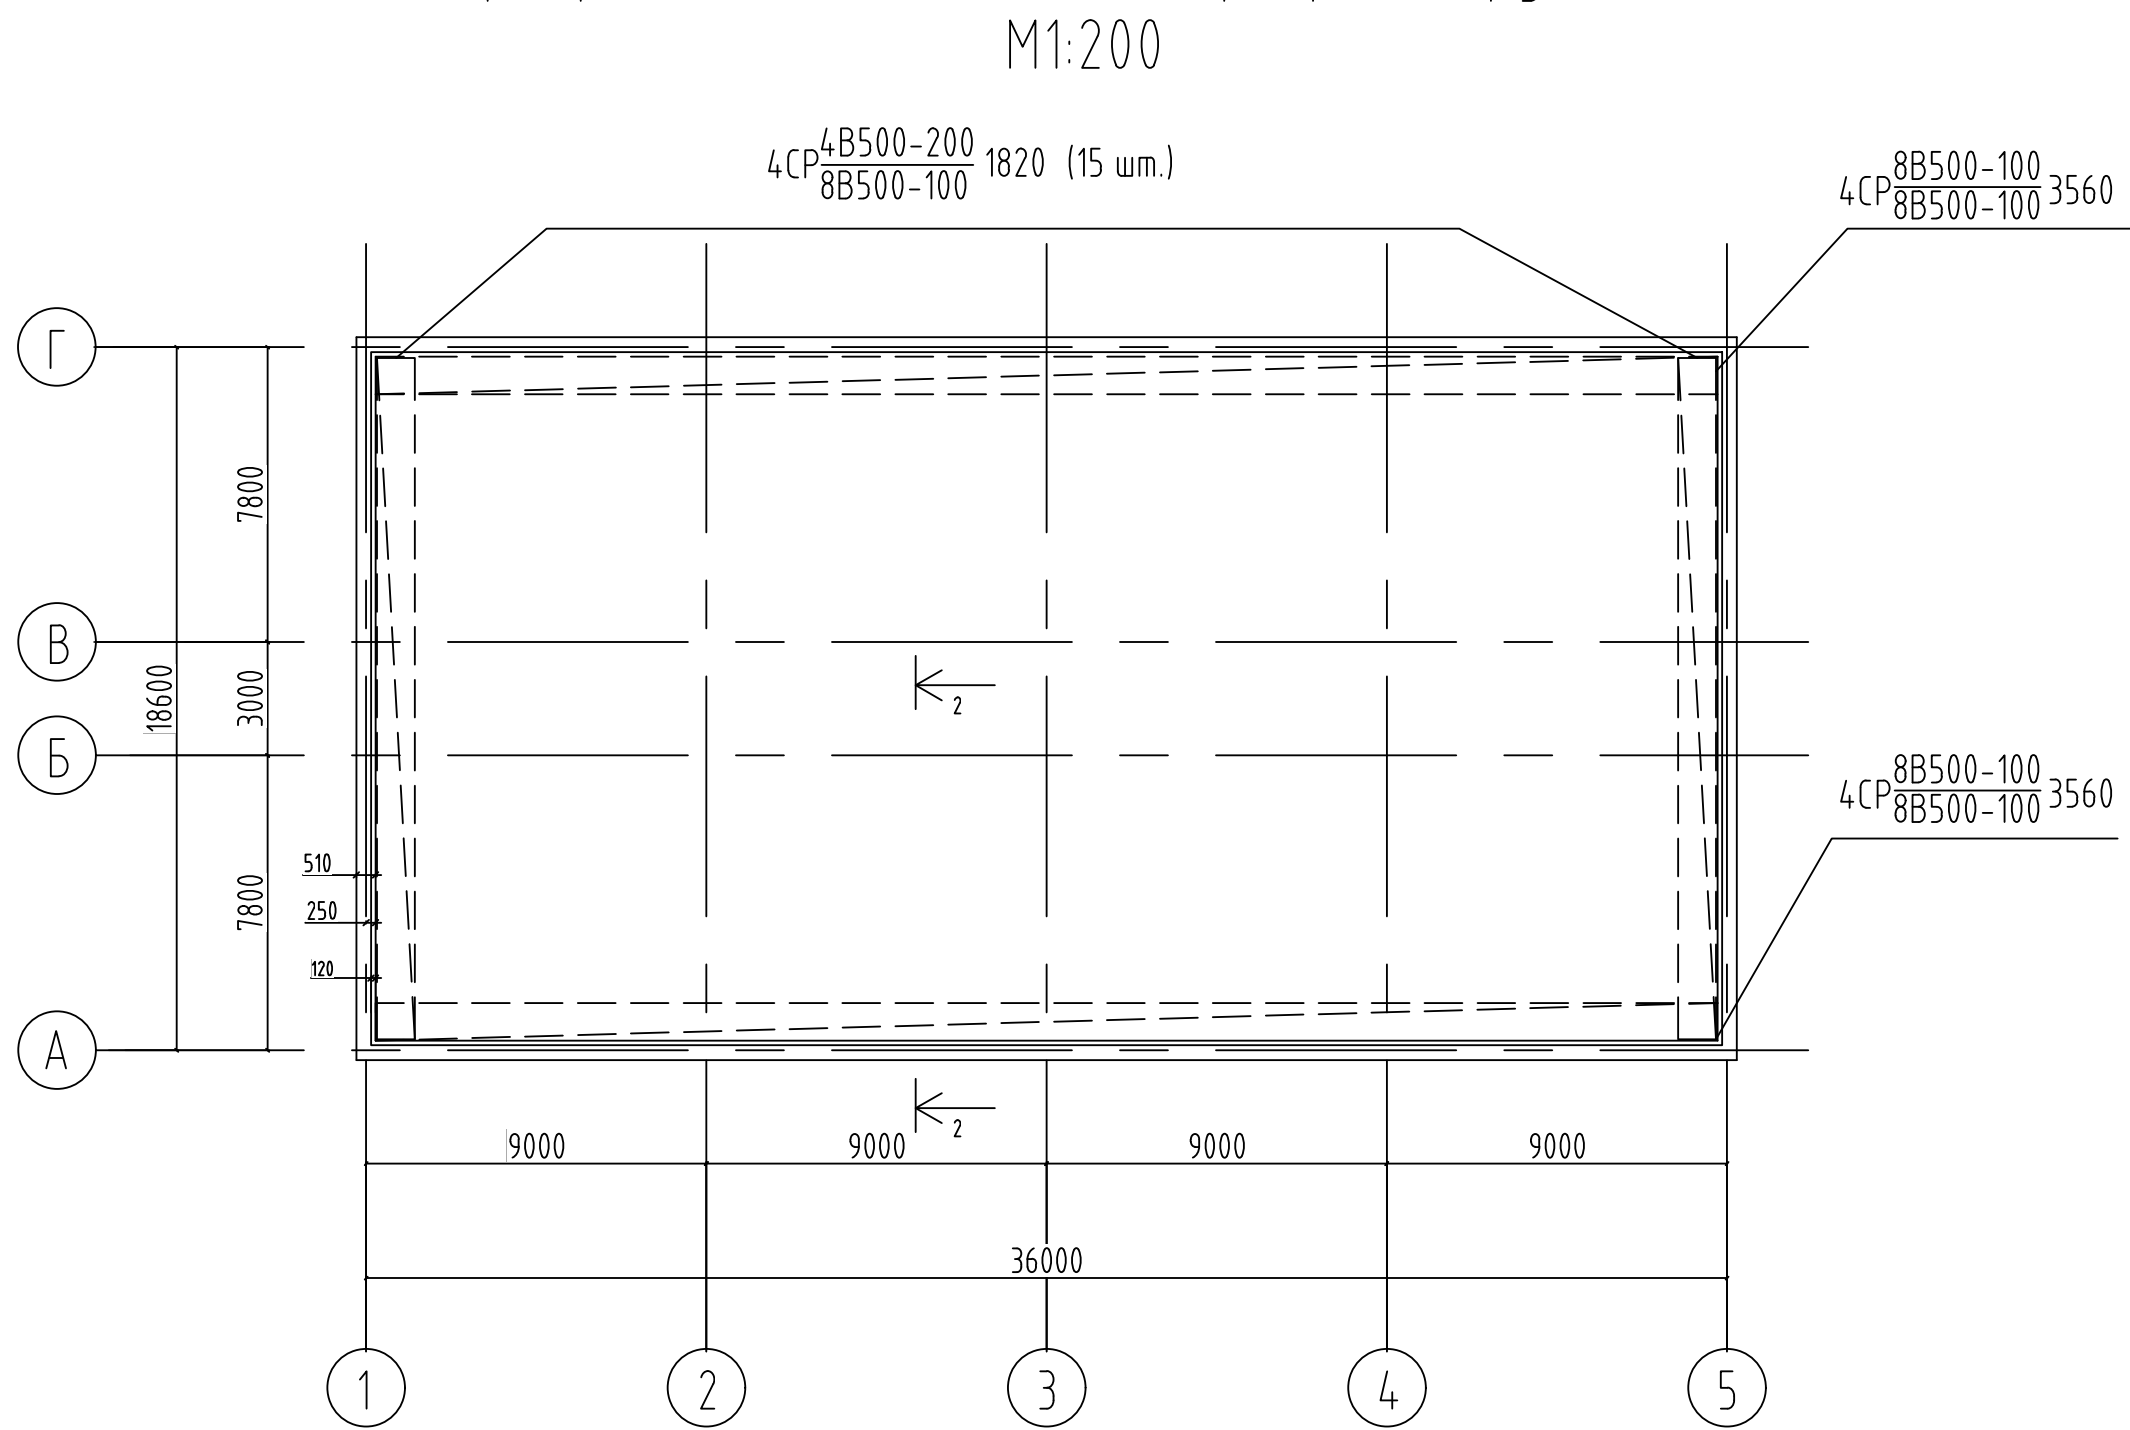

Поперечный разрез 2-2

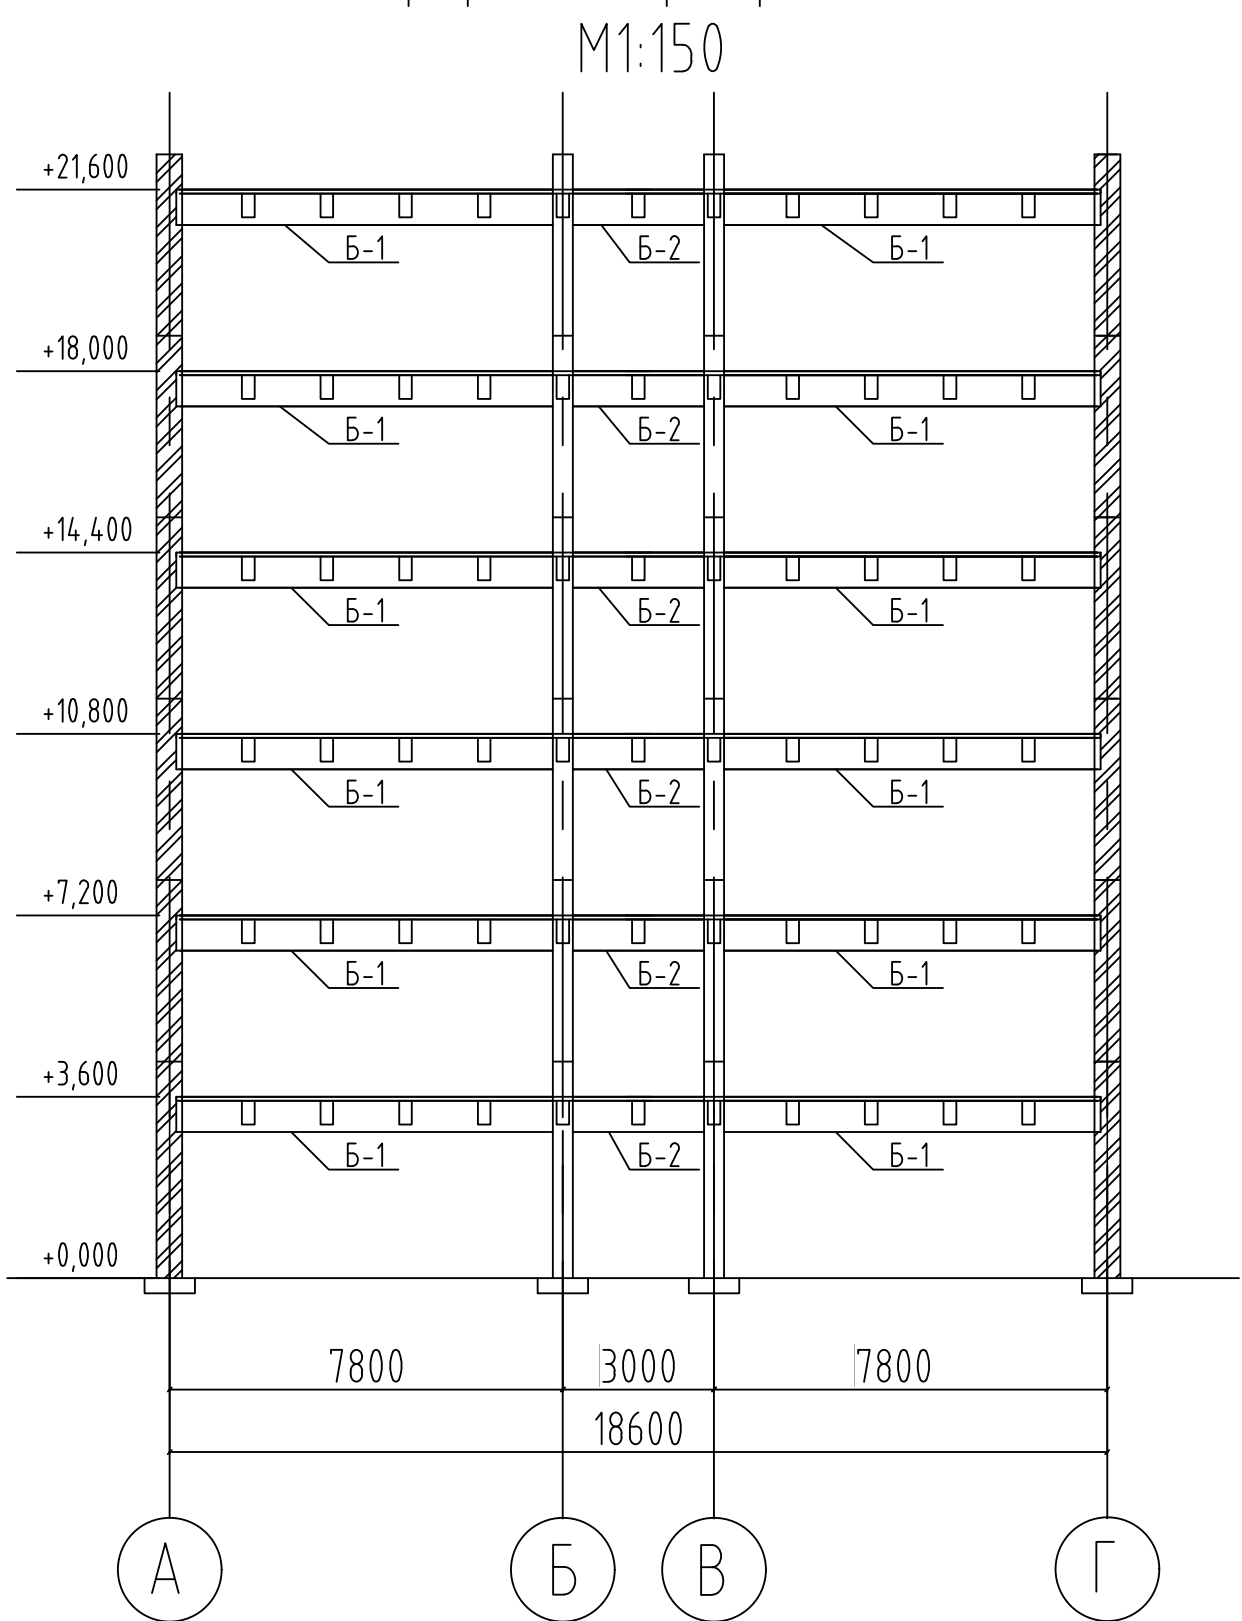


Конструктивная схема монолитной плиты (Разрез 1-1)

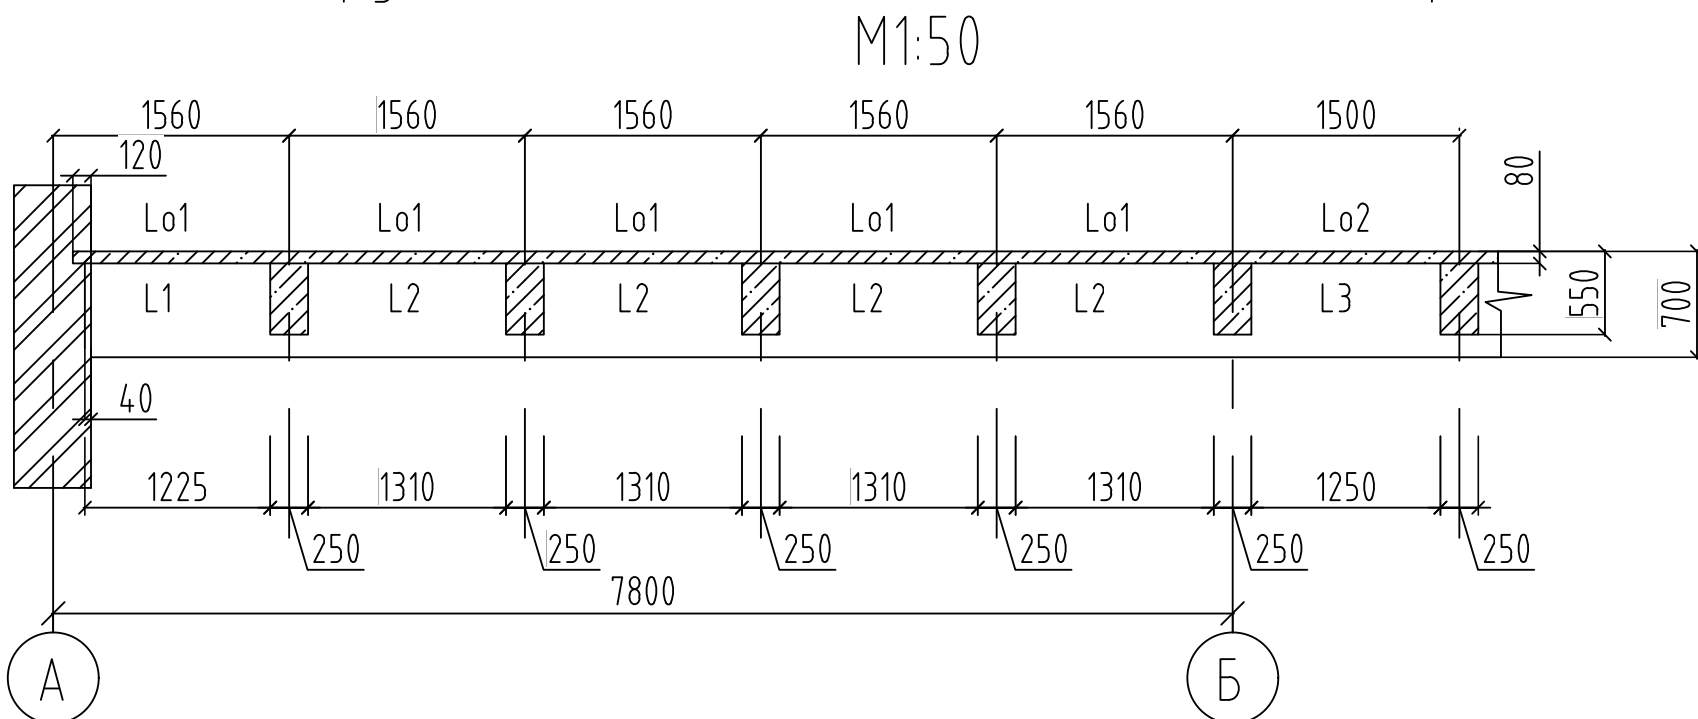


Инф. № подл.	Подпись и дата	Взам. инв. №

Д.ИСА.08.03.01.06201102.КП.25-КЖ					
Многоэтажное промышленное здание с железобетонным каркасом					
Изм.	Кол. уч.	Лист	№ док.	Подпись	Дата
Студент	Бадри Х.Х.	23.06			
Консультант	Редикунцев	23.06			
Консультант	Редикунцев	23.06			
Руководитель	Редикунцев	23.06			
Н.контр.	Уфимцева	23.06			
Зав. каф.	Беляева	23.06			
Сборное железобетонное перекрытие				Стадия	Лист
				у	5
Схема расположения главных и второстепенных балок				УрФУ кафедра СКМГ	


Схема армирования Б1
М1:40

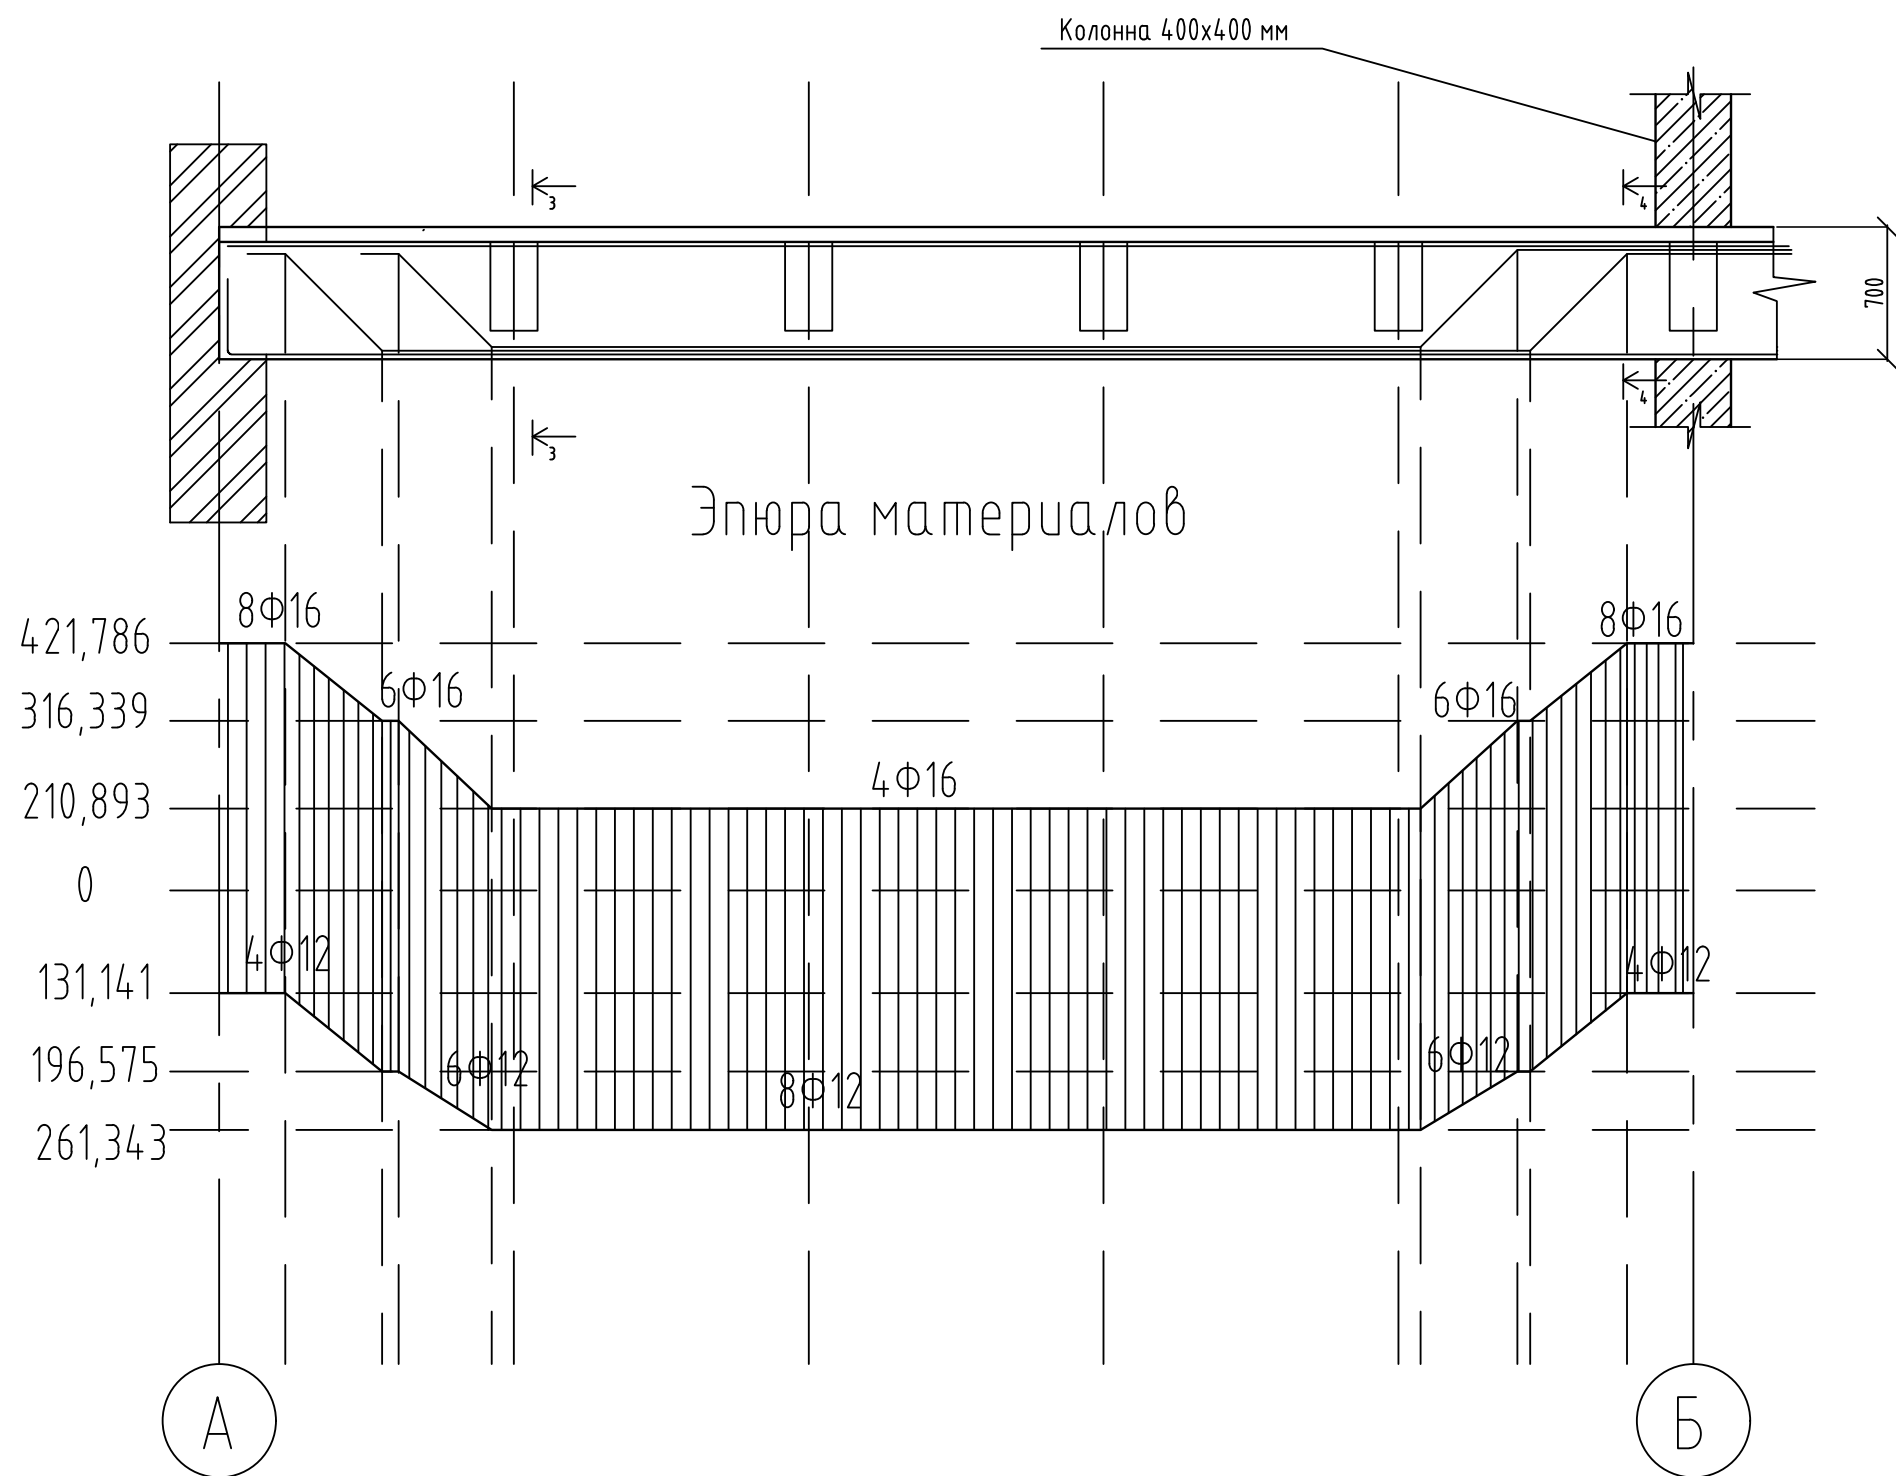


Разрез 2-2(5)
М1:40

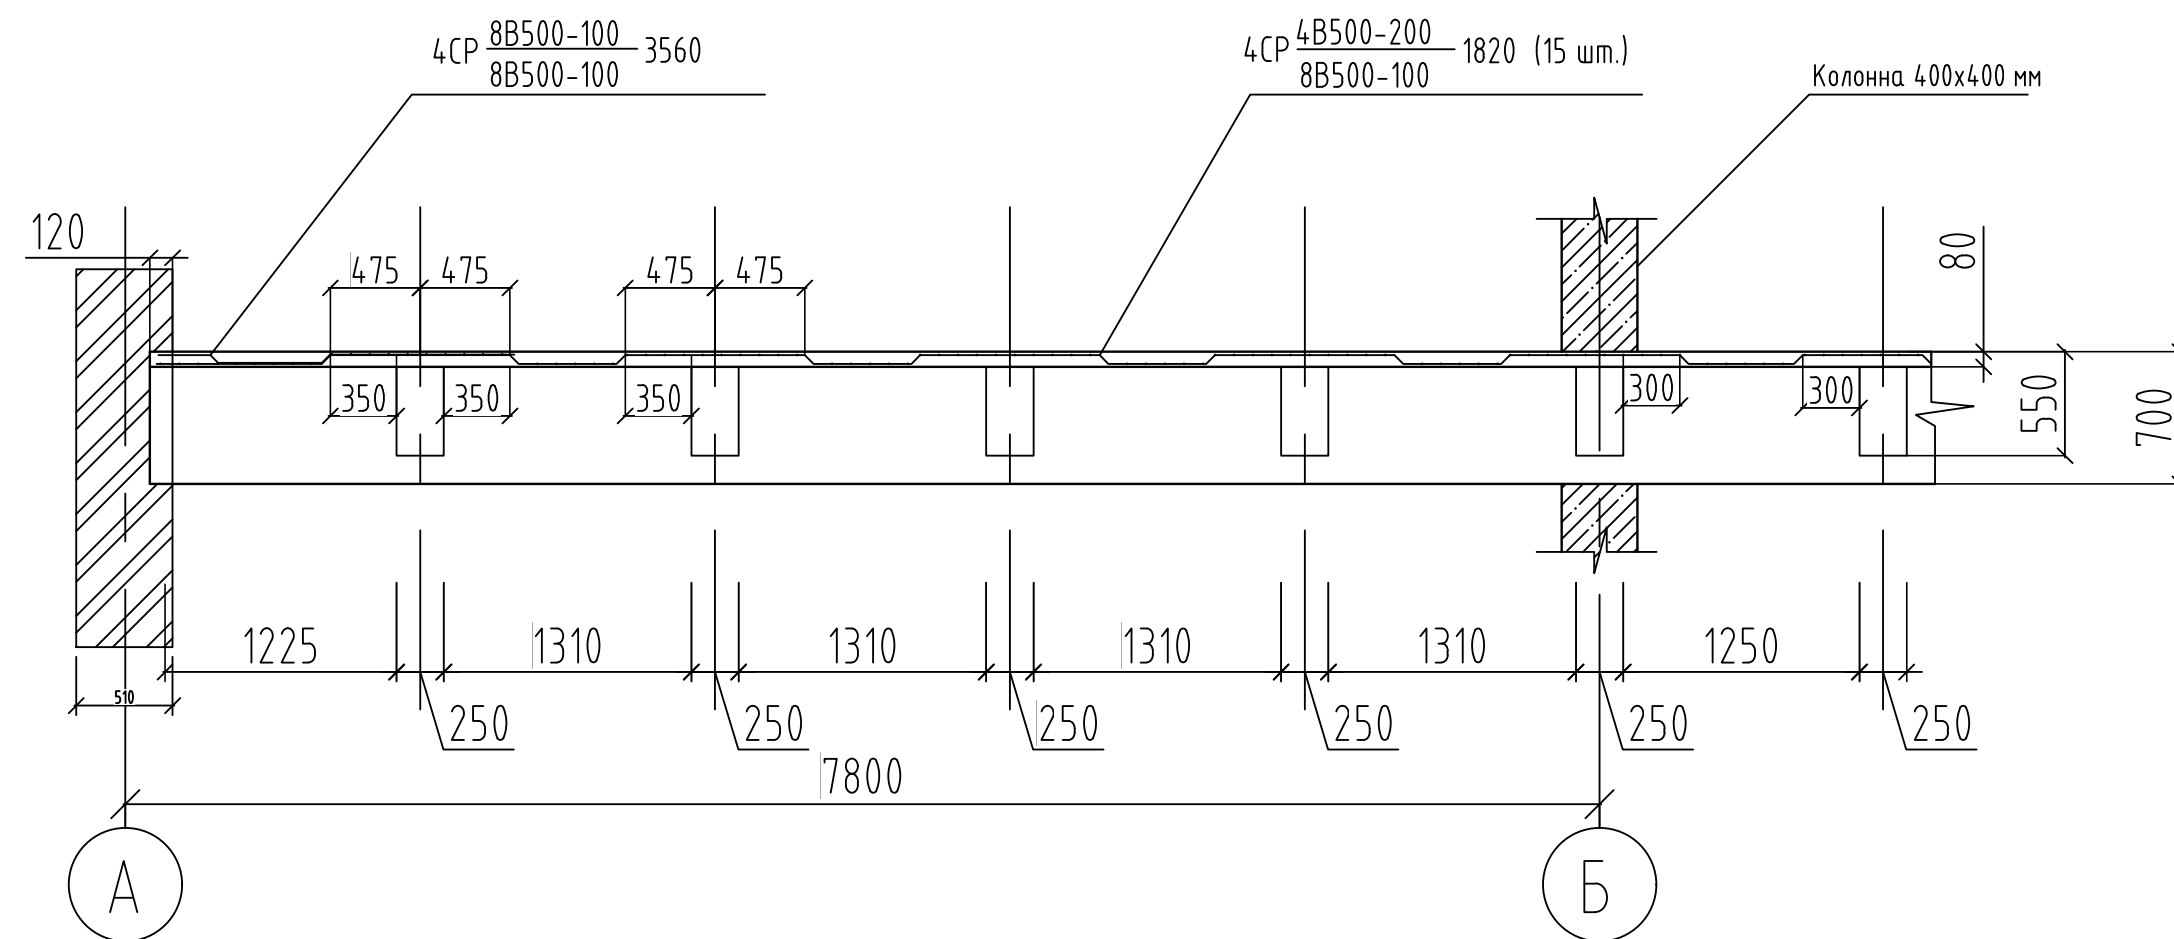


Расчетная схема

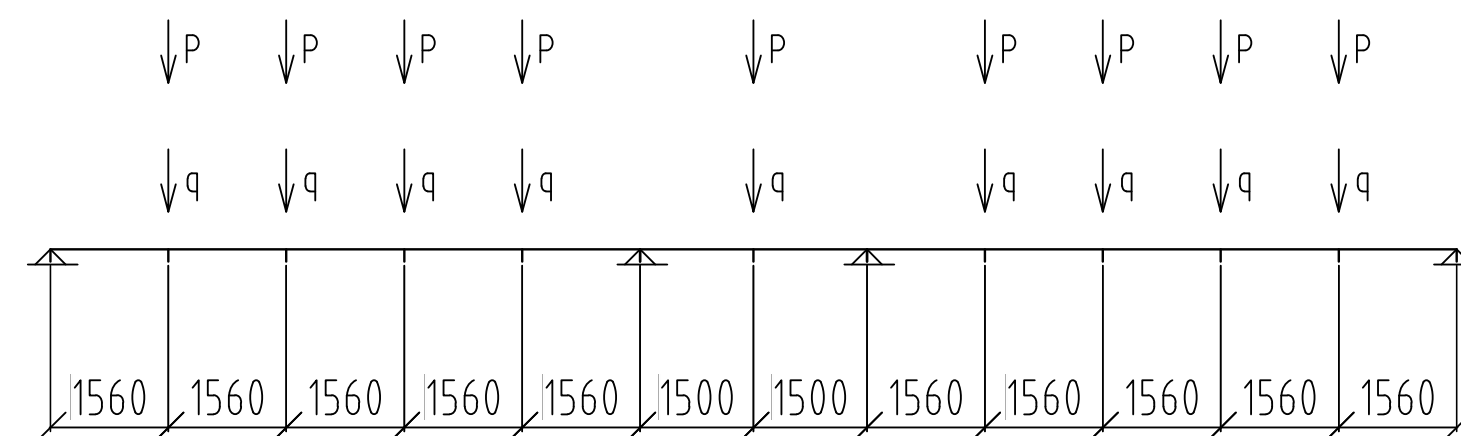

Разрез 4-4

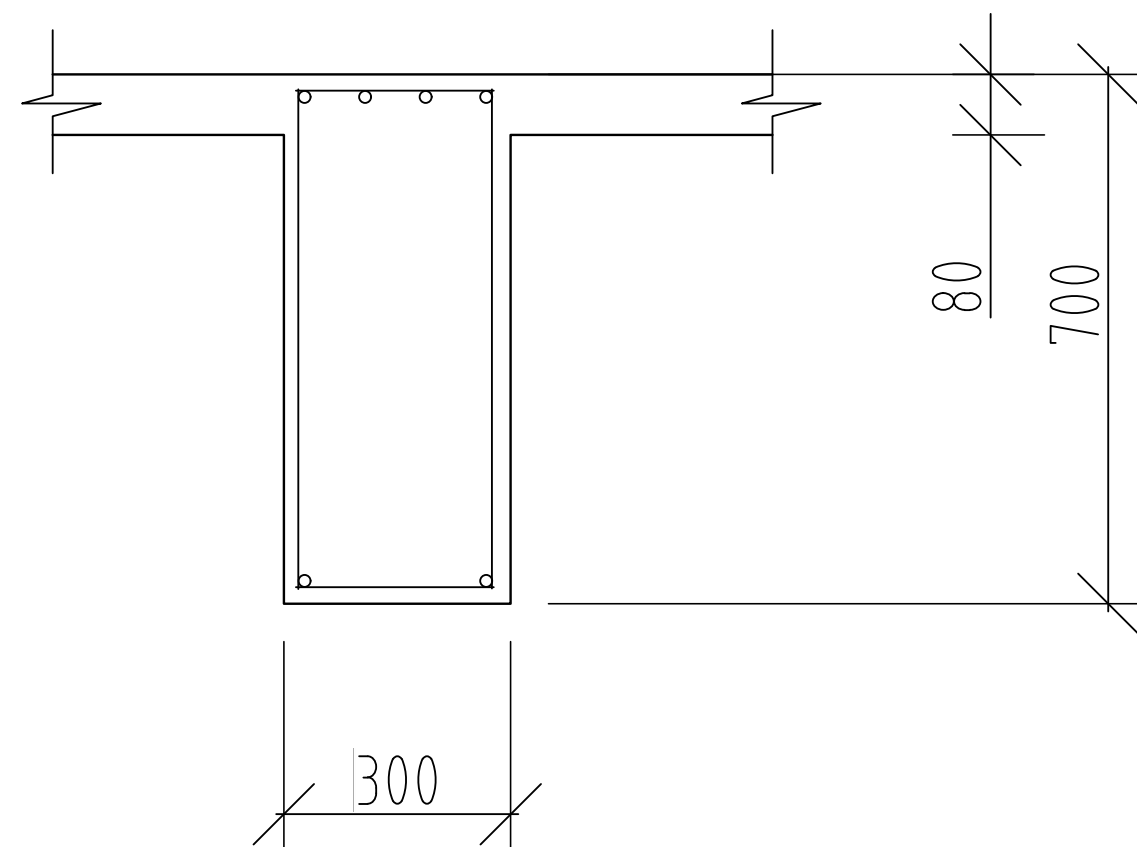

Разрез 3-3

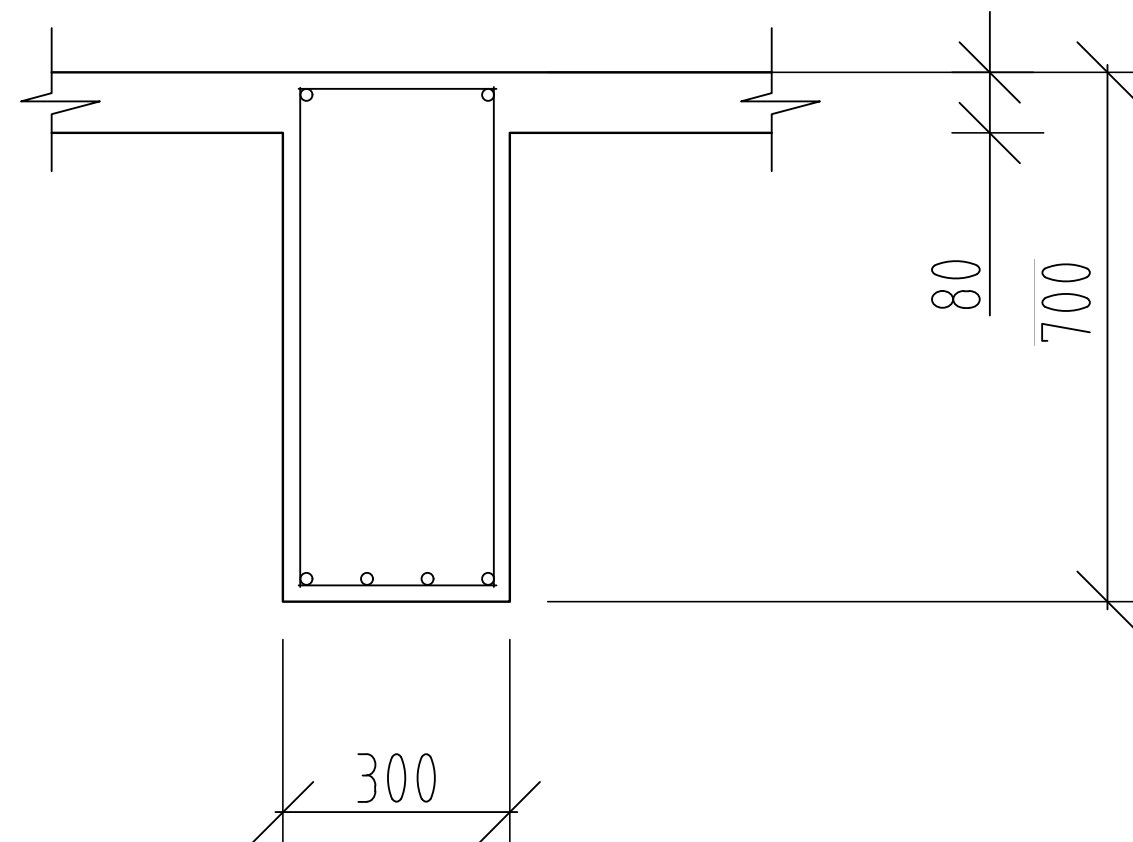

							Д.ИСА.08.03.01.06201102.КП.25-КЖ			
							Многоэтажное промышленное здание с железобетонным каркасом			
Изм.	Кол. уч.	Лист	N док.	Подпись	Дата	Сборное железобетонное перекрытие		Стадия	Лист	Листов
Студент		Бадри Х.Х.			23.06			У	6	6
Консультант		Редикунцев			23.06					
Консультант		Редикунцев			23.06					
Руководитель		Редикунцев			23.06					
Н.контр.		Уфимцева			23.06	Схема армирования Б1 и Эпюра материалов		Урфу кафедра СКМГ		
Зав. каф.		Беляева			23.06					