



Схема расположения колонн

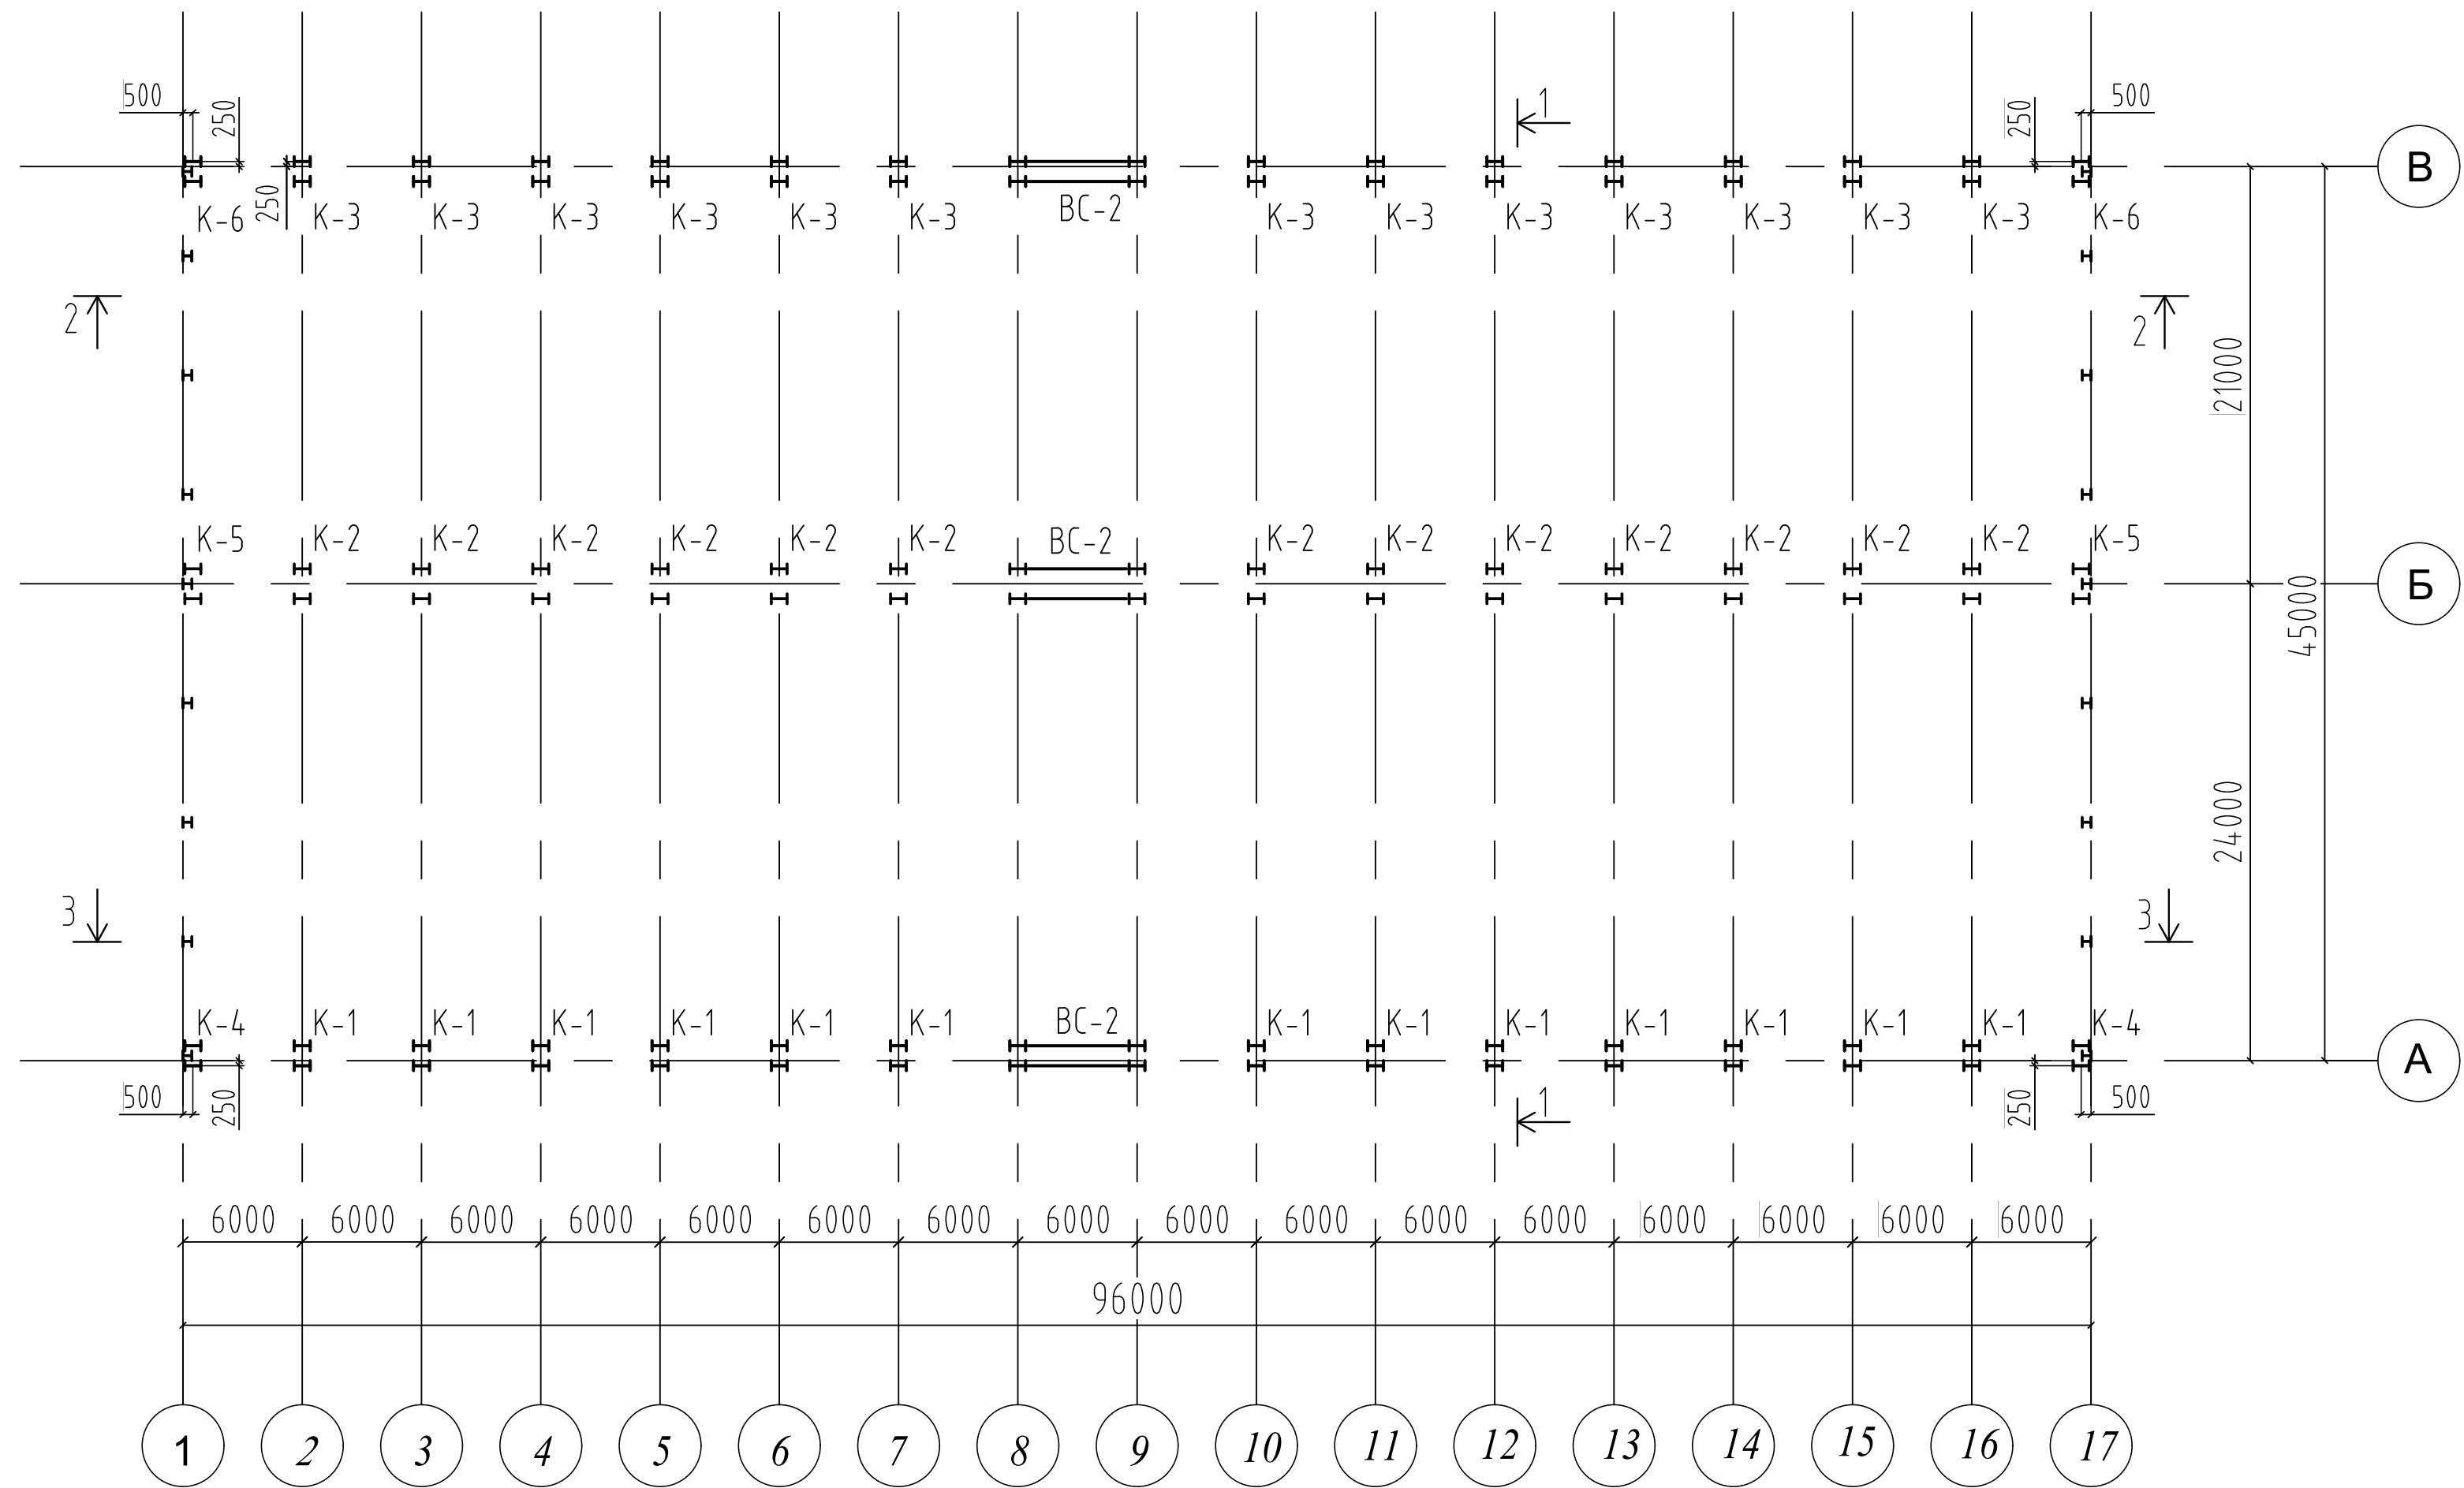

Ведомость элементов

Марка элемента	Сечение			Усилия			Группа констр.	Марка стали	Примечание
	эскиз	поз.	состав	Q, тс	N, тс	M, тс*м			
K1			70Б1					C355	
			30Б2, 30Б2					C355	
K2								C355	
								C355	
K3								C355	
								C355	
K4								C355	
								C355	
K5								C355	
								C355	
K6								C355	
								C355	
ФС-1	сложное		-	-	-	-		C355	лист
P-1			2L100x10					C355	
P-2			2L100x10					C355	
C-1			2L100x10					C355	
C-2			2L100x10					C355	
C-3			2L80x10					C355	
C-4			2L80x10					C355	
ПР-1			16 y					C355	
ПР-2			16 y					C355	
BC-1			2L100x8					C355	

Схема расположения прогонов

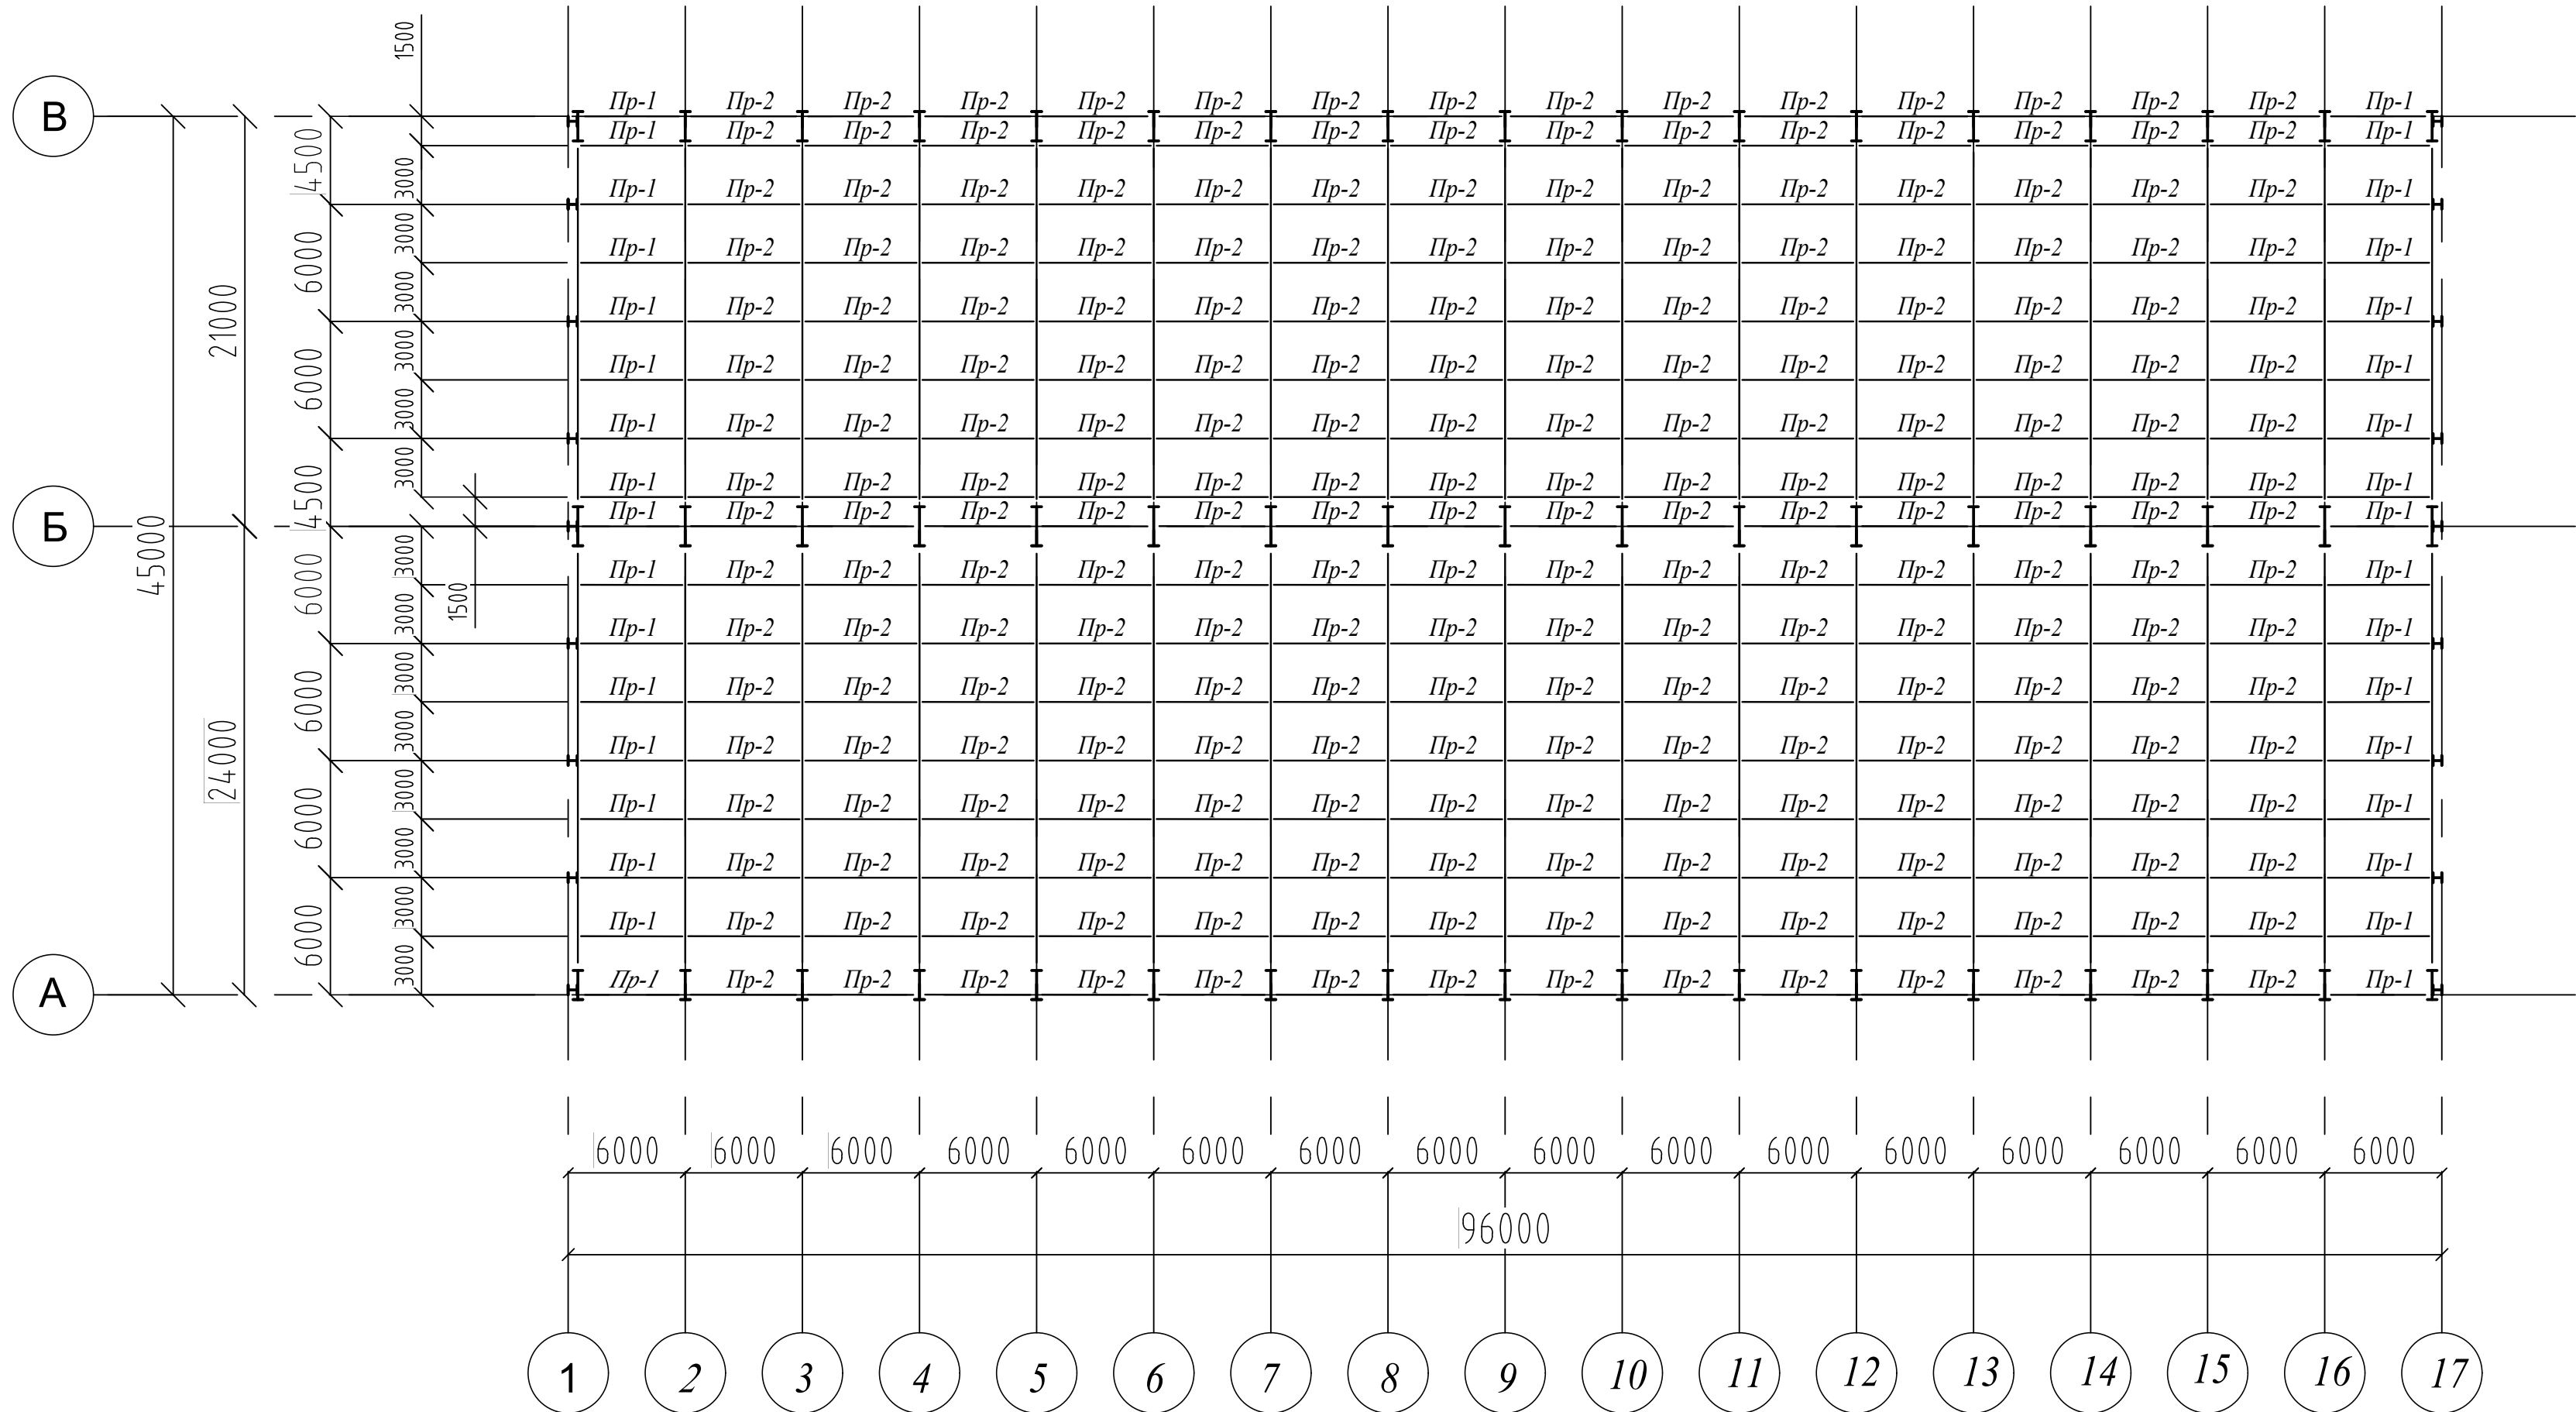

						Д.ИСА.08.03.01.320004.ПМ.3.2025-КМД					
						Расчет и конструирование основных несущих конструкций одноэтажного промышленного здания					
Изм.	Колуч.	Лист	N док.	Подпись	Дата	Здание цеха	Стадия	Лист	Листов	УрФУ кафедра СКиМГ	
Студент	Бадрн Х.Х.				26.05						
Консультант	Карлова				26.05		У	1	5		
Консультант											
	Карлова				26.05						
Руководитель						Схема расположения прогонов, схема расположения колонн					
Н.контр.	Карлова				26.05						
Заб. каф	Беляева				26.05						

Схема расположения элементов покрытия в плоскости нижних поясов ферм



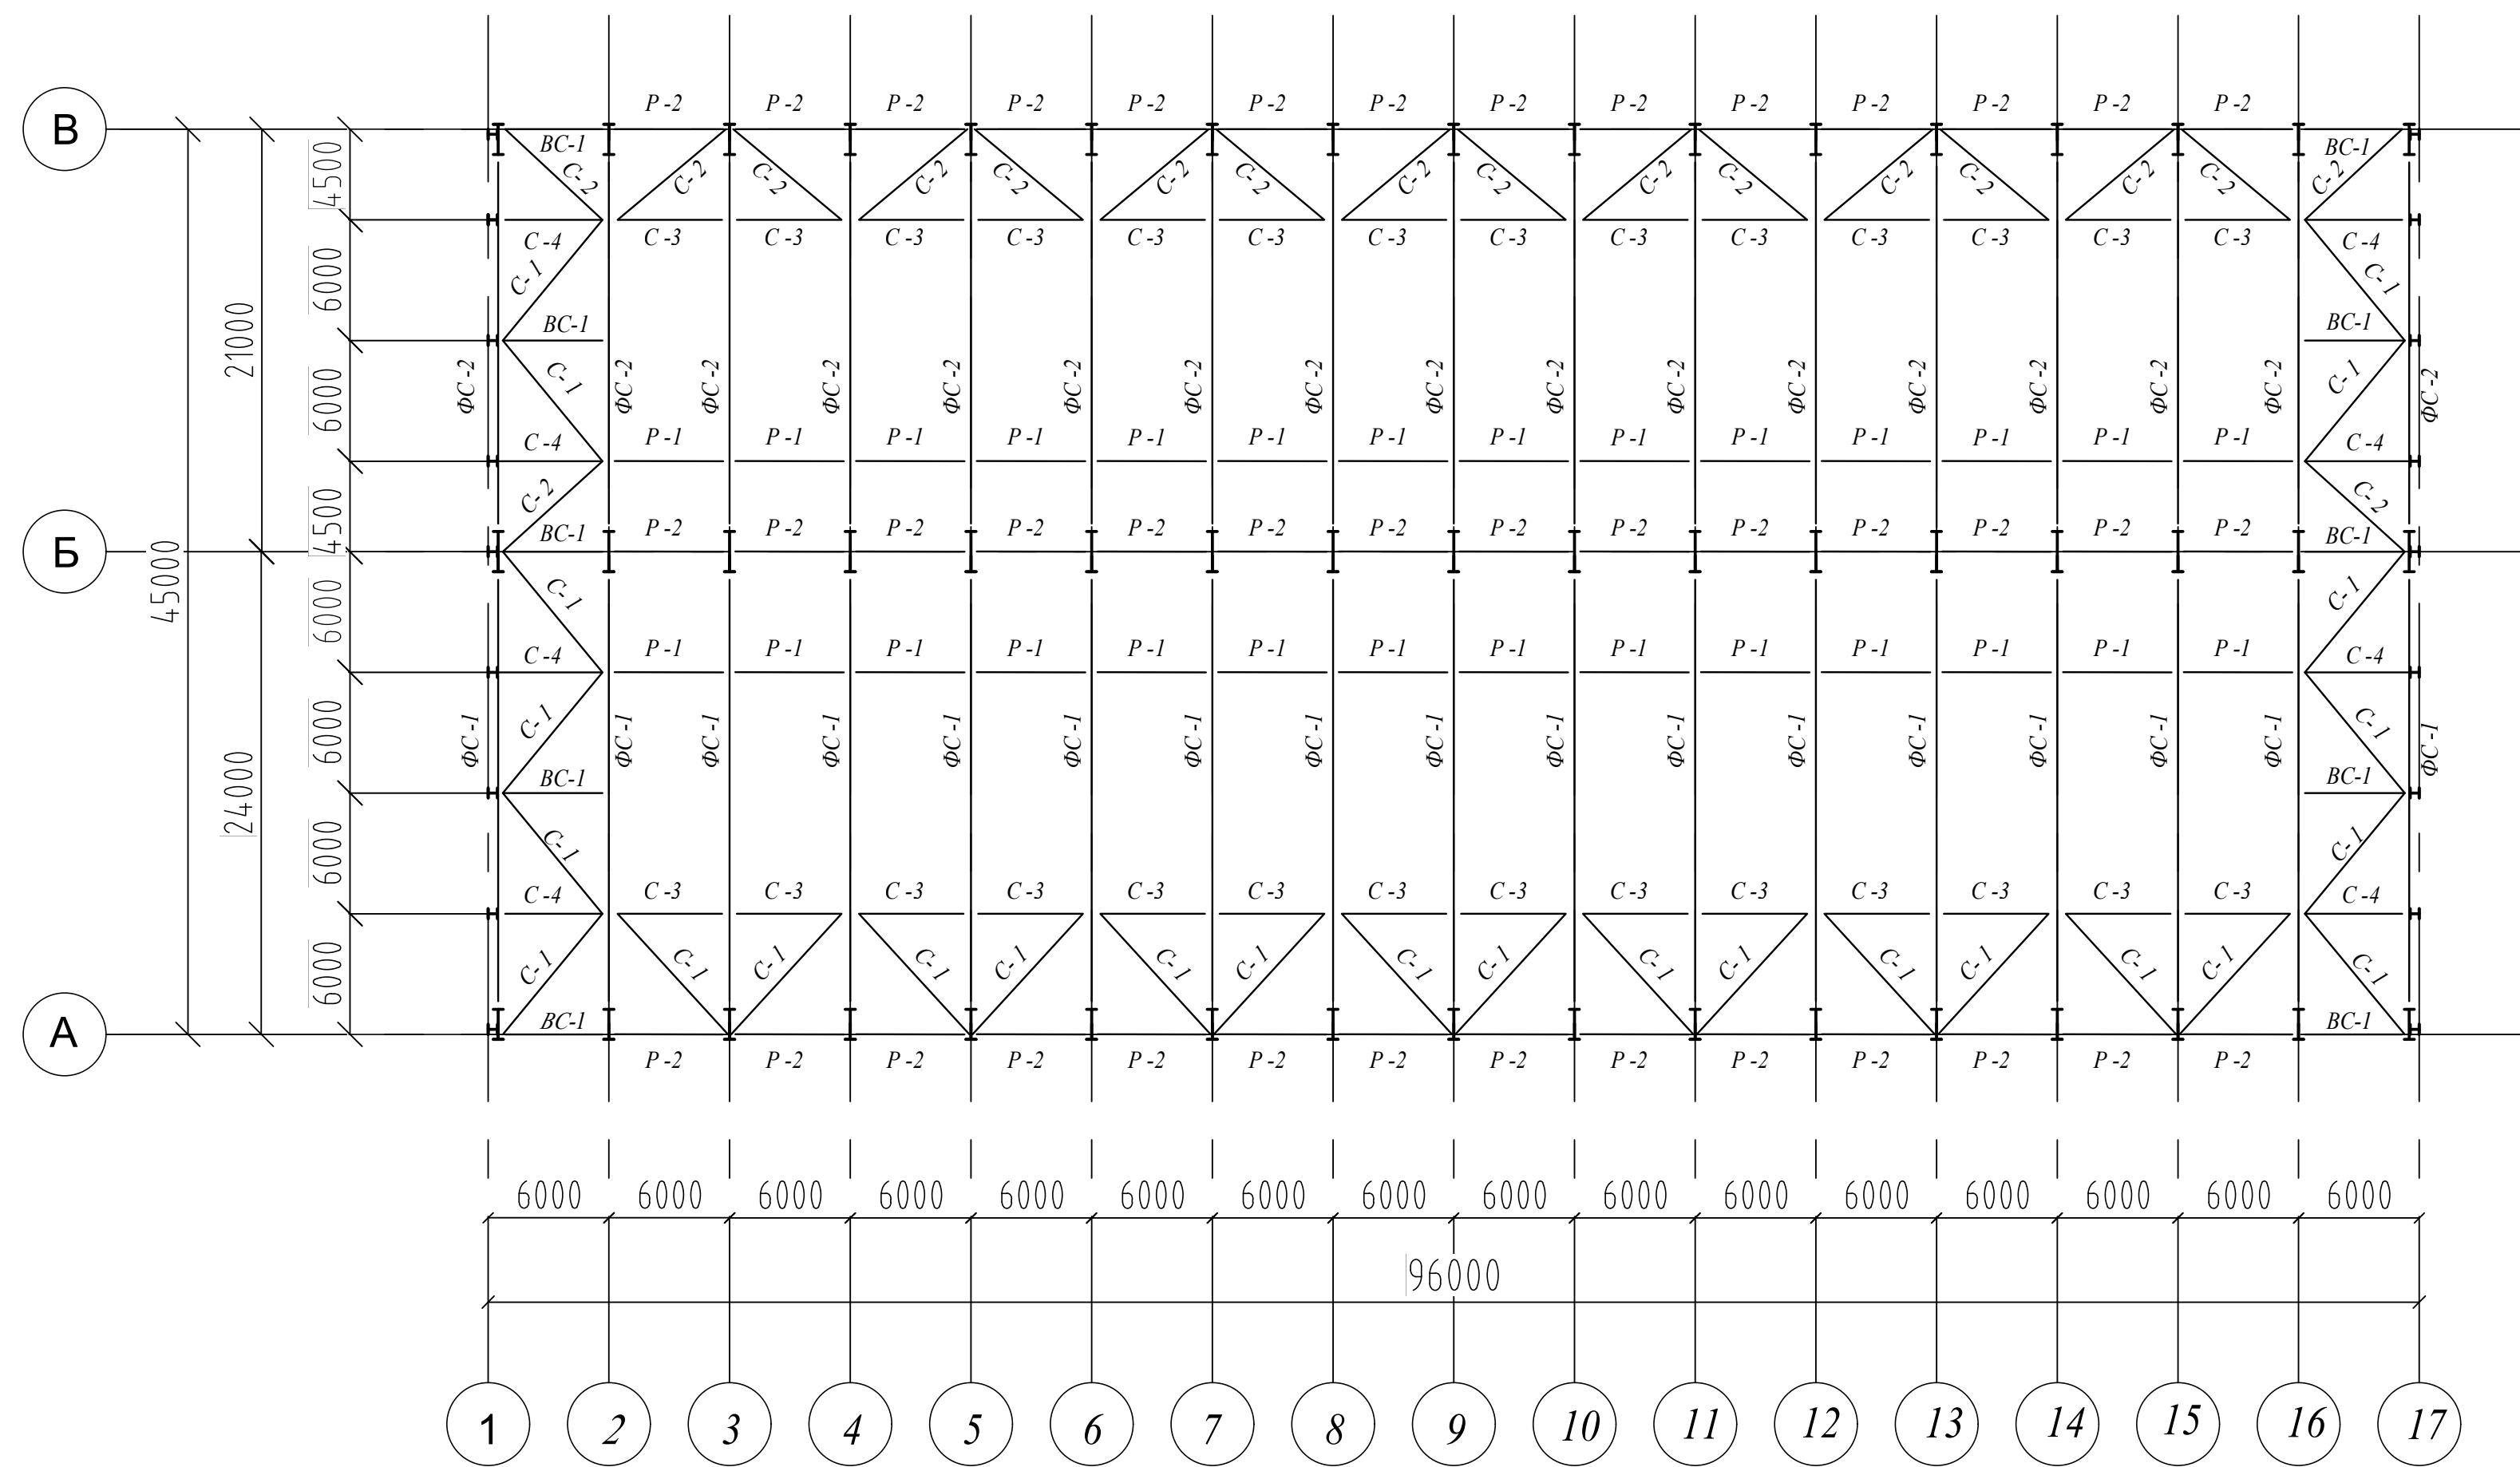


Схема расположения элементов покрытия в плоскости верхних поясов ферм

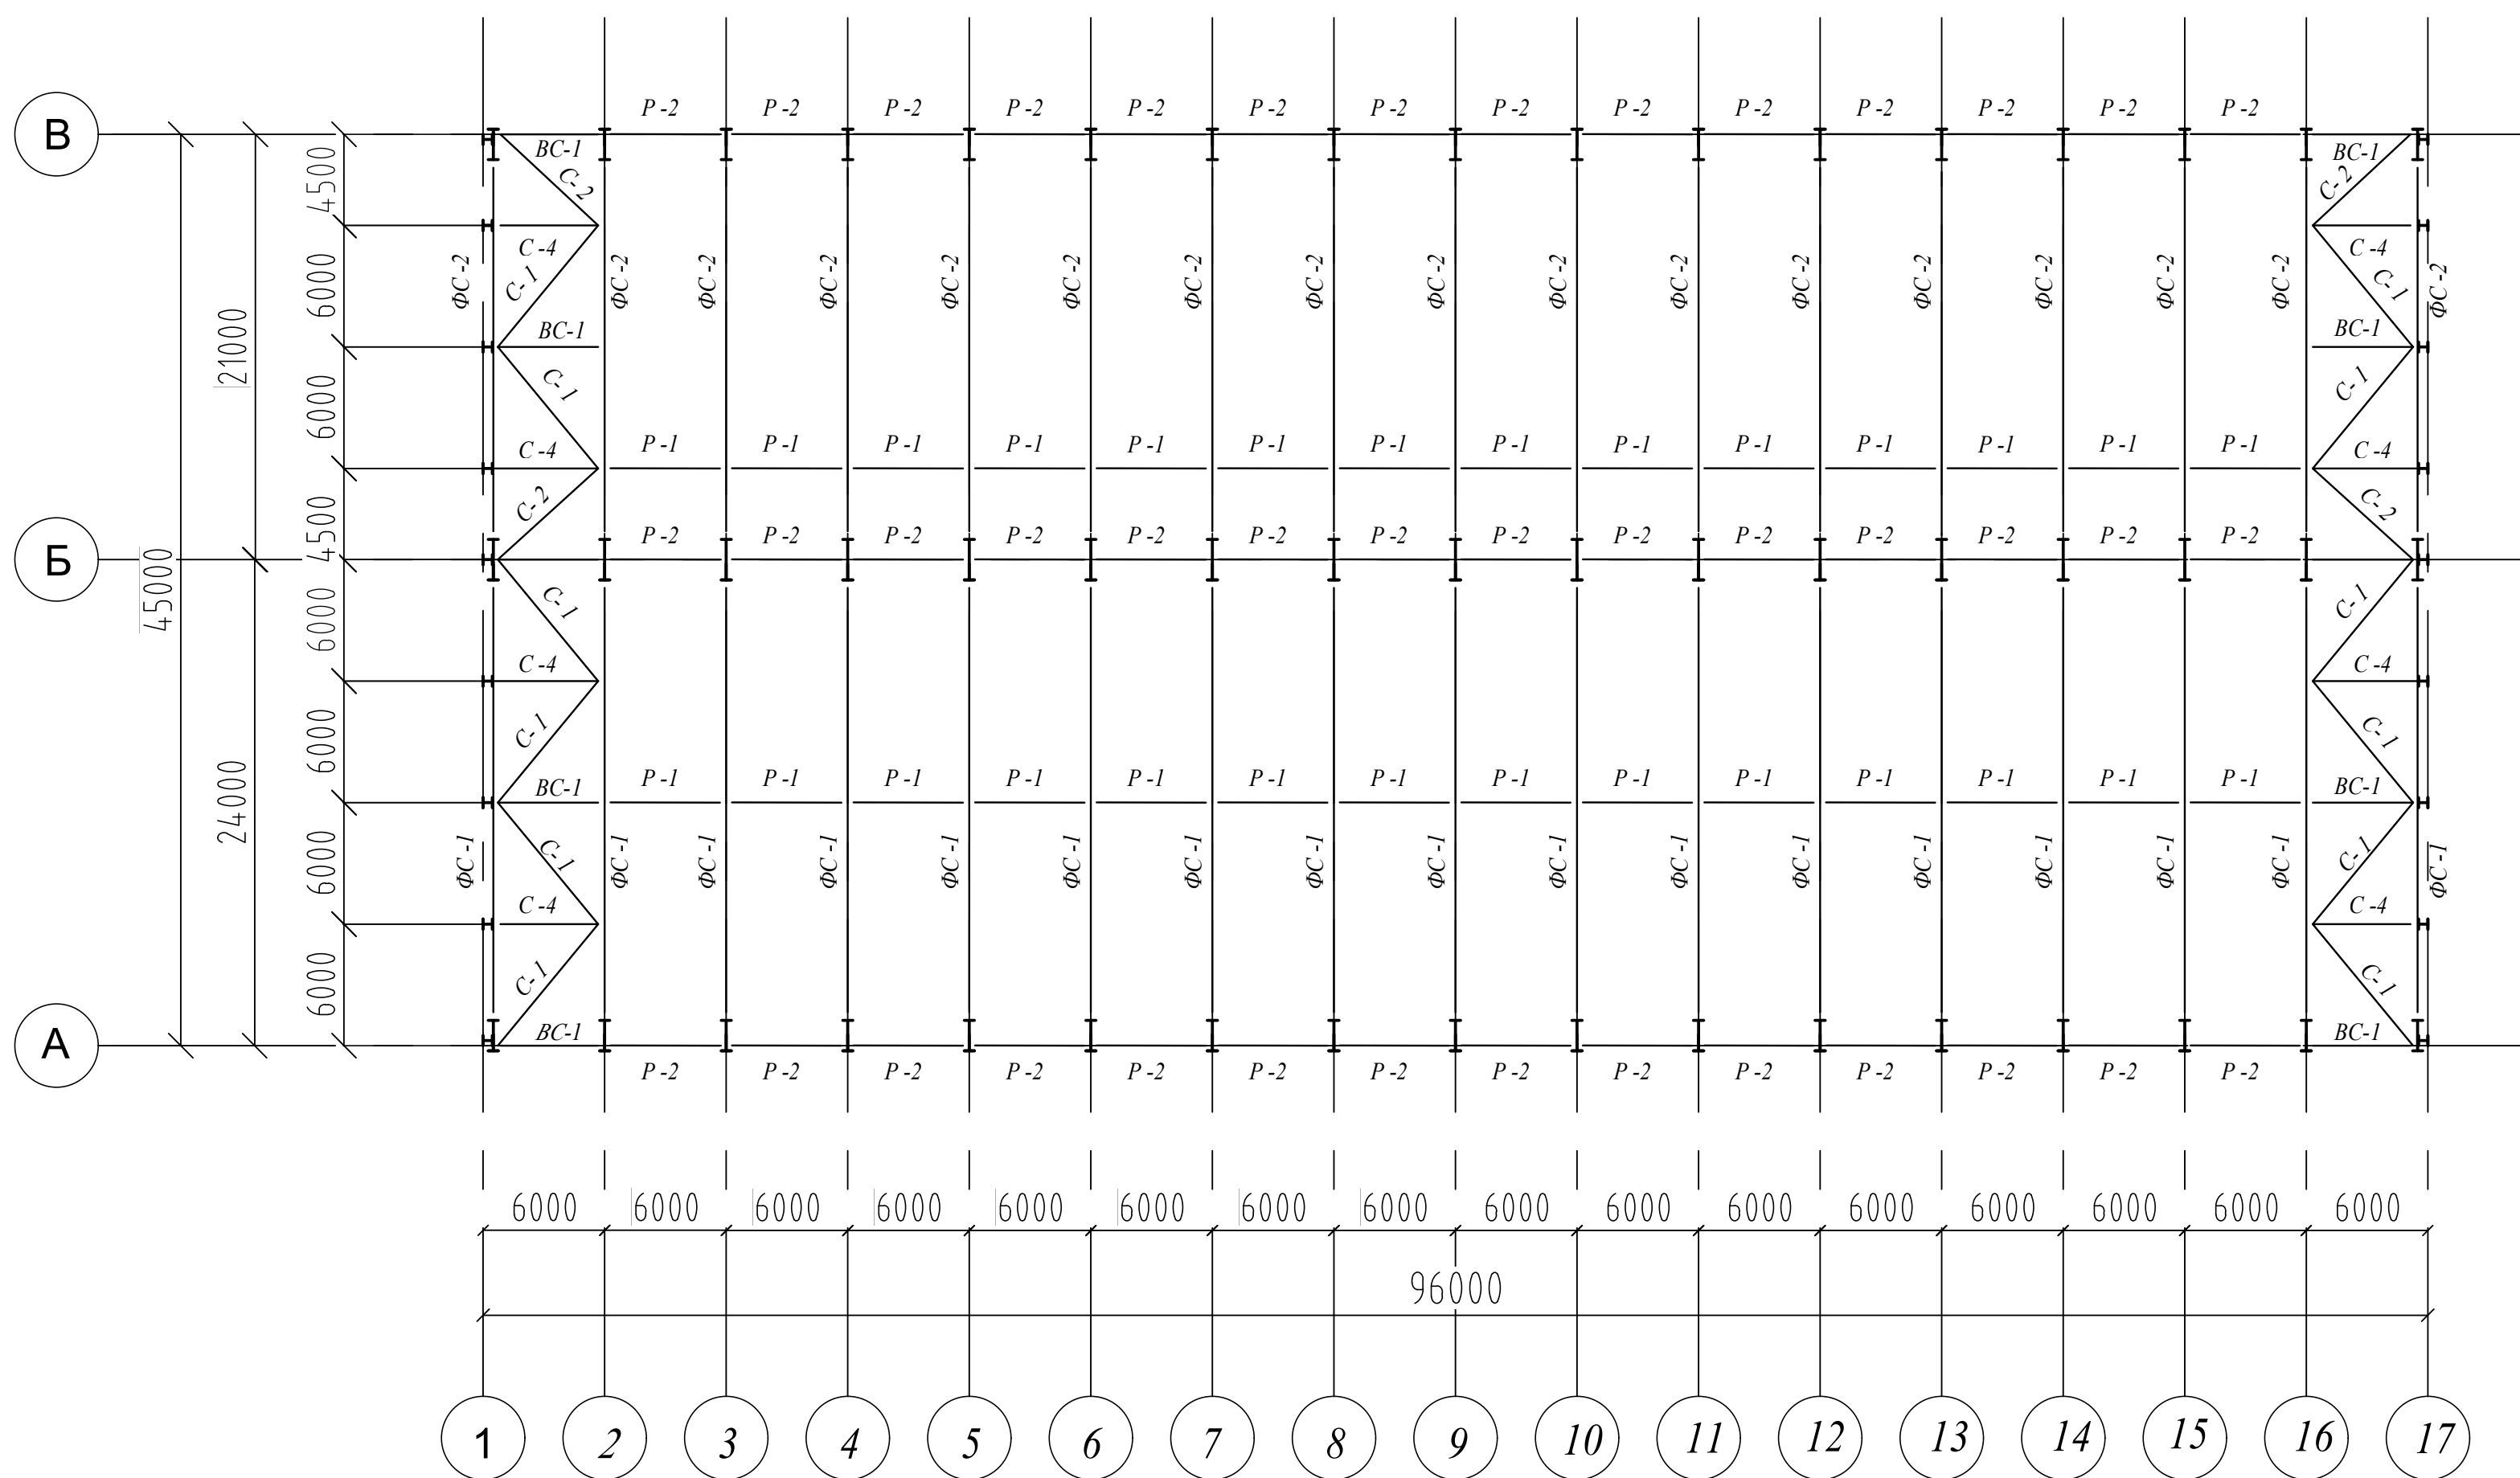


Поперечный разрез здания
Разрез 1-1(1)

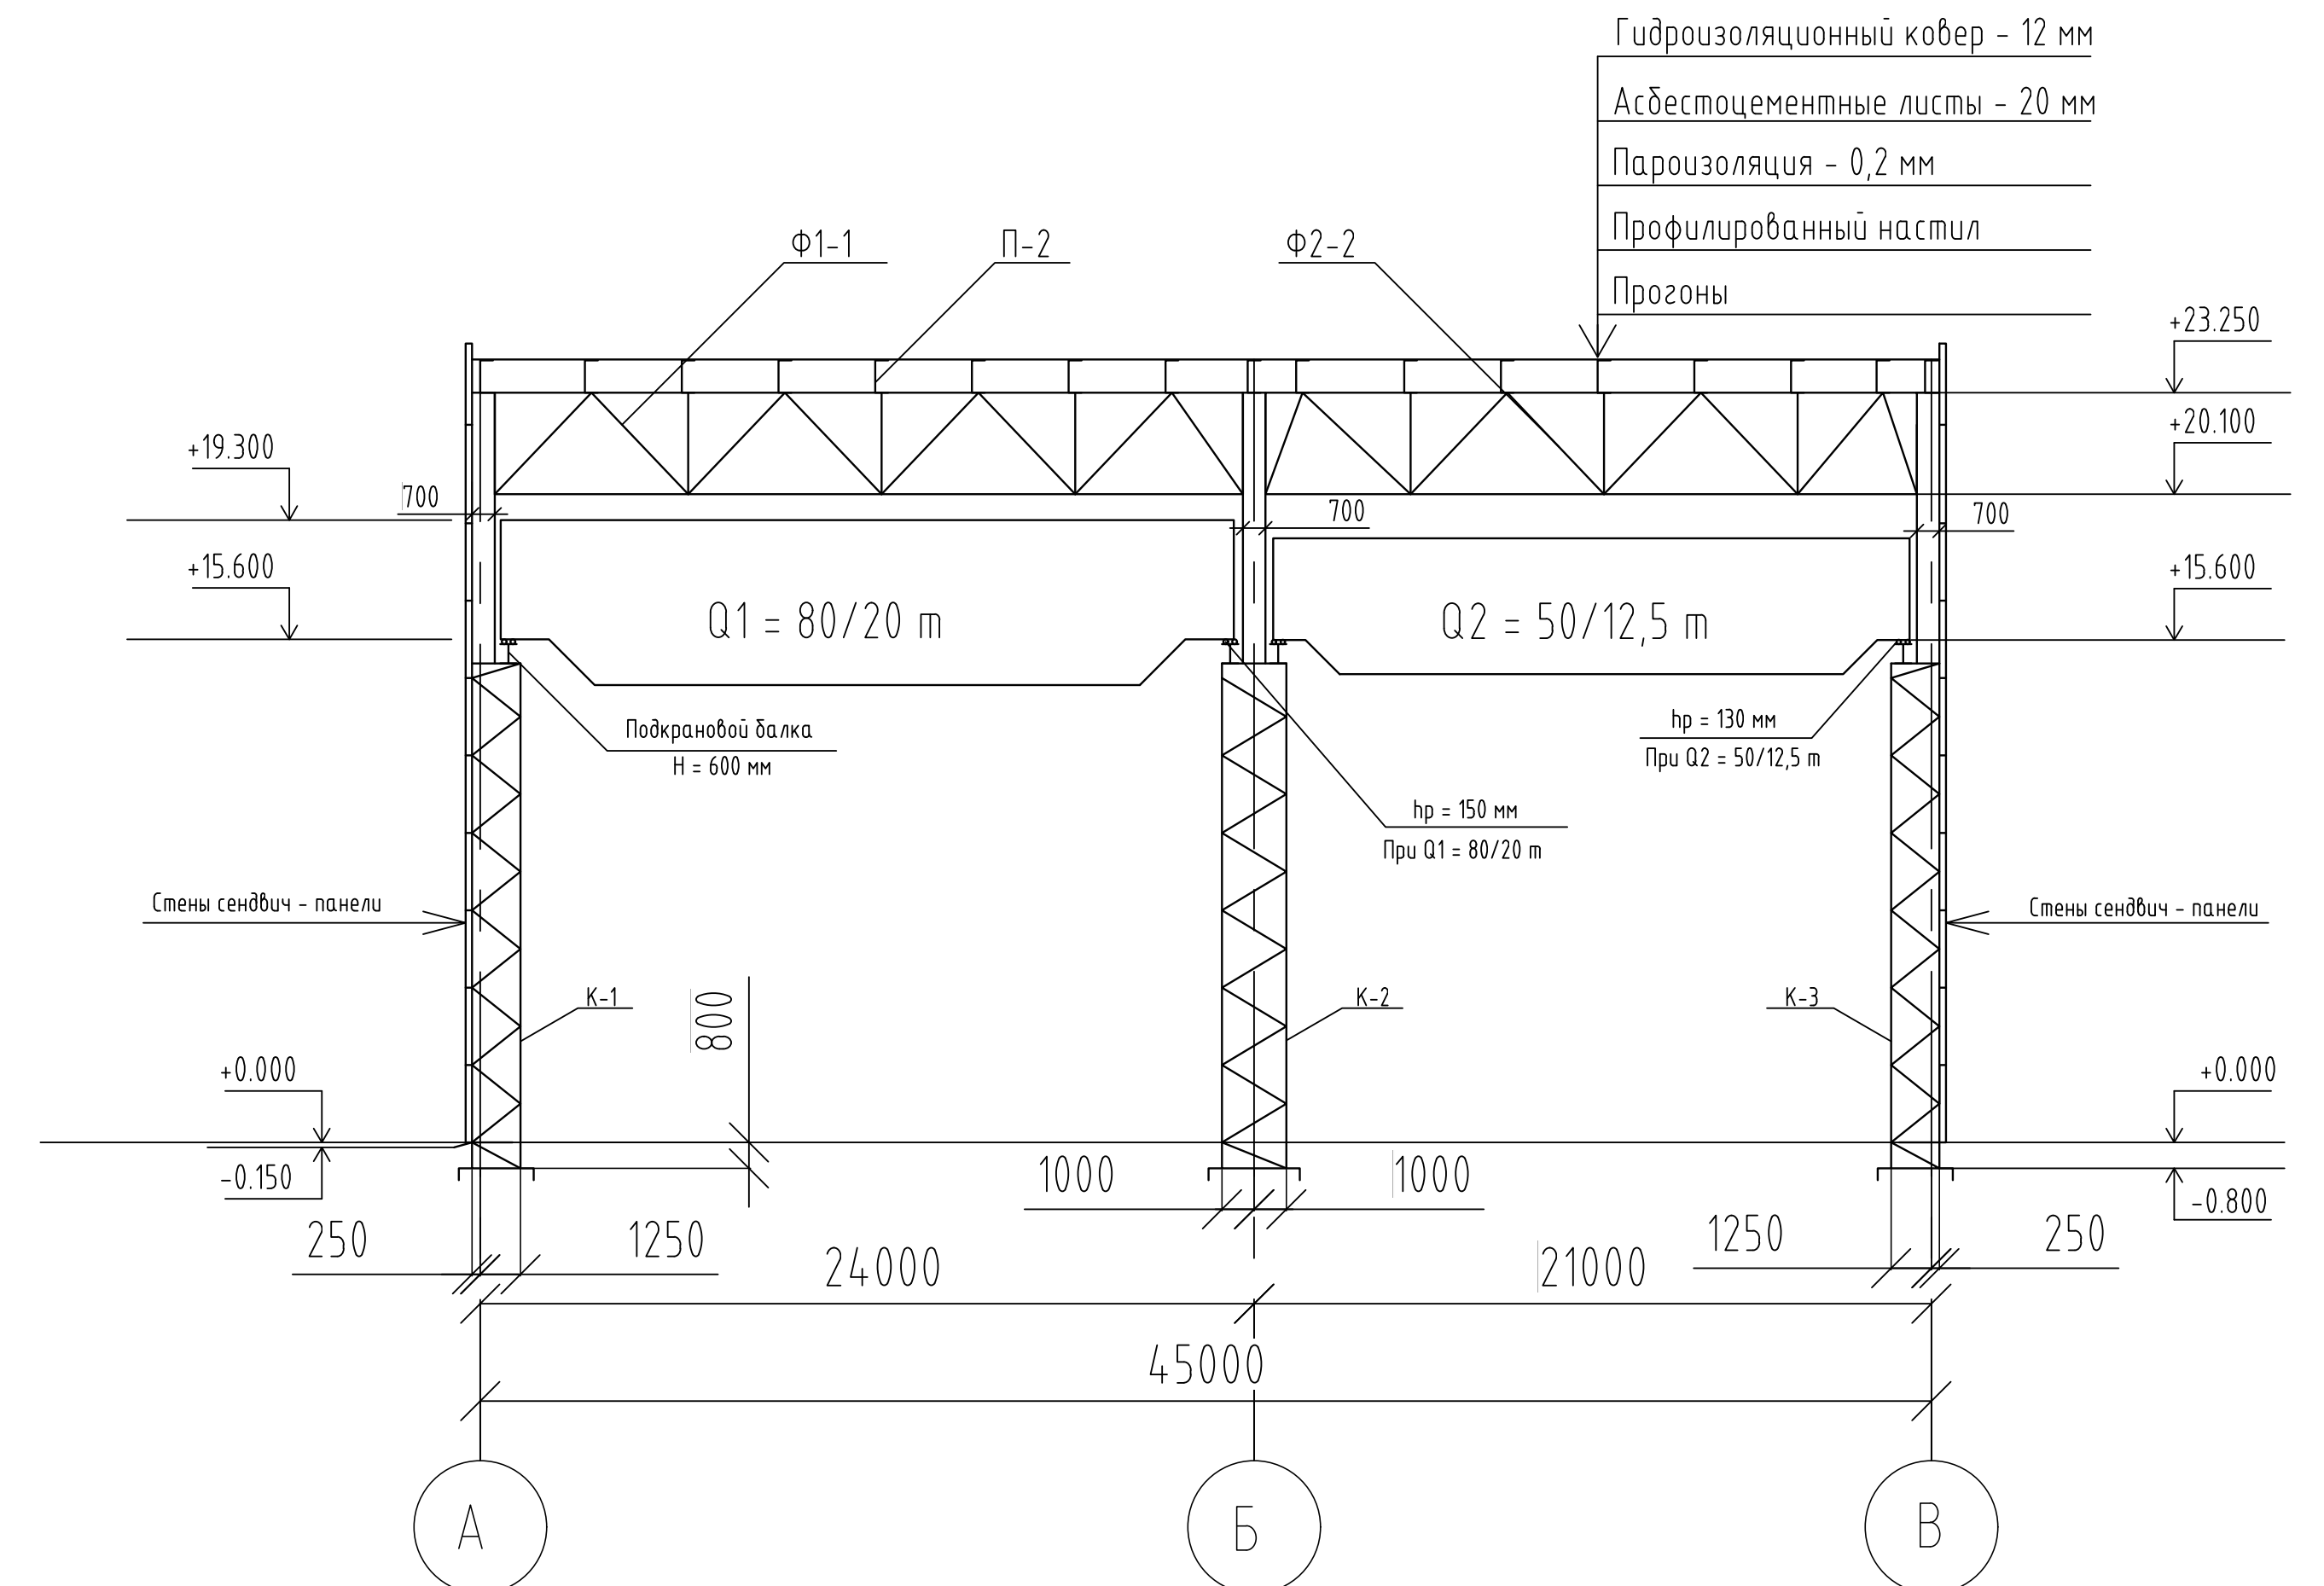

Д.ИСА.08.03.01.320004.ПМ.3.2025-КМД							
Расчет и конструирование основных несущих конструкций одноэтажного промышленного здания							
Изм.	Кол-во	Лист	№ док.	Подпись	Дата		
Студент	Бахри Х.Х.			<i>Х.Х. Бахри</i>	26.05		
Консультант	Карлова				26.05		
Здание цеха							
Консультант							
Руководитель	Карлова				26.05		
№ контр.	Карлова				26.05		
Заб. каф	Белева				26.05		
Схема расположения элементов покрытия в плоскости нижних и верхних поясов ферм					Страница	Лист	Листов
					У	2	5
УрФУ кафедра СКМГ							


Продольный разрез здания

Разрез 2-2(1)

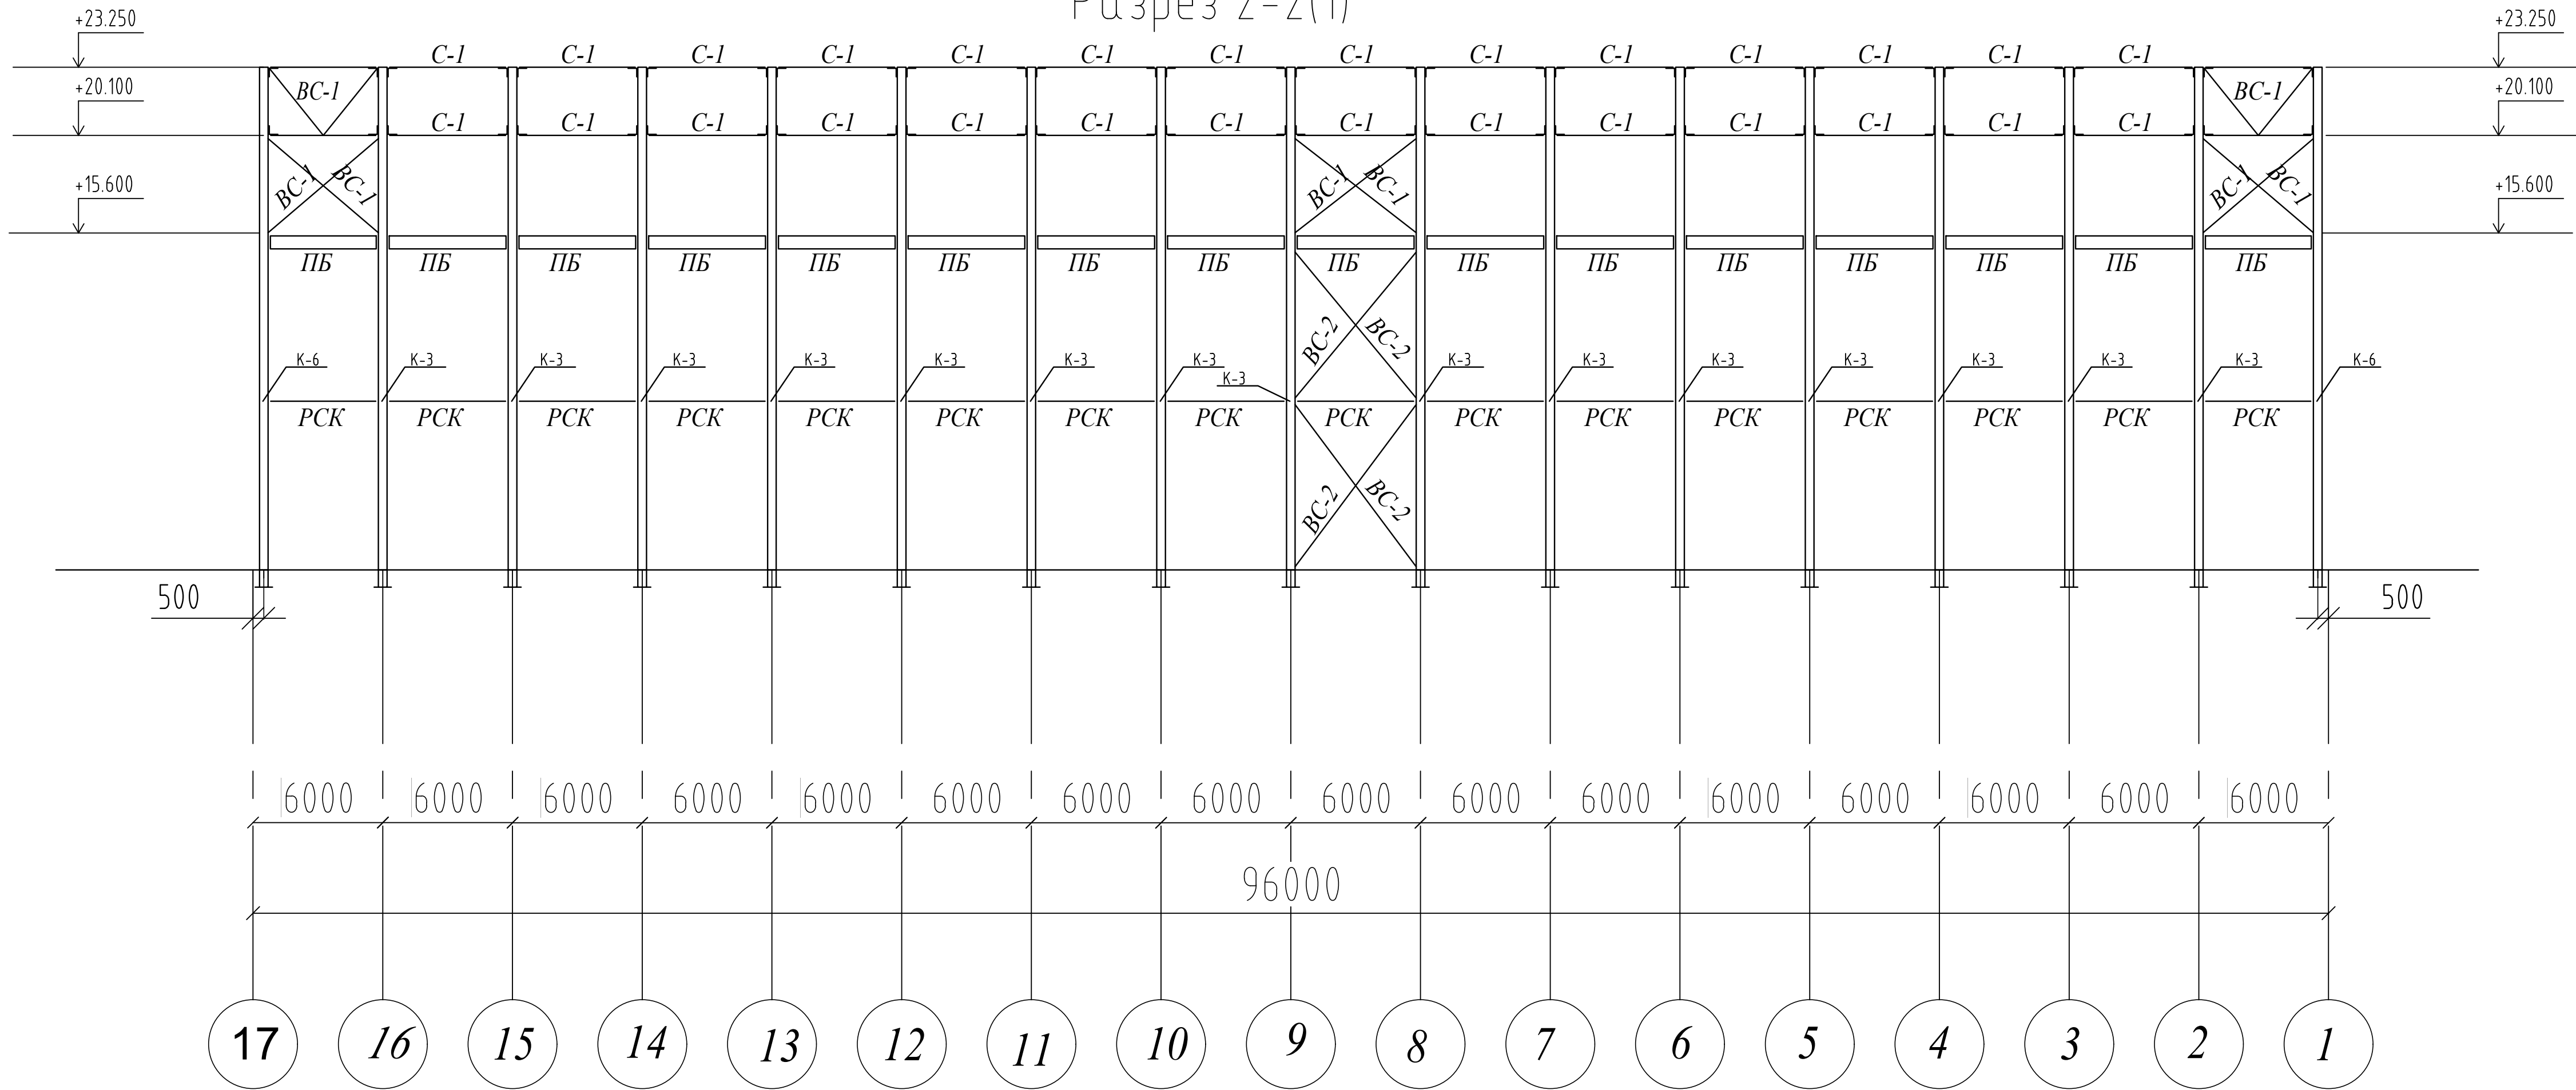


Продольный разрез здания

Разрез 3-3(1)

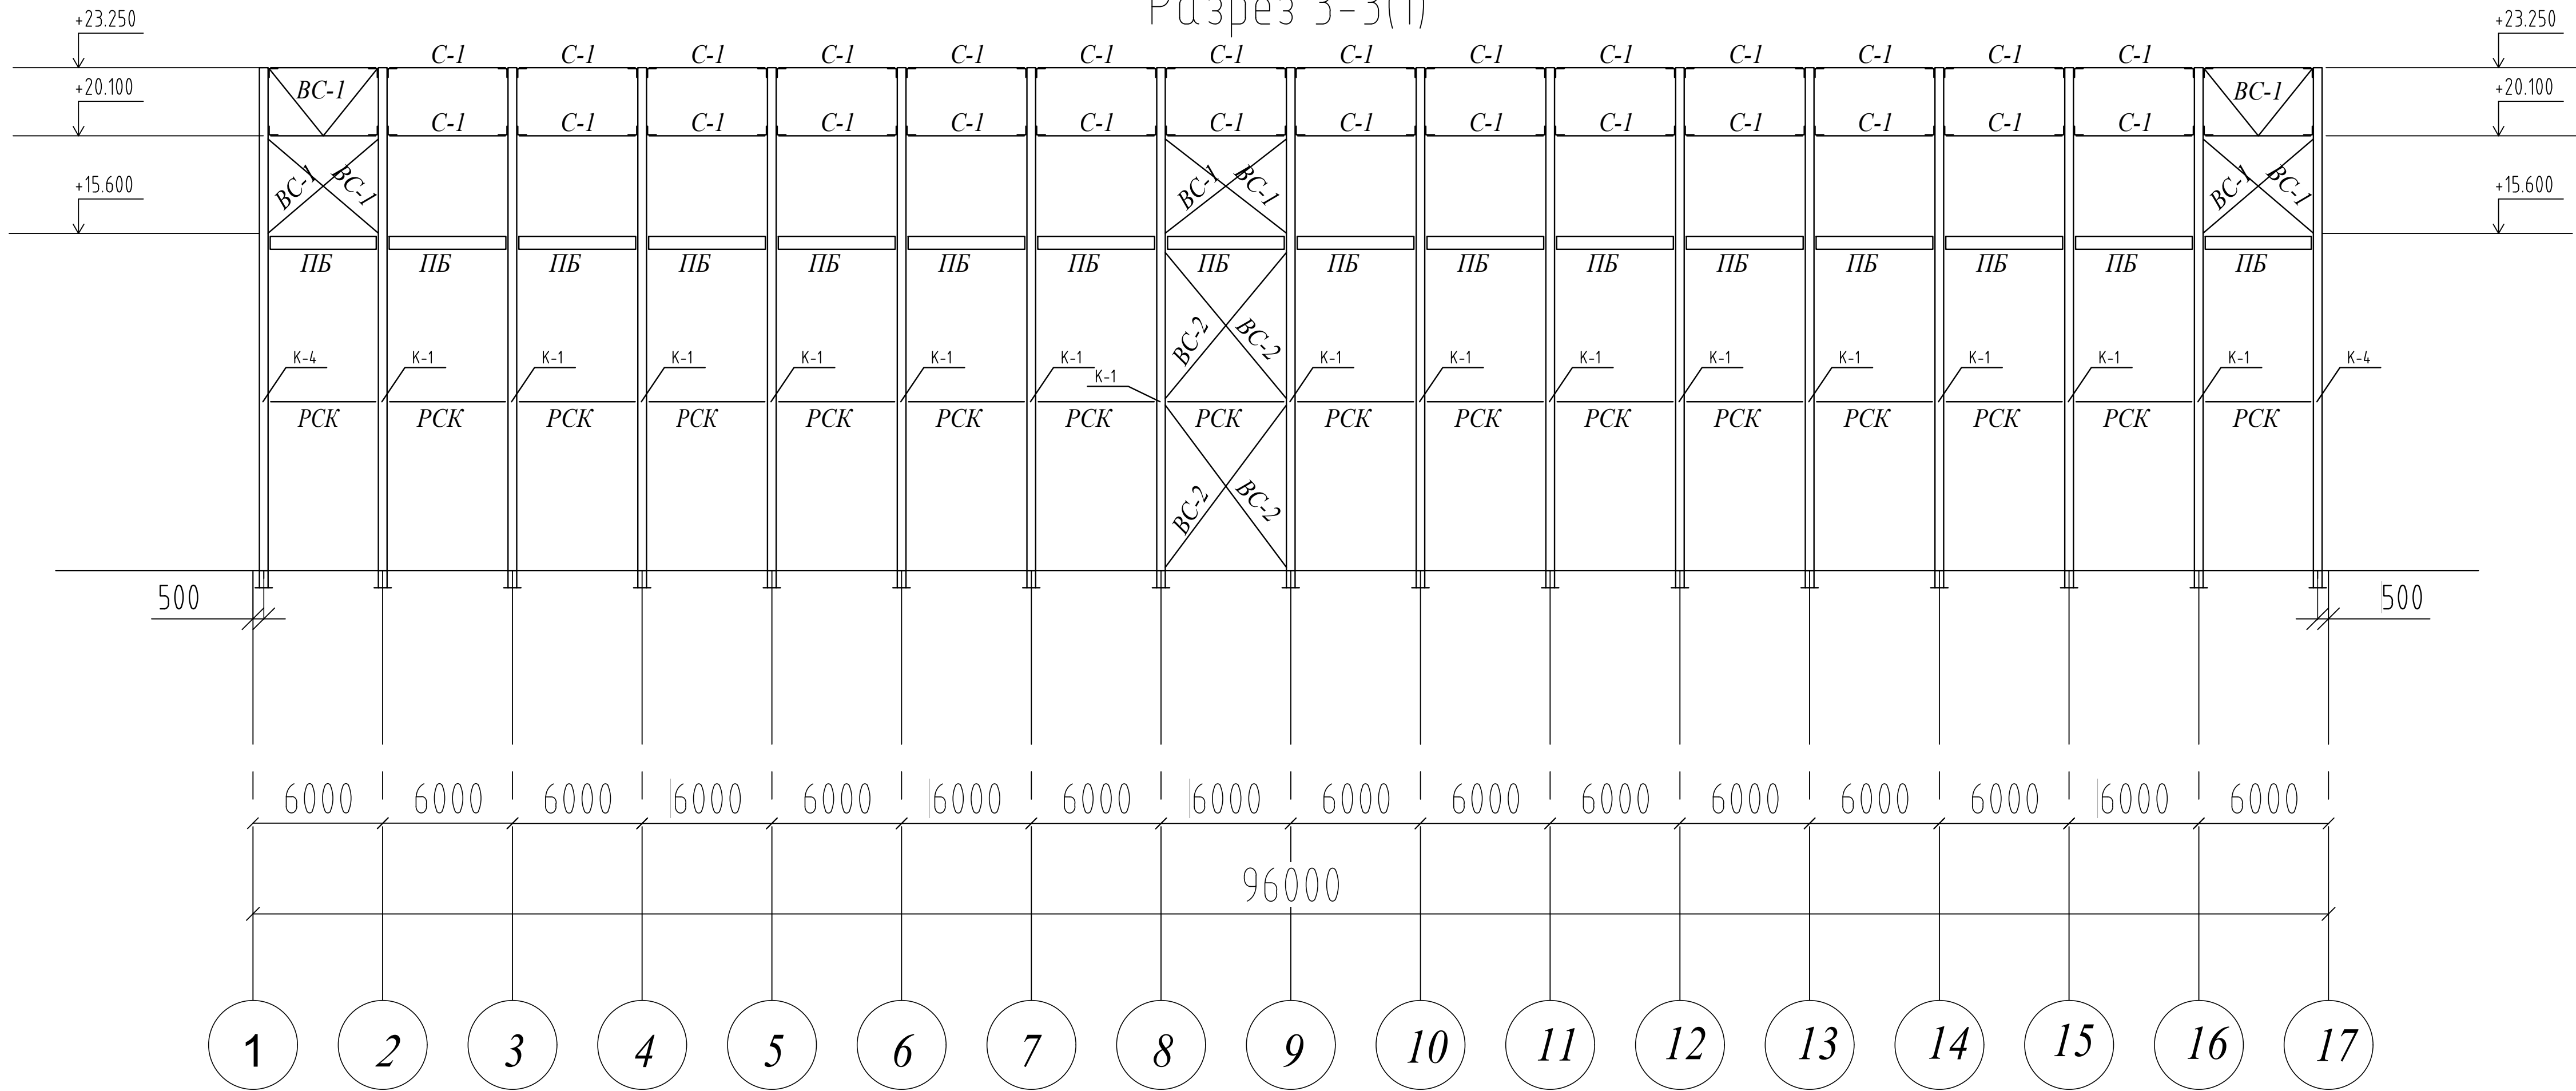


						Д.И.СА.08.03.01.320004.ПМ.3.2025-КМД				
						Расчет и конструирование основных несущих конструкций одноэтажного промышленного здания				
Изм.	Кол-во	Лист	№ док.	Подпись	Дата	Здание цеха	Стадия	Лист	Листов	
Студент			Баффа Х.Х.		26.05					
Консультант			Карлова		26.05		У	3	5	
Консультант						Разрезы 2-2, 3-3	УрФУ кафедра СКМГ			
Руководитель			Карлова		26.05					
Н.контр.			Карлова		26.05					
Заб. каф.			Беляева		26.05					

Отправочная марка ФС-1-1

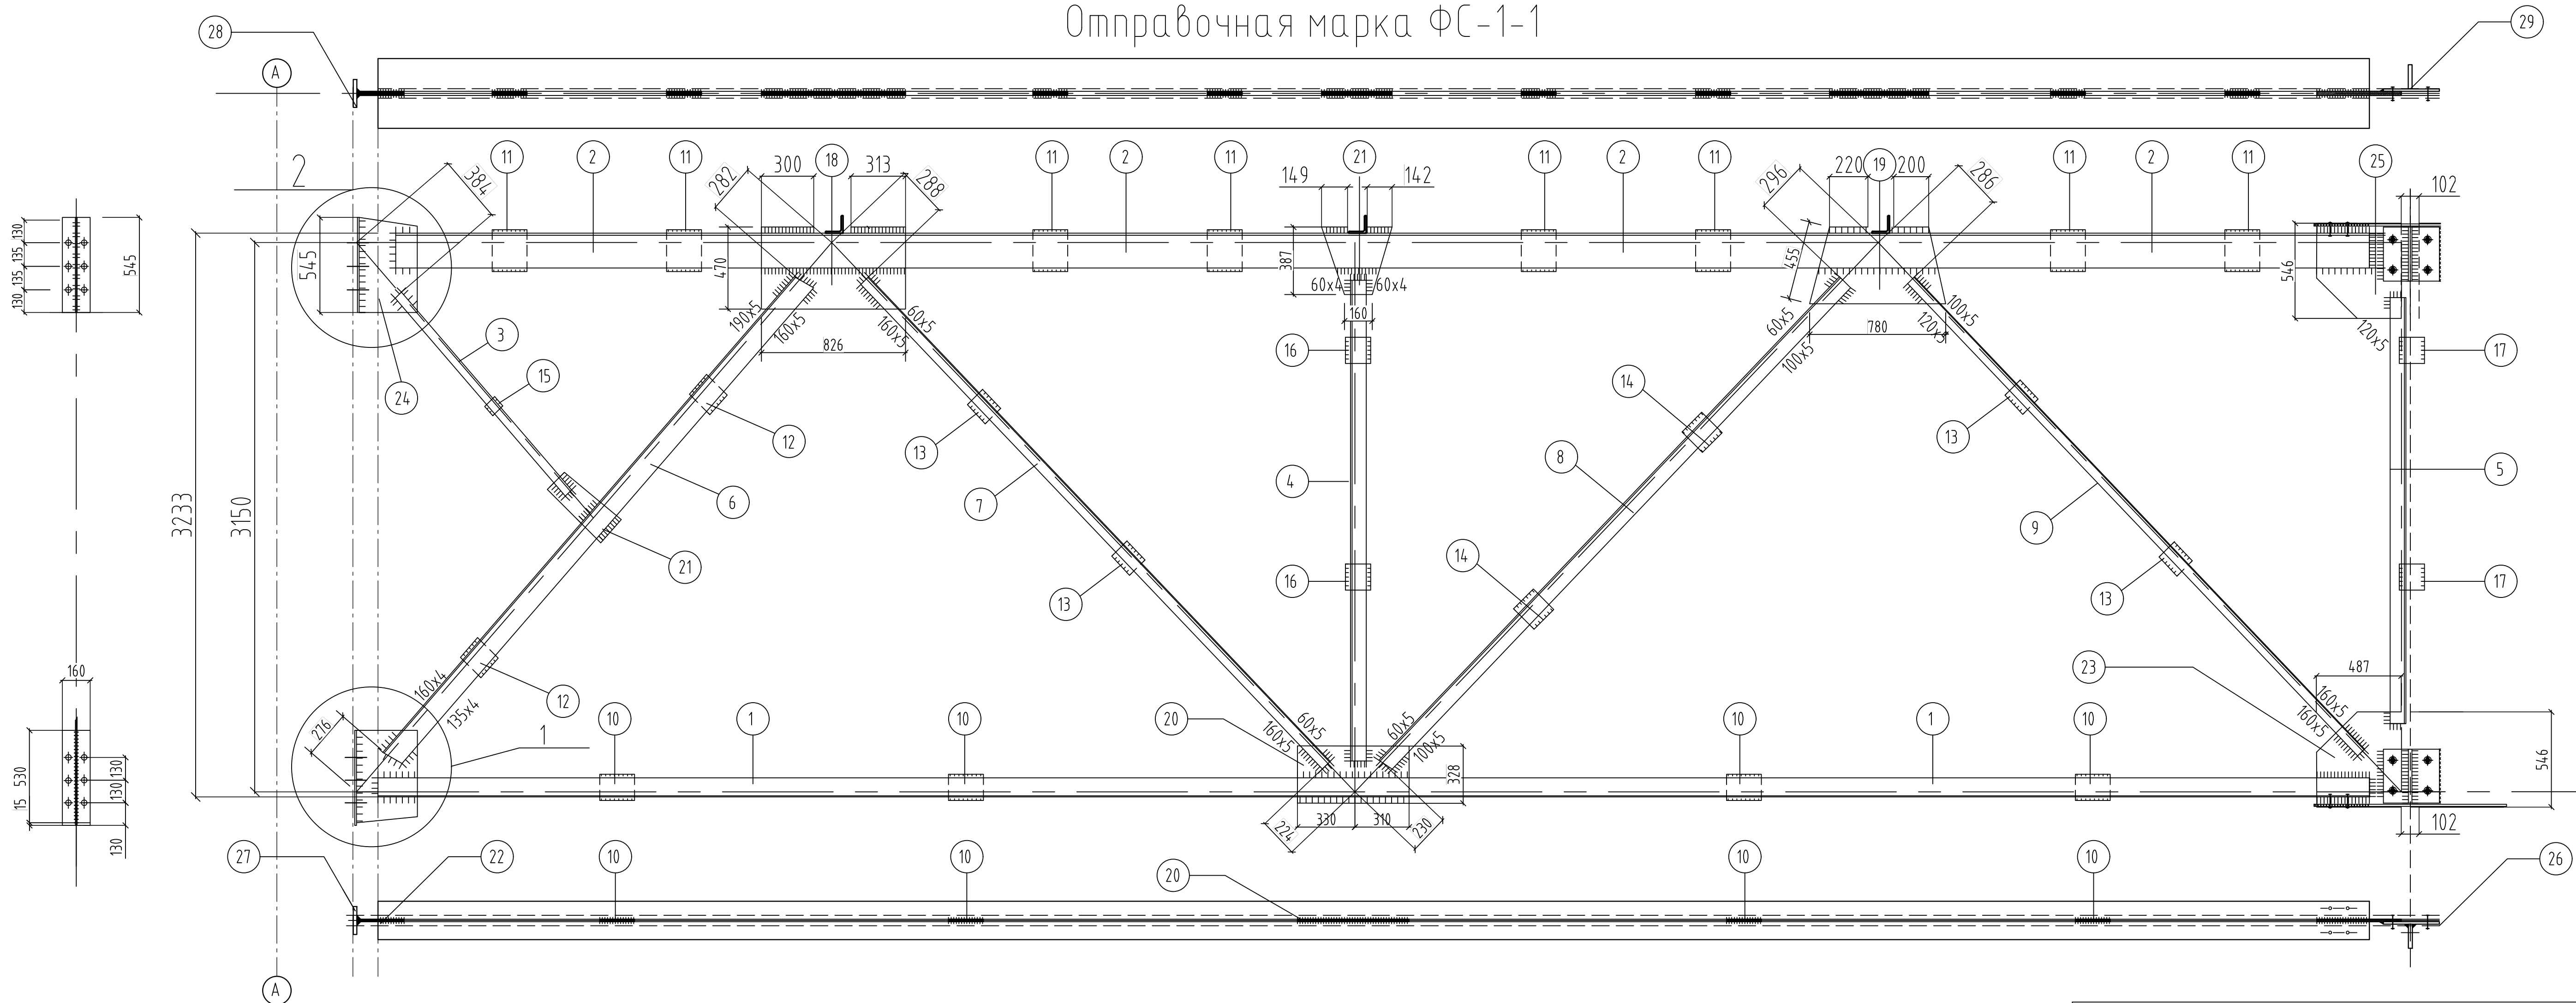

Геометрическая схема фермы Ф-1 с усилиями в кН

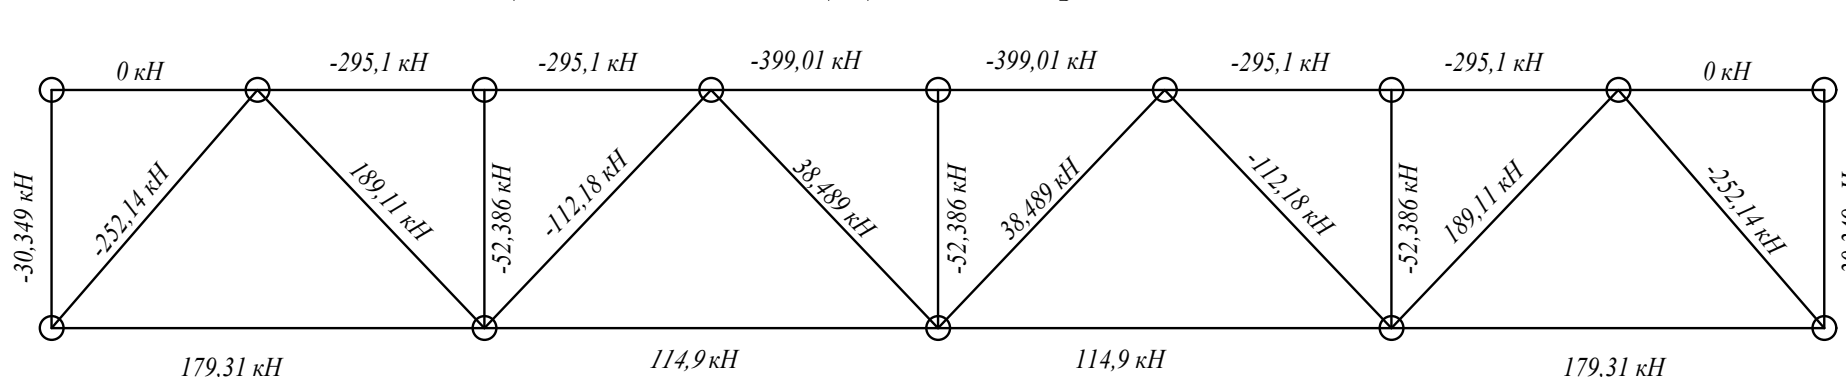

Геометрическая схема фермы Ф-1

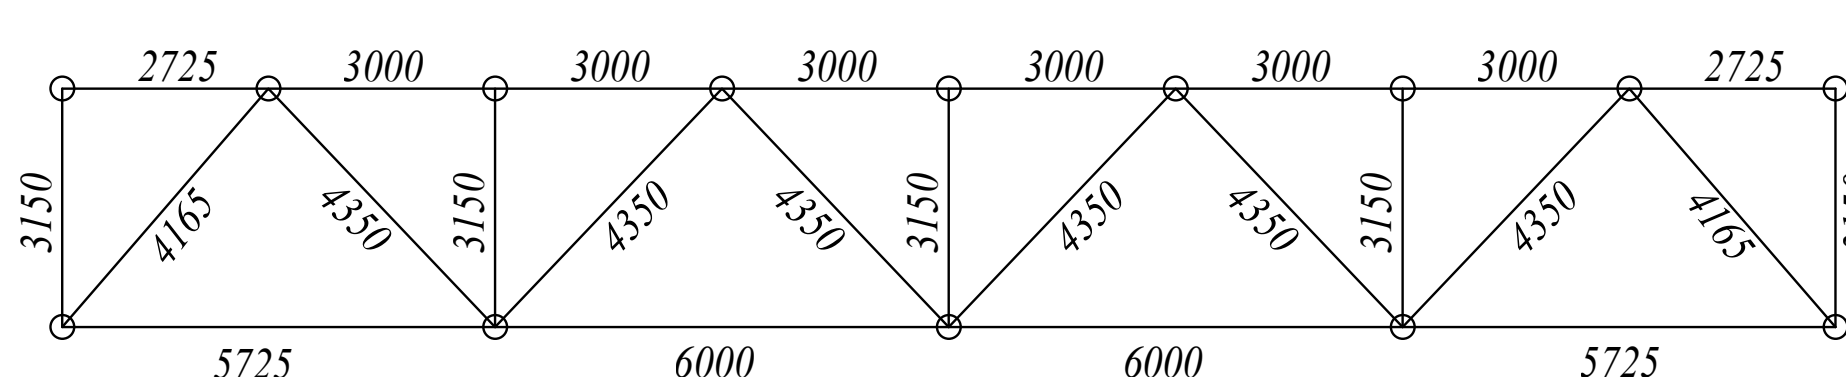


Схема отправочных элементов фермы Ф-1

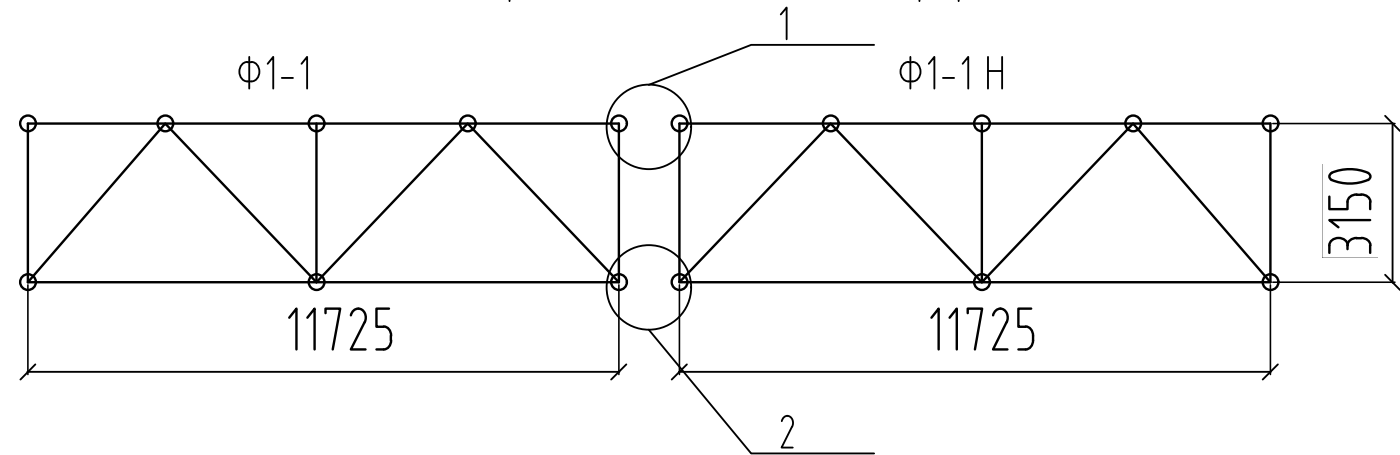


Таблица отправочных марок				
Отпр. марка	К-во		масса в кг	
	Т	Н	марки	общая
Ф1-1	1	1	1509.2	3018.4
			Итого:	3018.4

Спецификация металла

Отпр. марка	Сбор. мар.	К-во		Сечение	Длина	масса в кг			Марка стали	Примечание
		Т	Н			шт.	общ.	о.м.		
Ф1-1	1	1	1	L 110 x 110 x 7	114.19	135.8	271.5	1509.2	С355	
	2	1	1	L 200 x 200 x 12	113.16	418.4	836.7		С355	
	3	1		L 50 x 50 x 5	14.96	5.6	5.6		С355	
	4	1		L 90 x 90 x 9	27.57	33.6	33.6		С355	
	5	1		L 90 x 90 x 9	24.43	29.8	29.8		С355	
	6	1		L 125 x 125 x 8	36.06	55.7	55.7		С355	
	7	1		L 63 x 63 x 6	38.37	21.9	21.9		С355	
	8	1		L 90 x 90 x 9	38.11	46.5	46.5		С355	
	9	1		L 56 x 56 x 5	37.40	15.9	15.9		С355	
	10	4		- 110 x 8	130	0.9	3.6		С355	
	11	8		- 200 x 8	220	2.8	22.4		С355	
	12	2		- 125 x 8	150	1.2	2.4		С355	
	13	4		- 60 x 8	100	0.4	1.6		С355	
	14	2		- 100 x 8	120	0.8	1.6		С355	
	15	1		- 55 x 8	70	0.2	0.2		С355	
	16	2		- 100 x 8	120	0.8	1.6		С355	
	17	2		- 100 x 8	120	0.8	1.6		С355	
	18	1		- 470 x 8	820	24.2	24.2		С355	
	19	1		- 455 x 8	780	22.3	22.3		С355	
	20	1		- 330 x 8	640	13.3	13.3		С355	
	21	1		- 160 x 8	390	3.9	3.9		С355	
	22	1		- 530 x 8	350	11.6	11.6		С355	
	23	1		- 480 x 8	540	16.3	16.3		С355	
	24	1		- 300 x 8	530	10.0	10.0		С355	
	25	1		- 480 x 8	540	16.3	16.3		С355	
	26	1		- 300 x 10	350	8.2	8.2		С355	
	27	1		- 160 x 10	310	3.9	3.9		С355	
	28	1		- 160 x 10	530	6.7	6.7		С355	
	29	1		- 190 x 10	350	5.2	5.2		С355	
наплав. металл 1%						14.9				

Д.И.СА.08.03.01.320004.ПМ.3.2025-КМД

Расчет и конструирование основных несущих конструкций одноэтажного промышленного здания

Здание цеха

Ферма 1-1

Стадия Лист Листов
УрФУ
кафедра СКМГ

- Данный рабочий чертеж стадии КМД разработан на основании чертежа стадии КМ, лист 1.
- Материал конструкций см. - "Спецификация стали".
- Заводские соединения варить проволокой СВ-08Г2С в среде углекислого газа.
- Монтажные соединения - сварные электродами типа Э-46 по ГОСТ 9467-75 и на болтах М16 класса 5.6 по ГОСТ 7798-70х
- Неоговоренные швы катетом kf=6мм. Неоговоренные обрезы 25мм. 7. Все отверстия диаметром $\Phi 20$ мм.